


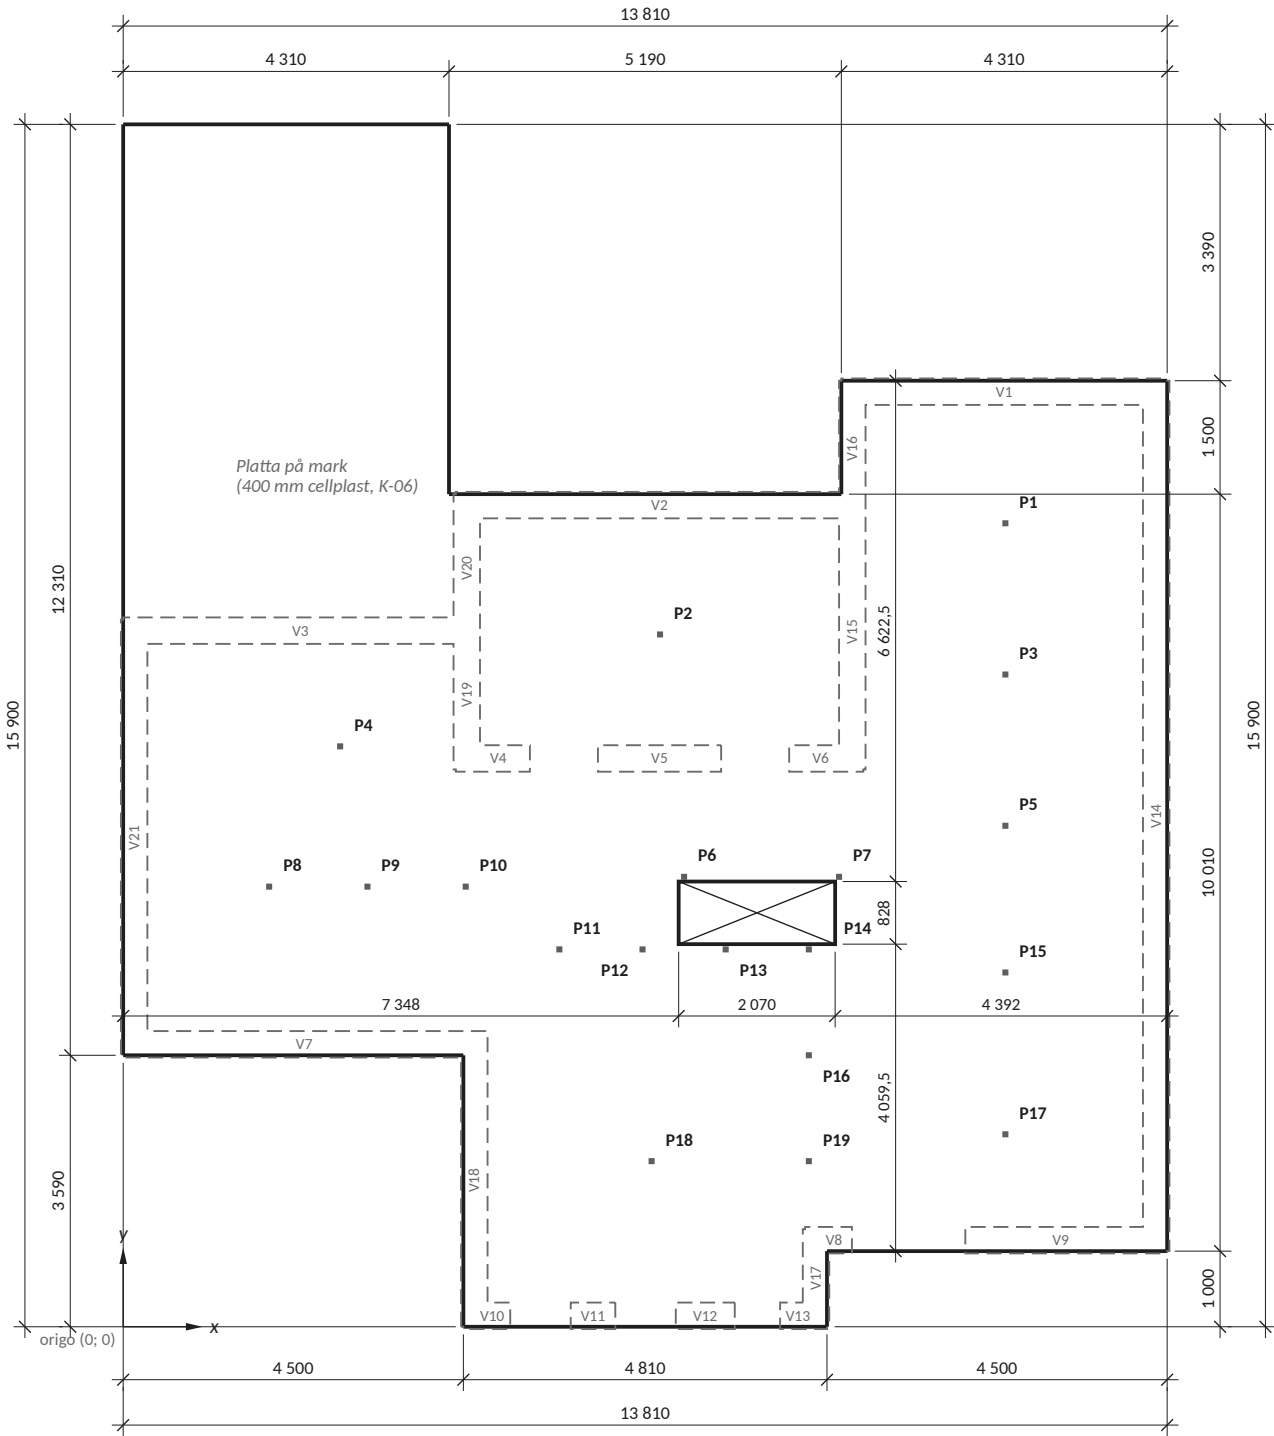

PLAN - ÖVERSIKT OCH YTTERMÅTT

Skala 1:100



Anvisningar

- Betong C25/30, exponeringsklass XC1, livslängd 50 år. Armering B500B.
- Täckskikt: underkant 20 mm, överkant 25 mm, kanter och hållkanter 25 mm.
- Skarvlängd: Ø8 500, Ø10 650, Ø12 750 mm. Skarvar förskjuts minst 1,3 x skarvlängden.
- x-järnen ligger ytterst i båda näten. Tilläggsjärn läggs i nätets lager.
- Koordinater i mm enligt K-05; origo i skärningen mellan plattkanterna x = 0 och y = 0. Mått, se R-03.1.
- Plattans kontur och trapphålets läge enligt denna ritning. Rörens lägen, se tabell på R-03.2.
- Lecaväggarna under plattan streckade (K-06).

Teckenförklaring

- plattans kant
- Lecavägg under plattan
- stålrör VKR 80x80x4 (K-05)

Ritningsförteckning R-03

Ritning	Innehåll	Skala
R-03.1	Översikt och yttermått	1:100
R-03.2	Armering i underkant	1:50
R-03.3	Armering i överkant	1:50
R-03.4	Sektioner, detaljer och stålförteckning	1:5, 1:10, 1:20

Rev	Avser	Datum	Sign
A	Första utgåvan	2026-10-08	VO

PROJEKT

Fritidshus Trebodar, Resö, Tanum

FASTIGHET

Resö 2:66, Tanums kommun · BYGG.2025.2278


INNEHÅLL

Mellanbjälklag Översikt och yttermått

SKALA	FORMAT	DATUM
1:100	A3	2026-10-08
UPPRÄTTAD	GRANSKAD	UNDERLAG
Viktor Ogeman	-	K-05 rev A, K-06
STATUS	REVISION	
FÖR GRANSKNING	A	

RITNINGNUMMER

R-03.1

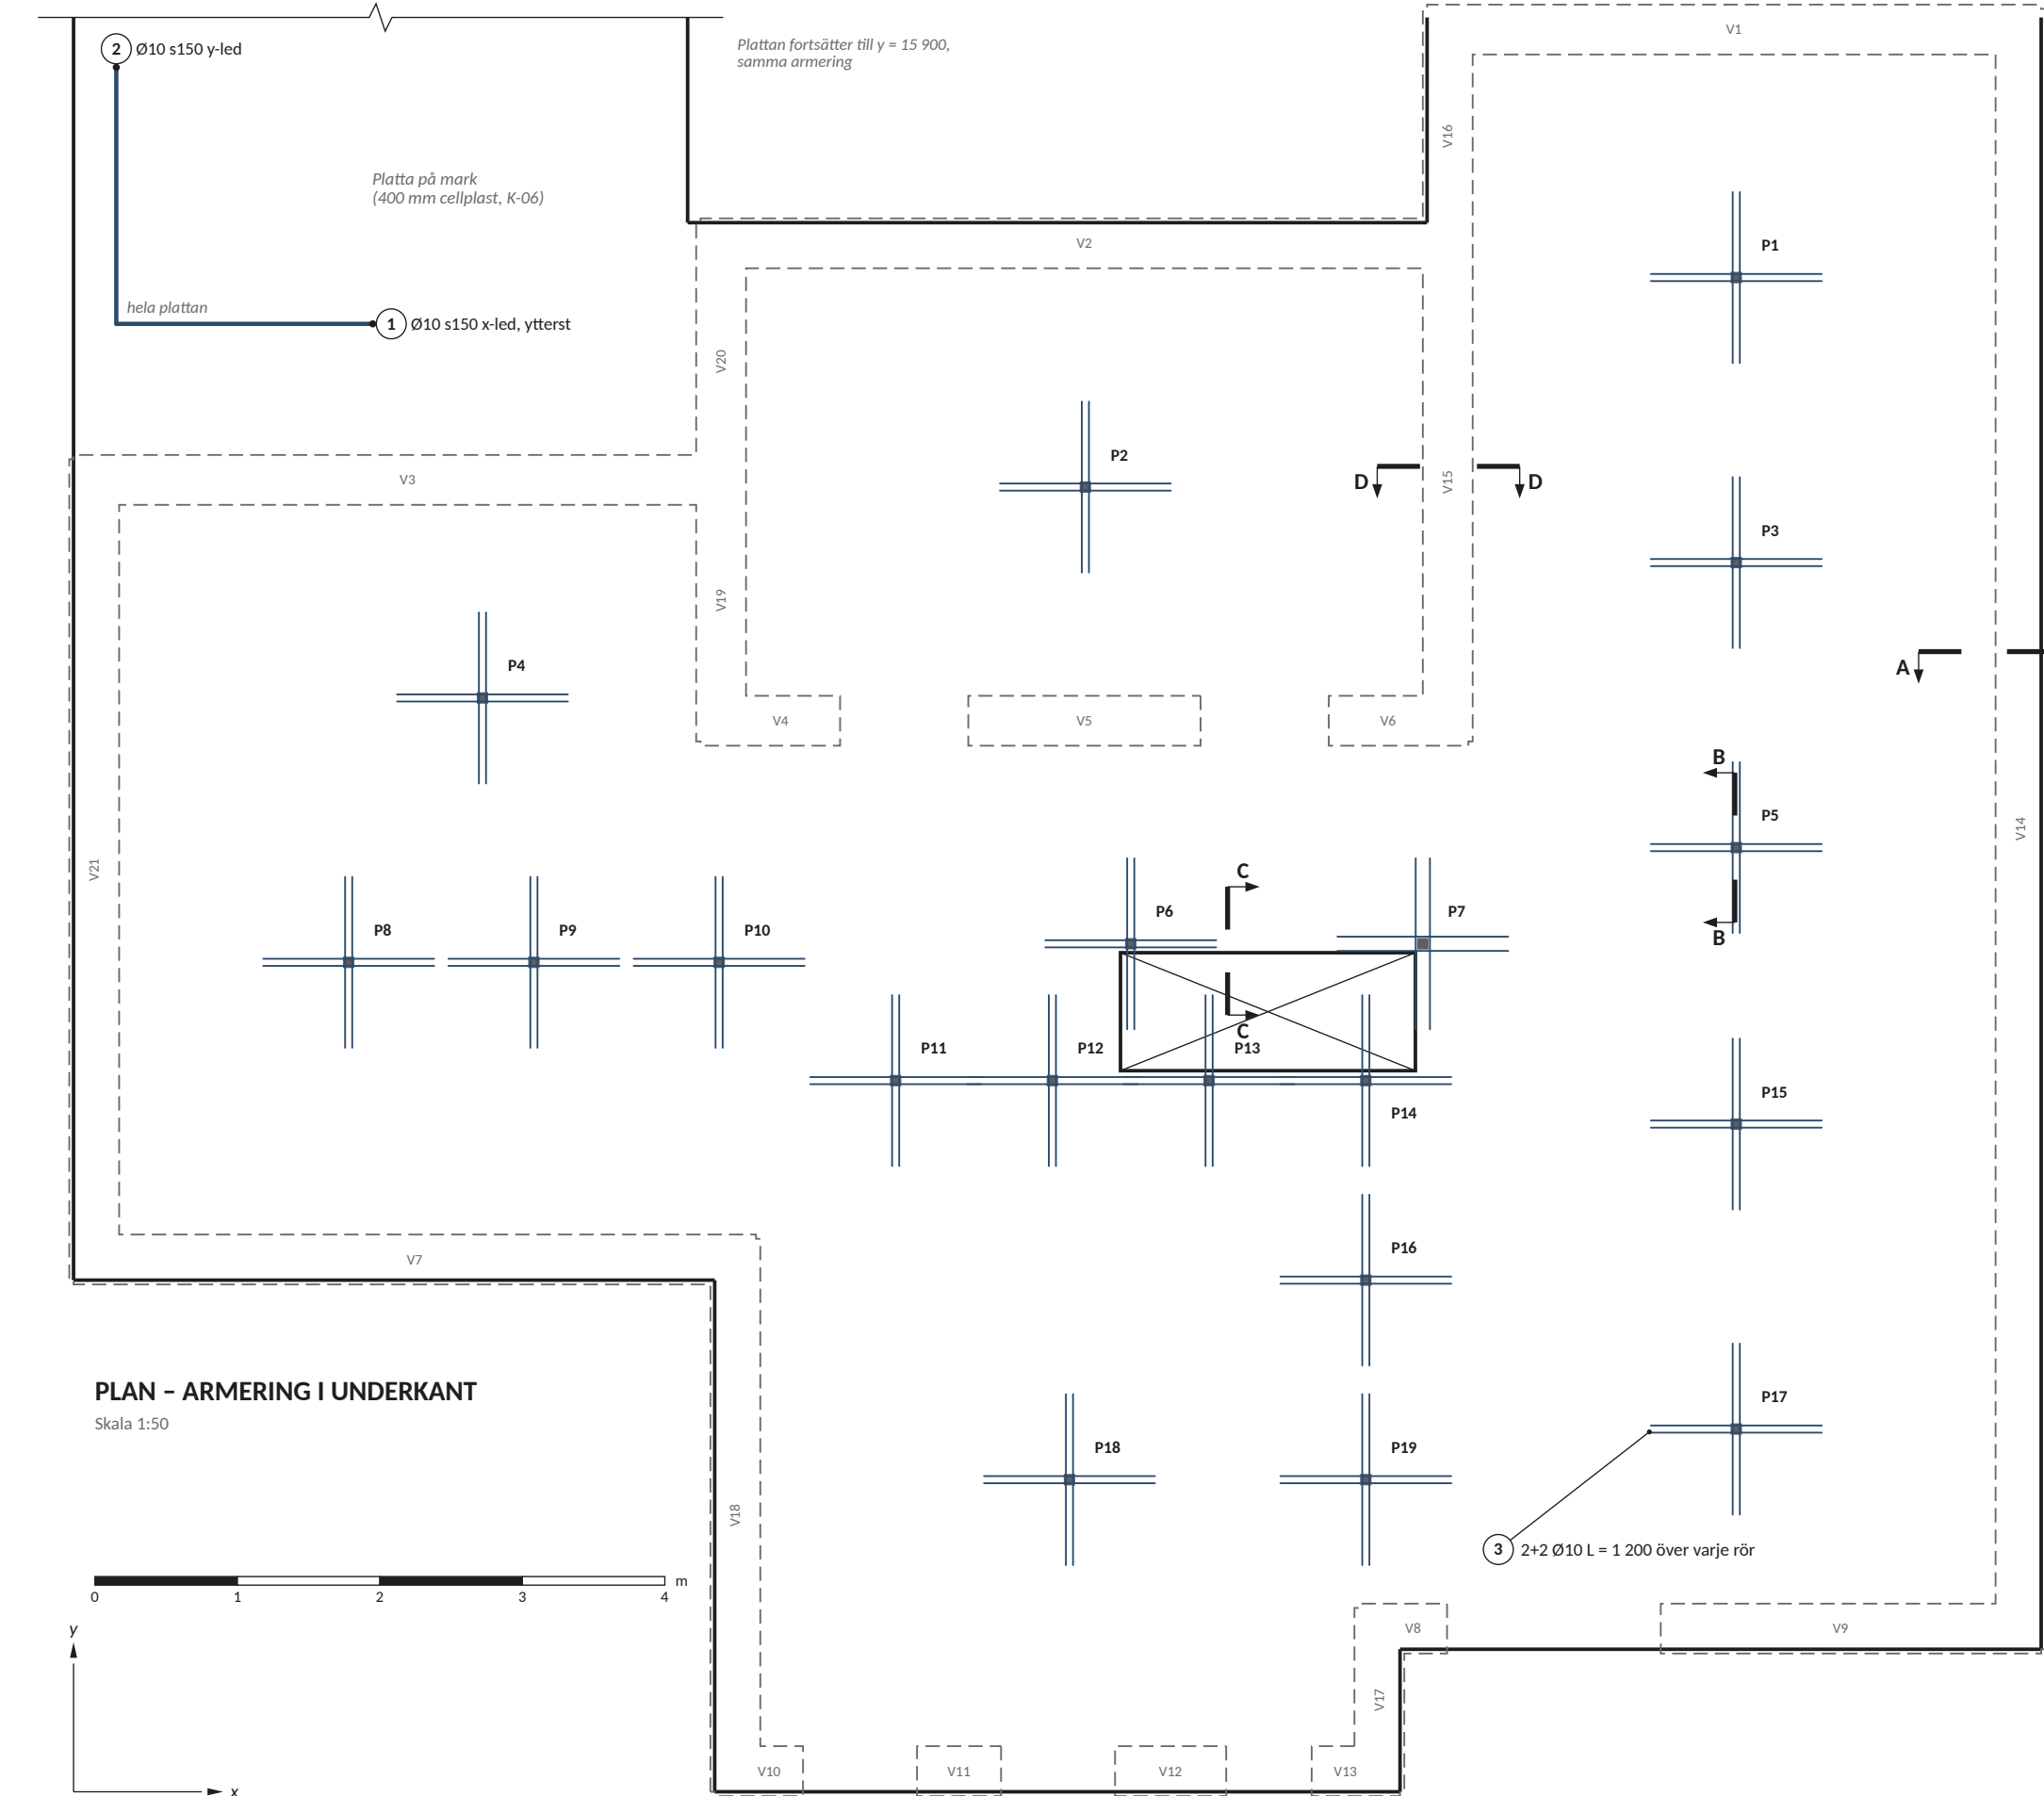

Anvisningar

- Betong C25/30, exponeringsklass XC1, livslängd 50 år. Armering B500B.
- Täckskikt: underkant 20 mm, överkant 25 mm, kanter och hållkanter 25 mm.
- Skarvlängd: Ø8 500, Ø10 650, Ø12 750 mm. Skarvar förskjuts minst 1,3 x skarvlängden.
- x-järnen ligger ytterst i båda näten. Tilläggsjärn läggs i nätets lager.
- Koordinater i mm enligt K-05; origo i skärningen mellan plattkanterna x = 0 och y = 0. Mått, se R-03.1.
- Underkantsnätet läggs på distanser 20 mm, högst 0,8 m isär.
- Minst två underkantsjärn i vardera riktningen ska passera över varje rör (SS-EN 1992-1-1 9.4.1(3)): pos 3, bundna till nätet.
- Överkant, se R-03.3. Sektioner A–D, se R-03.4.

Teckenförklaring

- armering i underkant
- positionsnummer (stålförteckning R-03.4)
- Lecavägg under plattan
- stålrör VKR 80×80×4 (K-05)

Rör och topplåtar

Rör	x	y	Topplåt
P1	11 670	10 625	80×80×8
P2	7 102	9 155	80×80×8
P3	11 670	8 625	80×80×8
P4	2 870	7 675	80×80×8
P5	11 670	6 625	80×80×8
P6	7 420	5 950	80×80×8
P7	9 470	5 950	160×160×25 S355
P8	1 931	5 820	80×80×8
P9	3 231	5 820	80×80×8
P10	4 531	5 820	80×80×8
P11	5 770	4 990	80×80×8
P12	6 870	4 990	80×80×8
P13	7 970	4 990	80×80×8
P14	9 070	4 990	80×80×8
P15	11 670	4 685	80×80×8
P16	9 070	3 590	80×80×8
P17	11 670	2 545	80×80×8
P18	6 990	2 190	80×80×8
P19	9 070	2 190	80×80×8

Rev	Avser	Datum	Sign
A	Första utgåvan	2026-10-08	VO

PROJEKT

Fritidshus Trebodar, Resö, Tanum

FASTIGHET

Resö 2:66, Tanums kommun · BYGG.2025.2278

INNEHÅLL

Mellanbjälklag
Armering i underkant

KALA	FORMAT	DATUM
1:50	A3	2026-10-08
UPPRÄTTAD	GRANSKAD	UNDERLAG
Viktor Ogeman	–	K-05 rev A, K-06
STATUS		REVISION
FÖR GRANSKNING		A
RITNINGSNUMMER		

R-03.2



1. Allmänt, se R-03.2. Mått R-03.1, sektioner R-03.4.
2. Överkantsnätet läggs på armeringsstolar, högst 0,8 m isär.
3. Tilläggsjärnen i zonerna 01–017 läggs i båda riktningarna i nätets lager och binds till nätet (S150: mitt emellan nätets järn). Där zonen närliggande kant förs järnen ut till kanten.
4. Stålstolparnas plåtar (E) gäller system A i K-06. Gjuts in i underkant, se R-03.4.
5. Förankringsjärnen på 14 sätts i U-blocket innan bjälklaget gjuts.

- armering i överkant
- zon med tilläggsjärn i överkant
- fördelning av järn med samma position
- Lecavägg eller plåt under plattan
- stålrör VKR 80×80×4 (K-05)

Zon	Järn	x-led	y-led	x (m)	y (m)
01	Ø12 ≤150	8 st, 300-1 500	7 st, 850-1 250	4,03-5,15	10,18-11,41
02	Ø8 ≤150	7 × 900	6 × 1 100	0,00-0,90	8,62-9,71
03	Ø8 ≤150	7 × 1 000	7 × 1 050	6,57-6,74	8,60-8,91
04	Ø8 ≤150	8 × 1 050	7 × 1 200	2,28-3,32	7,17-8,33
05	Ø12 ≤150	8 × 1 450	10 × 1 150	8,91-10,34	6,91-8,06
06	Ø8 ≤150	7 × 1 200	8 × 1 050	3,95-5,11	6,96-7,99
07	Ø8 ≤150	10 × 1 500	10 × 1 500	10,92-12,42	5,88-7,38
08	Ø12 ≤100	15 st, 800-1 500	15 st, 800-1 500	8,72-10,22	5,20-6,70
09	Ø10 ≤150	10 × 1 500	10 × 1 500	3,78-5,28	5,07-6,57
010	Ø8 ≤150	6 st, 450-1 050	7 st, 600-900	6,92-7,92	5,62-6,48
011	Ø10 ≤150	10 st, 400-1 500	10 st, 800-1 500	8,32-9,82	4,22-5,54
012	Ø8 ≤150	6 × 1 000	7 × 950	5,23-6,22	4,44-5,34
013	Ø8 ≤150	8 st, 850-1 200	8 st, 800-1 150	4,20-5,36	3,28-4,41
014	Ø8 ≤150	6 × 900	6 × 950	8,73-9,61	3,14-4,04
015	Ø10 ≤150	10 × 1 500	10 × 1 500	10,92-12,42	1,79-3,29
016	Ø8 ≤150	7 × 1 050	7 × 1 150	6,40-7,74	1,65-2,75
017	Ø8 ≤150	13 st, 750-1 150	8 st, 1 700-1 900	8,54-9,69	0,79-2,69

Rev	Avser	Datum	Sign
A	Första utgåvan	2026-10-08	VO

PROJEKT

Fritidshus Trebodard, Resö, Tanum


FASTIGHET

Resö 2:66, Tanums kommun · BYGG.2025.2278

INNEHÅLL


Mellanbjälklag Armering i överkant

SKALA	FORMAT	DATUM
1:50	A3	2026-10-08
UPPRÄTTAD	GRANSKAD	UNDERLAG
Viktor Ogeman	-	K-05 rev A, K-06
STATUS		REVISION
FÖR GRANSKNING		A
RITNINGSNUMMER		

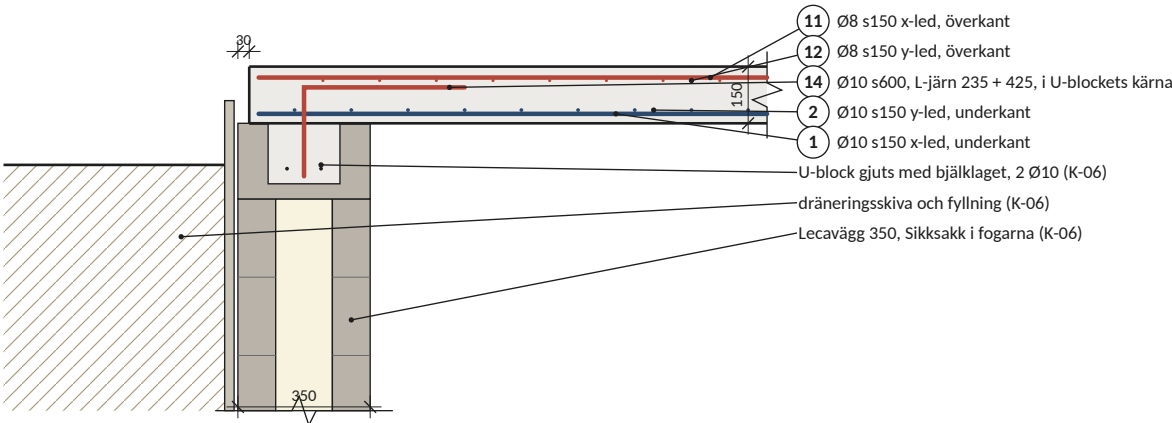


SEKTION A-A Yttervägg mot jord (V14)

Skala 1:20

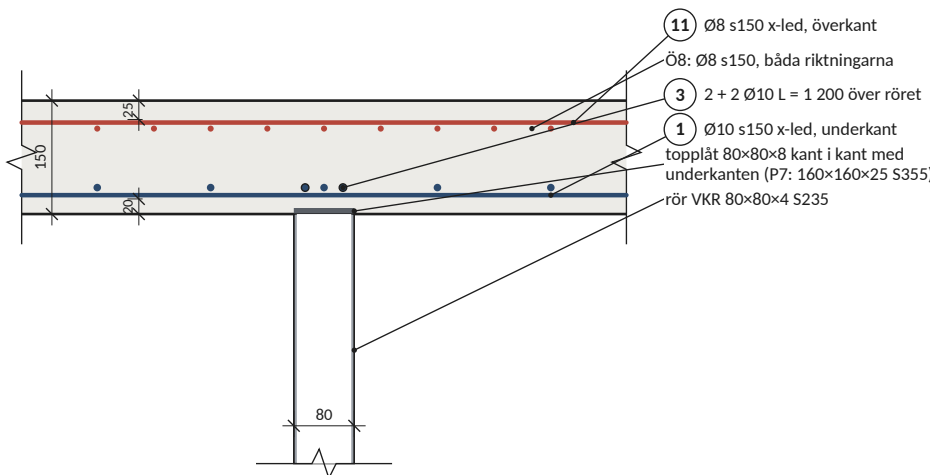


SEKTION B-B Vid rör (P5)

Skala 1:10

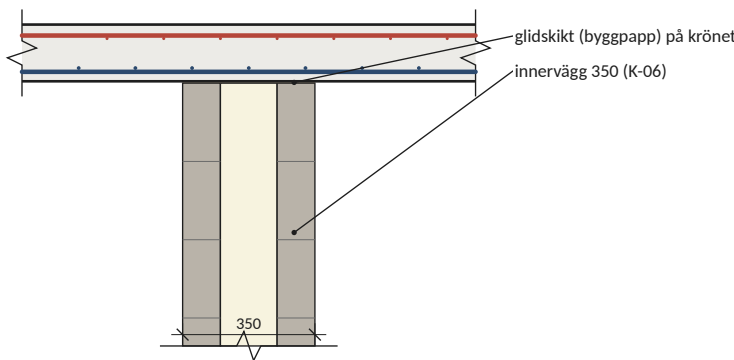


SEKTION D-D Innervägg (V15)

Skala 1:20

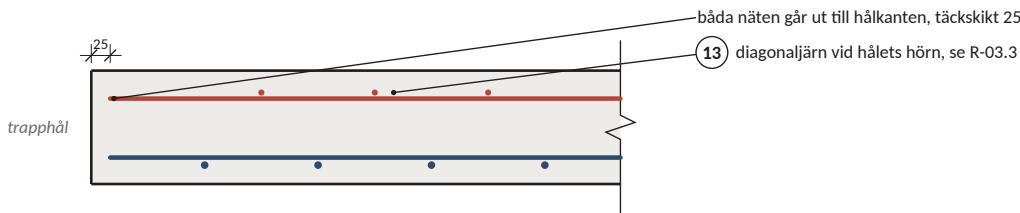

SEKTION C-C Trapphålets kant

Skala 1:10

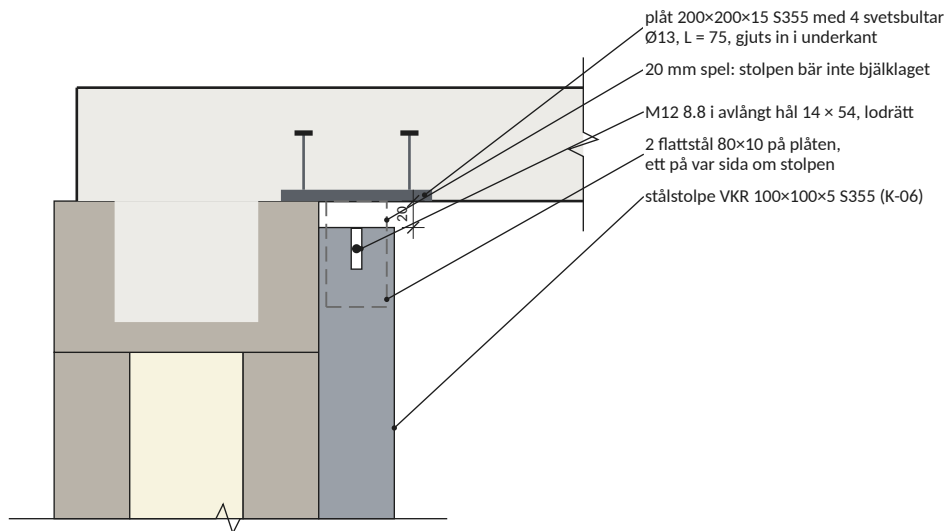


DETALJ E Stålstolpens topp, system A (K-06)

Skala 1:10

Stålförteckning, B500B

Pos	Ø	Form	s	Antal	L (mm)	Total (m)	Vikt (kg)	Anm
1	Ø10	rak	s150	122	var.	1 063	656	UK x-led
2	Ø10	rak	s150	106	var.	1 057	652	UK y-led
11	Ø8	rak	s150	122	var.	1 057	417	ÖK x-led
12	Ø8	rak	s150	106	var.	1 053	416	ÖK y-led
3	Ø10	rak	-	76	1 200	91	56	UK över rören
13	Ø10	rak	-	16	1 200	19	12	ÖK diagonalt
14	Ø10	L 235+425	s600	86	660	57	35	U-block
Ö-Ø8	Ø8	rak	-	166	var.	186	74	zoner R-03.3
Ö-Ø10	Ø10	rak	-	60	var.	80	49	zoner R-03.3
Ö-Ø12	Ø12	rak	-	63	var.	71	63	zoner R-03.3
Summa							2 431	Ø8: 907 + Ø10: 1 460 + Ø12: 63

Näten raknade över hela plattan (även plattan på mark) med en skarv per 12 m stång. Skarvslängd Ø8 500, Ø10 650, Ø12 750 mm.

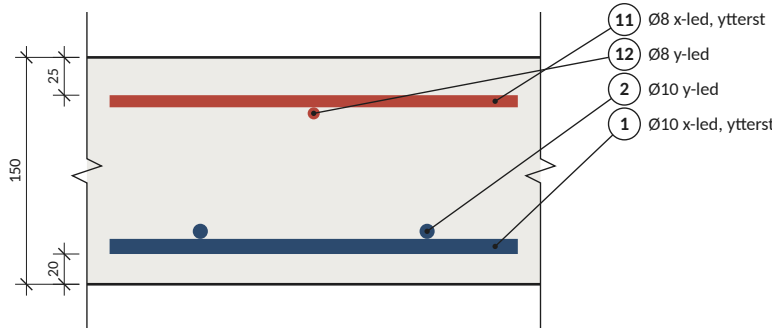

DETALJ F Armeringens lägen

Skala 1:5

Anvisningar

- Betong C25/30, exponeringsklass XC1, livslängd 50 år. Armering B500B.
- Täckskikt: underkant 20 mm, överkant 25 mm, kanter och hållkanter 25 mm.
- Skarvlängd: Ø8 500, Ø10 650, Ø12 750 mm. Skarvar förskjuts minst 1,3 x skarvlängden.
- x-järnen ligger ytterst i båda näten. Tilläggsjärn läggs i nätets lager.
- Rörens topplåt gjuts in kant i kant med plattans underkant. Röret centreras under plåten.
- U-blocket i ytterväggarna gjuts samtidigt med bjälklaget. Pos 14 sätts i U-blocket före gjutning.
- Innerväggarna får glidskikt (byggpapp) på krönet.
- Detalj E gäller stål stolparna i system A (K-06): V14 och V21.
- Plan: underkant R-03.2, överkant R-03.3.

Teckenförklaring

- armering i underkant
- armering i överkant
- betong C25/30
- Leca (lättklinker)
- isolering
- fyllning
- stål

Rev	Avser	Datum	Sign
A	Första utgåvan	2026-10-08	VO

PROJEKT

Fritidshus Trebodar, Resö, Tanum

FASTIGHET

Resö 2:66, Tanums kommun · BYGG.2025.2278

INNEHÅLL

Mellanbjälklag Sektioner, detaljer och stålförteckning

SKALA	FORMAT	DATUM
1:5, 1:10, 1:20	A3	2026-10-08
UPPRÄTTAD	GRANSKAD	UNDERLAG
Viktor Ogeman	–	K-05 rev A, K-06
STATUS		REVISION
FÖR GRANSKNING		A
RITNINGSNUMMER		

R-03.4