## Plan 1, golvet, belysningsstyrka

Skala 1:75




### Belysningsstyrka, lux

5 000
2 000
1 000
750
500
300
200
150
100
75
50
20
10
0

### Rum och delområden, lux

| Rum | Medel | Min | Max | Jämnhet $U_0$ |
|---|---|---|---|---|
| Allrum | 125 | 26 | 197 | 0,21 |
| Badrum | 323 | 155 | 373 | 0,48 |
| Bänken längs 3NV (0,91 m) | 651 | 192 | 899 | 0,30 |
| Bänken längs 3SV (0,91 m) | 240 | 93 | 535 | 0,39 |
| Gästrum | 49 | 44 | 52 | 0,90 |
| Gång | 123 | 52 | 206 | 0,42 |
| Hall | 102 | 75 | 163 | 0,73 |
| Kontor | 200 | 105 | 319 | 0,52 |
| Kontor, litet | 50 | 41 | 59 | 0,81 |
| Kök | 249 | 40 | 530 | 0,16 |
| Sovrum | 37 | 16 | 73 | 0,43 |
| Sovrum, litet | 197 | 153 | 219 | 0,78 |
| Trappa | 129 | 89 | 185 | 0,69 |
| Vardagsrum | 250 | 125 | 394 | 0,50 |
| Ön (0,91 m) | 811 | 182 | 2 020 | 0,22 |

### Anvisningar

1. Belysningsstyrkan på en vågrät yta 0,04 m över golvet, i rutor om 50 mm, ur renderingen i Blender (Cycles): armaturernas uppmätta ljusfördelning (tillverkarnas fotometrifiler), dagsljuset och reflexerna i rummen. Delområdena Bänken längs 3NV, Bänken längs 3SV och Ön mäts på en vågrät yta 0,91 m över golvet.
2. Tända: AL-T1 Allrum, tubspotar sydost; AL-T2 Allrum, tubspotar nordväst; AL-T3 Allrum, PH 5 över bordet; KO-T1 Kök, tubspotar mot taket; KO-T2 Kök, spotar mot bänken; KO-T3 Kök, Stav över ön; GA-T1 Gång, tubspotar; HA-T1 Hall, tubspotar; VR-T1 Vardagsrum, spotar sydost; VR-T2 Vardagsrum, spotar nordväst; VR-T3 Vardagsrum, VL45; BA-T1 Badrum, spotar; BA-T2 Badrum, lampan över tvättstället; SV-T1 Sovrum, glob; KT-T1 Kontor, spotar mot väggarna; SL-T1 Sovrum litet, spotar mot gaveln; SL-T2 Sovrum litet, spotar mot L1; KL-T1 Kontor litet, glob; GR-T1 Gästrum, glob; KA-T6 Källaren, det stora rummet; KA-T7 Källaren, det lilla rummet väster om KL2; KA-T8 Källaren, det lilla rummet öster om KL2; KA-T1 Källaren, trapphallen; KA-T2 Källaren, tvättstugan; KA-T3 Källaren, rummen söder om V4–V6, västra delen; KA-T4 Källaren, rummen söder om V4–V6, östra delen; KA-T5 Källaren, rummet norr om trapphallen.
3. Inget dagsljus (2026-12-21 kl. 22:00).
4. Statistiken per rum utan en kantzon på 0,5 m längs väggarna (SS-EN 12464-1), i små rum mindre, och utan inredningen på mätytan (skåp, säng, bänkskivor, källartrappan och pelarna, vita på planen); jämnheten $U_0$ = minsta / medel. Rummen är de slutna ytorna mellan väggarna; en öppen planlösning delas mellan rummens namn.
5. Ritningen ritas med ./mod ljusplan (verktyg/modellering); mätytorna står i modellens el/matytor.py.

### Teckenförklaring

- isolinje, med belysningsstyrkan
- rummets yta i statistiken (utan kantzonen)
- delområde med egen statistik
- armatur

| Rev | Avser | Datum | Sign |
|---|---|---|---|

PROJEKT

**Fritidshus Trebodar, Resö, Tanum**

FASTIGHET

Resö 2:66, Tanums kommun · BYGG.2025.2278

INNEHÅLL

**Ljusplan**
**Plan 1, golvet**

| SKALA | FORMAT | DATUM |
|---|---|---|
| 1:75 | A3 | 2026-11-05 |
| UPPRÄTTAD | GRANSKAD | UNDERLAG |
| Viktor Ogeman | – | Modellen, rendering |
| STATUS | | REVISION |
| **UTREDNING** | | **A** |

RITNINGSNUMMER

# U-04.1

## Plan 1, bordshöjd 0,75 m, belysningsstyrka

Skala 1:75




### Belysningsstyrka, lux

| |
|---|
| 5 000 |
| 2 000 |
| 1 000 |
| 750 |
| 500 |
| 300 |
| 200 |
| 150 |
| 100 |
| 75 |
| 50 |
| 20 |
| 10 |
| 0 |

### Rum och delområden, lux

| Rum | Medel | Min | Max | Jämnhet $U_0$ |
|---|---|---|---|---|
| Allrum | 280 | 118 | 766 | 0,42 |
| Badrum | 342 | 103 | 520 | 0,30 |
| Bänken längs 3NV (0,91 m) | 651 | 192 | 899 | 0,30 |
| Bänken längs 3SV (0,91 m) | 240 | 93 | 535 | 0,39 |
| Gästrum | 68 | 54 | 78 | 0,79 |
| Gång | 151 | 66 | 255 | 0,44 |
| Hall | 102 | 80 | 146 | 0,79 |
| Kontor | 241 | 78 | 444 | 0,32 |
| Kontor, litet | 70 | 52 | 82 | 0,75 |
| Kök | 315 | 44 | 719 | 0,14 |
| Sovrum | 37 | 16 | 58 | 0,42 |
| Sovrum, litet | 242 | 162 | 275 | 0,67 |
| Trappa | 155 | 93 | 193 | 0,60 |
| Vardagsrum | 267 | 100 | 483 | 0,37 |
| Ön (0,91 m) | 811 | 182 | 2 020 | 0,22 |

### Anvisningar

1. Belysningsstyrkan på en vågrät yta 0,75 m över golvet, i rutor om 50 mm, ur renderingen i Blender (Cycles): armaturernas uppmätta ljusfördelning (tillverkarnas fotometrifiler), dagsljuset och reflexerna i rummen. Delområdena Bänken längs 3NV, Bänken längs 3SV och Ön mäts på en vågrät yta 0,91 m över golvet.
2. Tända: AL-T1 Allrum, tubspotar sydost; AL-T2 Allrum, tubspotar nordväst; AL-T3 Allrum, PH 5 över bordet; KO-T1 Kök, tubspotar mot taket; KO-T2 Kök, spotar mot bänken; KO-T3 Kök, Stav över ön; GA-T1 Gång, tubspotar; HA-T1 Hall, tubspotar; VR-T1 Vardagsrum, spotar sydost; VR-T2 Vardagsrum, spotar nordväst; VR-T3 Vardagsrum, VL45; BA-T1 Badrum, spotar; BA-T2 Badrum, lampan över tvättstället; SV-T1 Sovrum, glob; KT-T1 Kontor, spotar mot väggarna; SL-T1 Sovrum litet, spotar mot gaveln; SL-T2 Sovrum litet, spotar mot L1; KL-T1 Kontor litet, glob; GR-T1 Gästrum, glob; KA-T6 Källaren, det stora rummet; KA-T7 Källaren, det lilla rummet väster om KL2; KA-T8 Källaren, det lilla rummet öster om KL2; KA-T1 Källaren, trapphallen; KA-T2 Källaren, tvättstugan; KA-T3 Källaren, rummen söder om V4–V6, västra delen; KA-T4 Källaren, rummen söder om V4–V6, östra delen; KA-T5 Källaren, rummet norr om trapphallen.
3. Inget dagsljus (2026-12-21 kl. 22:00).
4. Statistiken per rum utan en kantzon på 0,5 m längs väggarna (SS-EN 12464-1), i små rum mindre, och utan inredningen på mätytan (skåp, säng, bänkskivor, källartrappan och pelarna, vita på planen); jämnheten $U_0$ = minsta / medel. Rummen är de slutna ytorna mellan väggarna; en öppen planlösning delas mellan rummens namn.
5. Ritningen ritas med ./mod ljusplan (verktyg/modellering); mätytorna står i modellens el/matytor.py.

### Teckenförklaring

- isolinje, med belysningsstyrkan
- rummets yta i statistiken (utan kantzonen)
- delområde med egen statistik
- armatur

| Rev | Avser | Datum | Sign |
|---|---|---|---|

PROJEKT

**Fritidshus Trebodar, Resö, Tanum**

FASTIGHET

Resö 2:66, Tanums kommun · BYGG.2025.2278

INNEHÅLL

**Ljusplan**
**Plan 1, bordshöjd 0,75 m**


| SKALA | FORMAT | DATUM |
|---|---|---|
| 1:75 | A3 | 2026-11-05 |
| UPPRÄTTAD | GRANSKAD | UNDERLAG |
| Viktor Ogeman | – | Modellen, rendering |
| STATUS | | REVISION |
| **UTREDNING** | | **A** |

RITNINGSNUMMER


# U-04.2

## Köket, bänkskivorna 0,91 m, belysningsstyrka

Skala 1:50

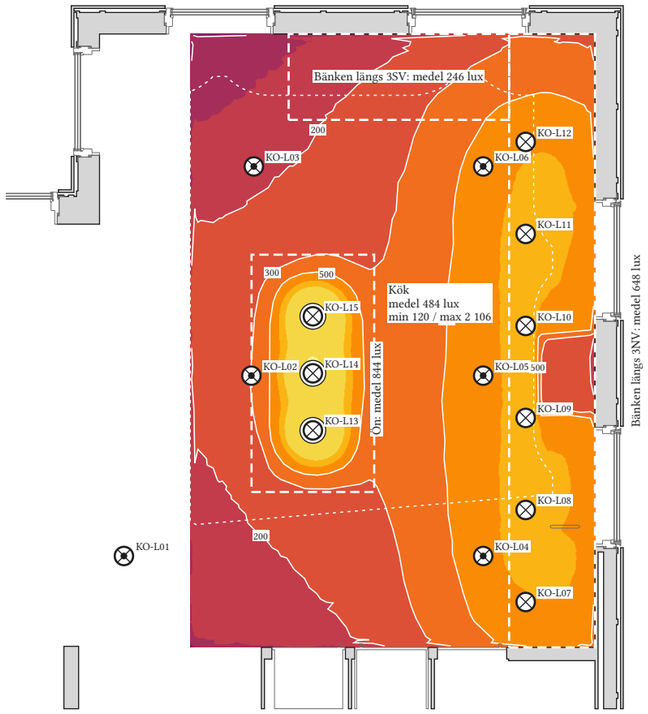


### Belysningsstyrka, lux

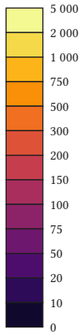


### Rum och delområden, lux

| Rum | Medel | Min | Max | Jämnhet $U_0$ |
|---|---|---|---|---|
| Bänken längs 3NV | 648 | 140 | 868 | 0,22 |
| Bänken längs 3SV | 246 | 125 | 566 | 0,51 |
| Kök | 484 | 120 | 2 106 | 0,25 |
| Ön | 844 | 216 | 2 106 | 0,26 |

### Anvisningar

1. Belysningsstyrkan på en vågrät yta 0,91 m över golvet, i rutor om 25 mm, ur renderingen i Blender (Cycles): armaturernas uppmätta ljusfördelning (tillverkarnas fotometrifiler), dagsljuset och reflexerna i rummen.
2. Tända: AL-T1 Allrum, tubspotar sydost; AL-T2 Allrum, tubspotar nordväst; AL-T3 Allrum, PH 5 över bordet; KO-T1 Kök, tubspotar mot taket; KO-T2 Kök, spotar mot bänken; KO-T3 Kök, Stav över ön; GA-T1 Gång, tubspotar; HA-T1 Hall, tubspotar; VR-T1 Vardagsrum, spotar sydost; VR-T2 Vardagsrum, spotar nordväst; VR-T3 Vardagsrum, VL45; BA-T1 Badrum, spotar; BA-T2 Badrum, lampan över tvättstället; SV-T1 Sovrum, glob; KT-T1 Kontor, spotar mot väggarna; SL-T1 Sovrum litet, spotar mot gaveln; SL-T2 Sovrum litet, spotar mot L1; KL-T1 Kontor litet, glob; GR-T1 Gästrum, glob; KA-T6 Källaren, det stora rummet; KA-T7 Källaren, det lilla rummet väster om KL2; KA-T8 Källaren, det lilla rummet öster om KL2; KA-T1 Källaren, trapphallen; KA-T2 Källaren, tvättstugan; KA-T3 Källaren, rummen söder om V4–V6, västra delen; KA-T4 Källaren, rummen söder om V4–V6, östra delen; KA-T5 Källaren, rummet norr om trapphallen.
3. Inget dagsljus (2026-12-21 kl. 22:00).
4. Statistiken per rum utan en kantzon på 0,5 m längs väggarna (SS-EN 12464-1), i små rum mindre, och utan inredningen på mätytan (skåp, säng, bänkskivor, källartrappan och pelarna, vita på planen); jämnheten $U_0$ = minsta / medel. Rummen är de slutna ytorna mellan väggarna; en öppen planlösning delas mellan rummens namn.
5. Ritningen ritas med ./mod ljusplan (verktyg/modellering); mätytorna står i modellens el/matytor.py.

### Teckenförklaring

- isolinje, med belysningsstyrkan
- rummets yta i statistiken (utan kantzonen)
- delområde med egen statistik
- armatur

| Rev | Avser | Datum | Sign |
|---|---|---|---|

PROJEKT

**Fritidshus Trebodar, Resö, Tanum**

FASTIGHET

Resö 2:66, Tanums kommun · BYGG.2025.2278

INNEHÅLL

**Ljusplan**
**Köket, bänkskivorna 0,91 m**


| SKALA | FORMAT | DATUM |
|---|---|---|
| 1:50 | A3 | 2026-11-05 |
| UPPRÄTTAD | GRANSKAD | UNDERLAG |
| Viktor Ogeman | – | Modellen, rendering |
| STATUS | | REVISION |
| **UTREDNING** | | **A** |

RITNINGSNUMMER

**U-04.3**

## Källaren, golvet, belysningsstyrka

Skala 1:75

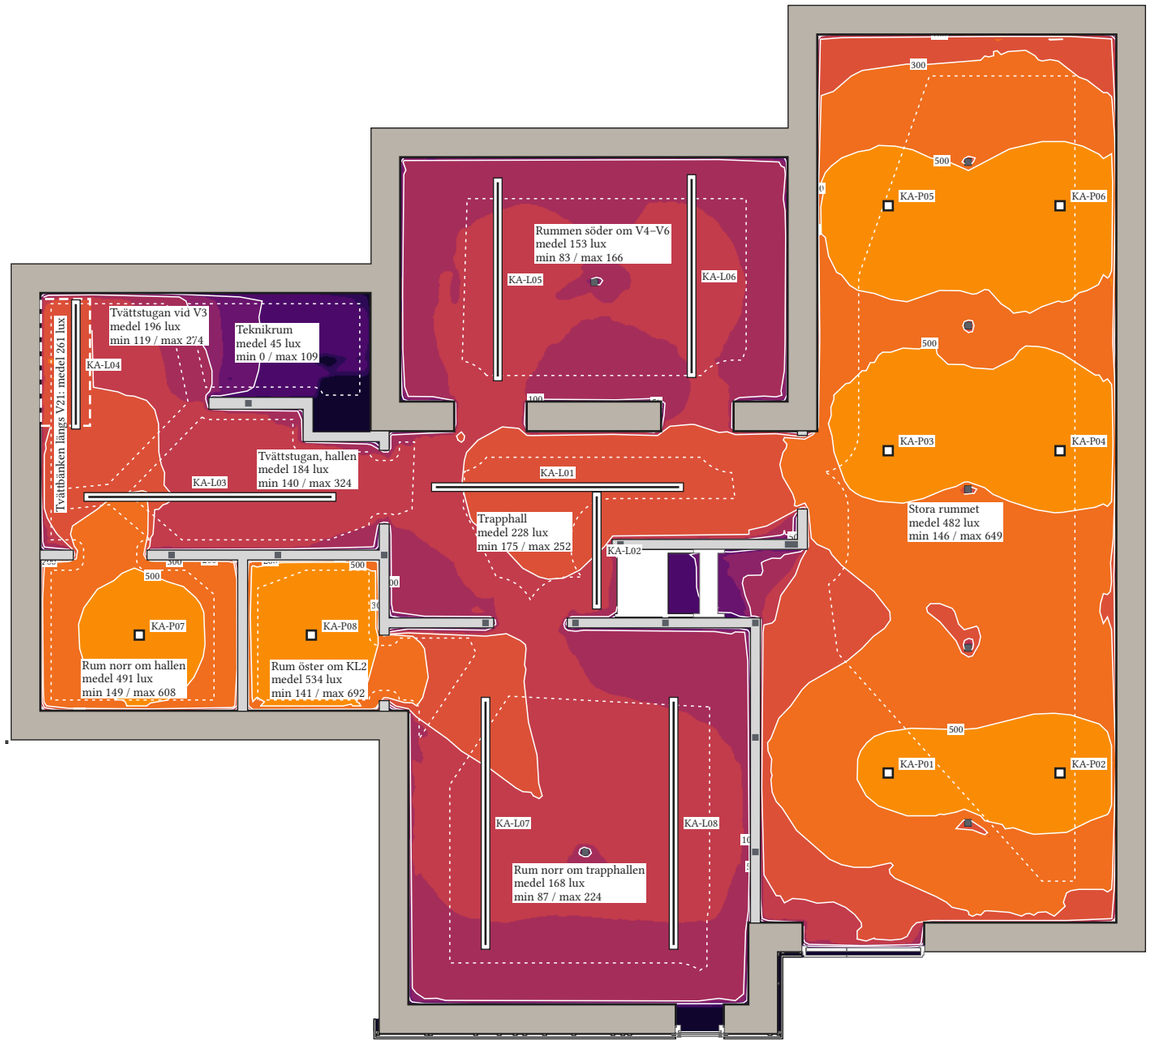


### Belysningsstyrka, lux

5 000
2 000
1 000
750
500
300
200
150
100
75
50
20
10
0

### Rum och delområden, lux

| Rum | Medel | Min | Max | Jämnhet $U_o$ |
|---|---|---|---|---|
| Rum norr om hallen | 491 | 149 | 608 | 0,30 |
| Rum norr om trapphallen | 168 | 87 | 224 | 0,52 |
| Rum öster om KL2 | 534 | 141 | 692 | 0,26 |
| Rummen söder om V4–V6 | 153 | 83 | 166 | 0,54 |
| Stora rummet | 482 | 146 | 649 | 0,30 |
| Teknikrum | 45 | 0 | 109 | 0,00 |
| Trapphall | 228 | 175 | 252 | 0,77 |
| Tvättbänken längs V21 (0,90 m) | 261 | 162 | 307 | 0,62 |
| Tvättstugan vid V3 | 196 | 119 | 274 | 0,61 |
| Tvättstugan, hallen | 184 | 140 | 324 | 0,76 |

### Anvisningar

1. Belysningsstyrkan på golvet, i rutor om 50 mm, ur renderingen i Blender (Cycles): armaturernas uppmätta ljusfördelning (tillverkarnas fotometrifiler), dagsljuset och reflexerna i rummen. Ljuslinjerna lyser som lambertska ytor (den opala diffusorn) med det antagna ljusflödet per meter lysande längd. Delområdet Tvättbänken längs V21 mäts på en vågrät yta 0,90 m över golvet.
2. Tända: AL-T1 Allrum, tubspotar sydost; AL-T2 Allrum, tubspotar nordväst; AL-T3 Allrum, PH 5 över bordet; KO-T1 Kök, tubspotar mot taket; KO-T2 Kök, spotar mot bänken; KO-T3 Kök, Stav över ön; GA-T1 Gång, tubspotar; HA-T1 Hall, tubspotar; VR-T1 Vardagsrum, spotar sydost; VR-T2 Vardagsrum, spotar nordväst; VR-T3 Vardagsrum, VL45; BA-T1 Badrum, spotar; BA-T2 Badrum, lampan över tvättstället; SV-T1 Sovrum, glob; KT-T1 Kontor, spotar mot väggarna; SL-T1 Sovrum litet, spotar mot gaveln; SL-T2 Sovrum litet, spotar mot L1; KL-T1 Kontor litet, glob; GR-T1 Gästrum, glob; KA-T6 Källaren, det stora rummet; KA-T7 Källaren, det lilla rummet väster om KL2; KA-T8 Källaren, det lilla rummet öster om KL2; KA-T1 Källaren, trapphallen; KA-T2 Källaren, tvättstugan; KA-T3 Källaren, rummen söder om V4–V6, västra delen; KA-T4 Källaren, rummen söder om V4–V6, östra delen; KA-T5 Källaren, rummet norr om trapphallen.
3. Inget dagsljus (2026-12-21 kl. 22:00).
4. Statistiken per rum utan en kantzon på 0,5 m längs väggarna (SS-EN 12464-1), i små rum mindre, och utan inredningen på mätytan (skåp, säng, bänkskivor, källartrappan och pelarna, vita på planen); jämnheten $U_o$ = minsta / medel. Rummen är de slutna ytorna mellan väggarna; en öppen planlösning delas mellan rummens namn.
5. Ritningen ritas med ./mod ljusplan (verktyg/modellering); mätytorna står i modellens el/matytor.py.

### Teckenförklaring

- isolinje, med belysningsstyrkan
- rummets yta i statistiken (utan kantzonen)
- delområde med egen statistik
- armatur
- ljuslinje, i sin längd

| Rev | Avser | Datum | Sign |
|---|---|---|---|

PROJEKT

**Fritidshus Trebodar, Resö, Tanum**

FASTIGHET

Resö 2:66, Tanums kommun · BYGG.2025.2278

INNEHÅLL

**Ljusplan**
**Källaren, golvet**

| SKALA | FORMAT | DATUM |
|---|---|---|
| 1:75 | A3 | 2026-11-05 |

| UPPRÄTTAD | GRANSKAD | UNDERLAG |
|---|---|---|
| Viktor Ogeman | – | Modellen, rendering |

| STATUS | REVISION |
|---|---|
| **UTREDNING** | **A** |

RITNINGSNUMMER

# U-04.4