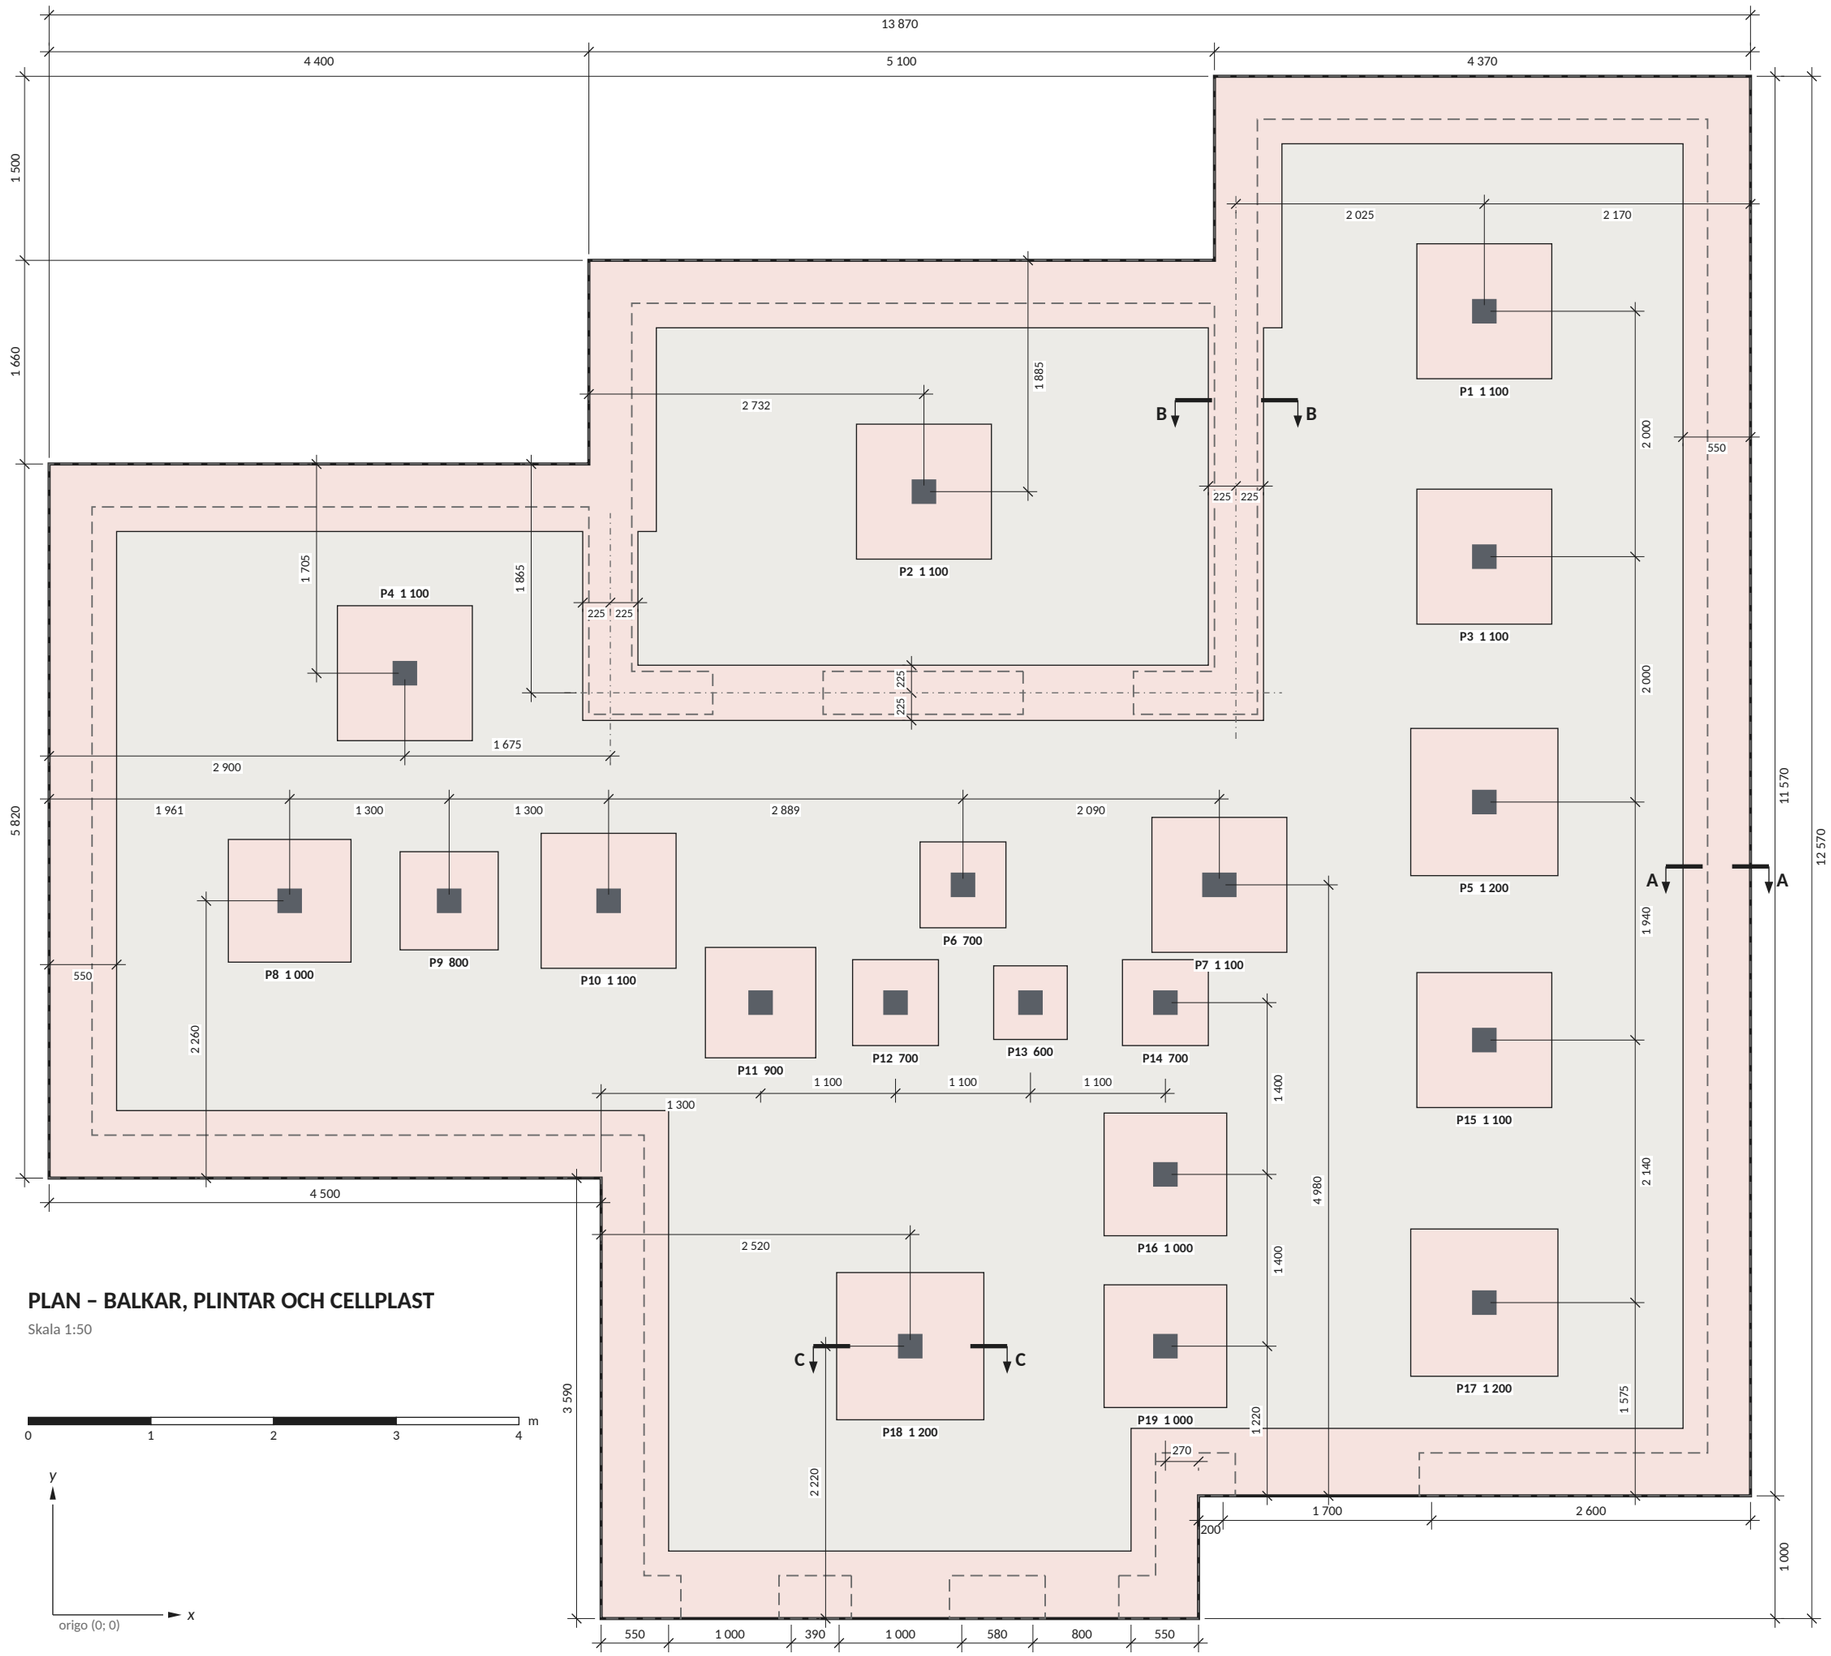


PLAN – BALKAR, PLINTAR OCH CELLPLAST

Skala 1:50

Anvisningar

1. Bottenplatta L300: 100 mm betong C30/37 på 200 mm cellplast S100 i två skikt med åldringsbeständig plastfolie emellan. Kantbalkar 450 × 200 längs hela kanten i L-element S300, höjd 300, 600 × 1200 (t.ex. Finja), med foten av S300; balkar under innerväggarna 450 × 200 och plintar under rören, lika höga, på 100 mm S300. Bara två kvaliteter: S100 under plattan och S300 under balkar och plintar. Samma uppbyggnad i hela källaren.
2. Bottenplattans ytterkant är L-elementens ytterkant, i väggarnas ytterliv (R-05.1). Planens mått går dit. Planen visar kantbalken ut till ytterkanten; betongen börjar innanför L-elementets rygg, 100 mm (sektion A). Väggens yttre cellplast står på ryggen, kärnan på kantbalken.
3. Plintarna är kvadratiska och centrerade under rörets mitt. Mått till plintarnas och innerbalkarnas mitt från bottenplattans ytterkant.
4. Dränledningen läggs runt huset innan cellplasten läggs (K-06).
5. Armering R-04.2, sektioner och förteckningar R-04.3. Fotplåtar och rör R-05.5.

Teckenförklaring

- kantbalk i L-element S300, balk och plint, 200 hög, på 100 S300
- platta 100 på 200 S100
- innerbalkarnas mitt
- väggarna (R-05)
- fotplåt (R-05.5)

Plintar (sida och mitt)

Plint	Sida	x	y	Anm
P1	1 100	11 670	10 625	
P2	1 100	7 102	9 155	
P3	1 100	11 670	8 625	
P4	1 100	2 870	7 675	
P5	1 200	11 670	6 625	
P6	700	7 420	5 950	
P7	1 100	9 510	5 950	två rör, fotplåt 280 × 200 eller 2 st 140 × 200 (R-05.5)
P8	1 000	1 931	5 820	
P9	800	3 231	5 820	
P10	1 100	4 531	5 820	
P11	900	5 770	4 990	
P12	700	6 870	4 990	
P13	600	7 970	4 990	
P14	700	9 070	4 990	
P15	1 100	11 670	4 685	
P16	1 000	9 070	3 590	
P17	1 200	11 670	2 545	
P18	1 200	6 990	2 190	
P19	1 000	9 070	2 190	

Ritningsförteckning R-04

Ritning	Innehåll	Skala
R-04.1	Plan, balkar, plintar och cellplast	1:50
R-04.2	Armering	1:50
R-04.3	Sektioner, detaljer och förteckningar	1:10, 1:20, 1:50

Rev	Avser	Datum	Sign
A	Första utgåvan	2026-10-16	VO

PROJEKT

Fritidshus Trebodar, Resö, Tanum

FASTIGHET

Resö 2:66, Tanums kommun · BYGG.2025.2278


INNEHÅLL

Bottenplatta
Plan, balkar, plintar och cellplast

SKALA	FORMAT	DATUM
1:50	A3	2026-10-16
UPPRÄTTAD	GRANSKAD	UNDERLAG
Viktor Ogeman	–	K-06 rev A, K-05 rev A
STATUS		REVISION
KONSTRUKTION		**A**

RITNINGSNUMMER

R-04.1

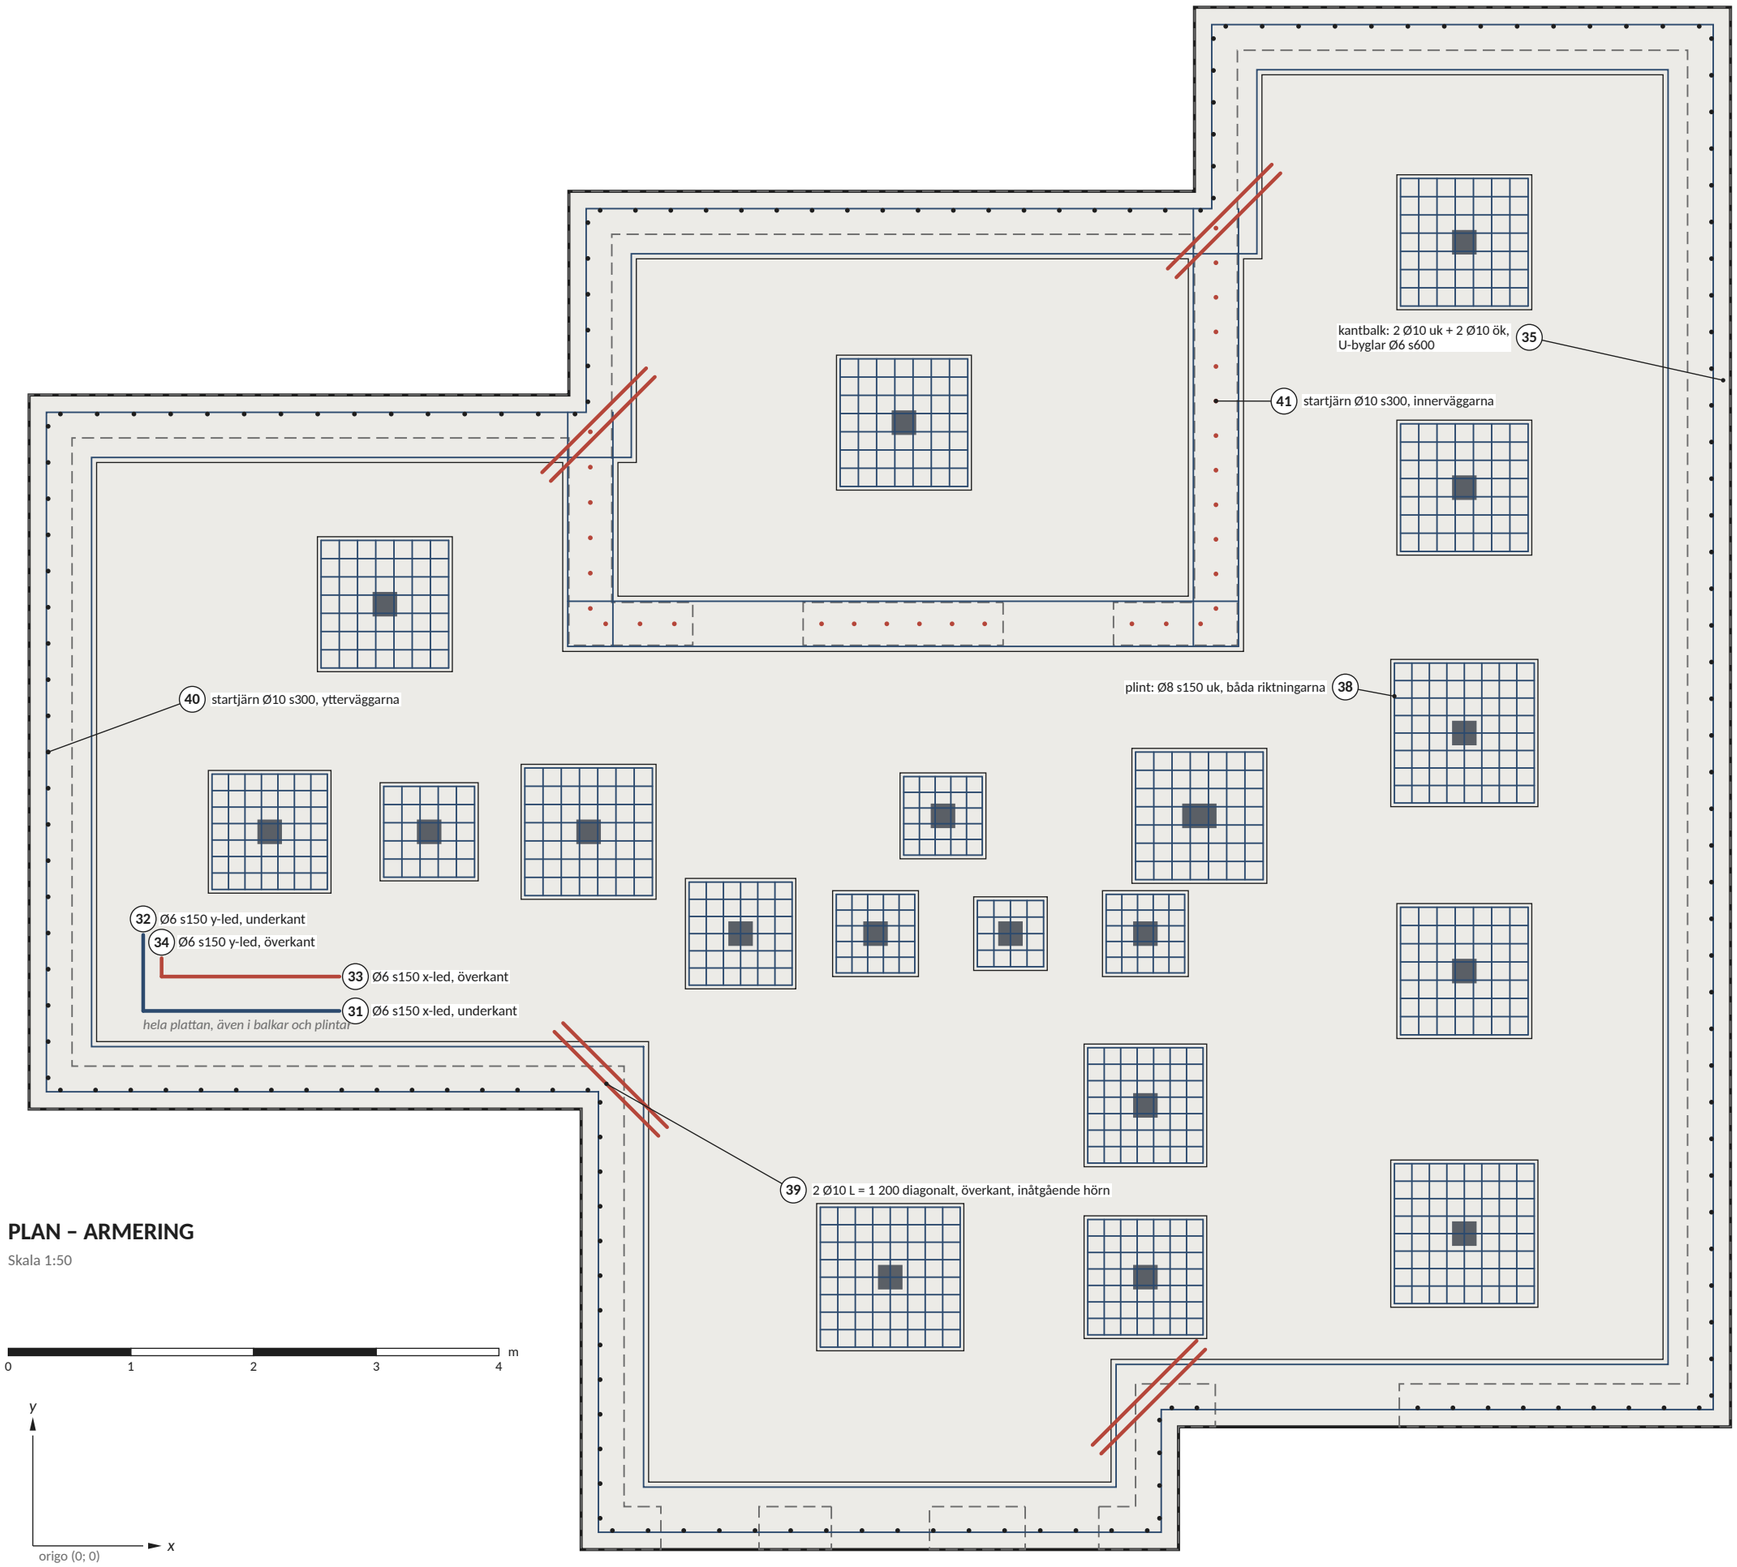

PLAN – ARMERING

Skala 1:50

Anvisningar

1. Armering B500B. Täckande skikt: 30 mm mot cellplasten (distanser) och 25 mm i överkant.
2. Nät Ø6 s150 i under- och överkant i hela plattan, också genom balkarna och plintarna. Golvvärmeslangarna fästs i underkantsnätet. Skarvlängd Ø6 400.
3. Kantbalkar och balkar under innerväggarna: 2 Ø10 i underkant på byglarna och 2 Ø10 i överkant under överkantsnätet, U-byglar Ø6 s600. Skarvlängd Ø10 650; i hörnen bockas järnen eller skarvas med vinkeljärn. Innerbalkarnas järn förs in i kantbalken och i den korsande balken.
4. Plintar: Ø8 s150 i underkant, båda riktningarna. Fotplåten gjuts in kant i kant med plintens överkant (R-05.5); näten läggs fritt från svetsbultarna.
5. Inåtgående hörn: 2 Ø10, L = 1 200, i överkant diagonalt, 150 och 250 mm från hörnet.
6. Startjärn Ø10 s300, 1 200 upp och 500 i balken: den lodräta delen och foten, 330, på byglarna.

Teckenförklaring

- armering i underkant / balkjärn
- armering i överkant (diagonaljärn)
- startjärn, ytterväggarna
- startjärn, innerväggarna
- (31) positionsnummer (stålförteckning R-04.3)

Rev	Avser	Datum	Sign
A	Första utgåvan	2026-10-16	VO

PROJEKT

Fritidshus Trebodar, Resö, Tanum

FASTIGHET

Resö 2:66, Tanums kommun · BYGG.2025.2278

INNEHÅLL

Bottenplatta
Armering


SKALA	FORMAT	DATUM
1:50	A3	2026-10-16

UPPRÄTTAD	GRANSKAD	UNDERLAG
Viktor Ogeman	–	K-06 rev A, K-05 rev A

STATUS	REVISION
KONSTRUKTION	**A**


RITNINGSNUMMER

R-04.2

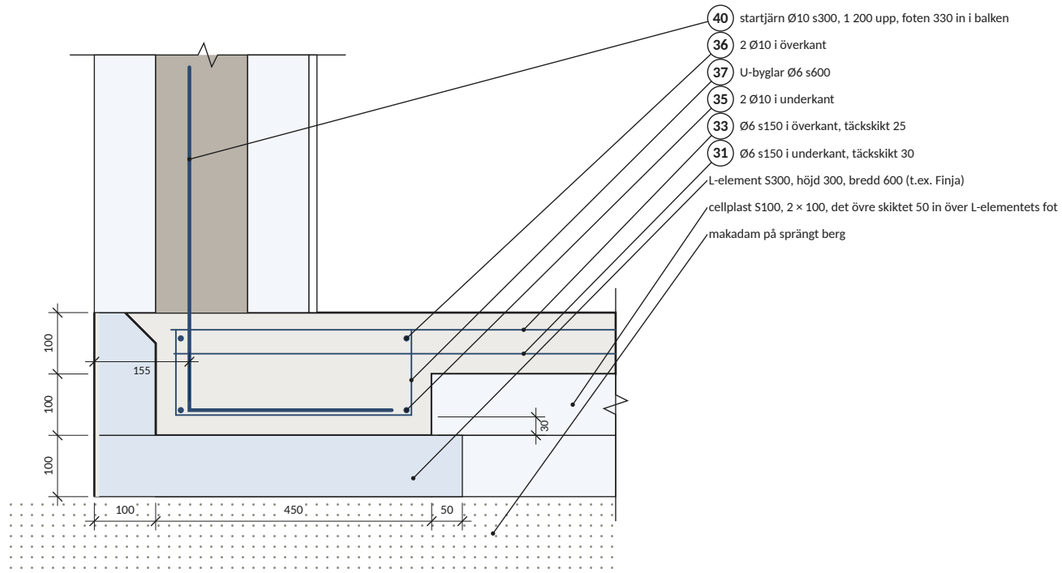


SEKTION A–A Kantbalk i L-element (V14)

Skala 1:10

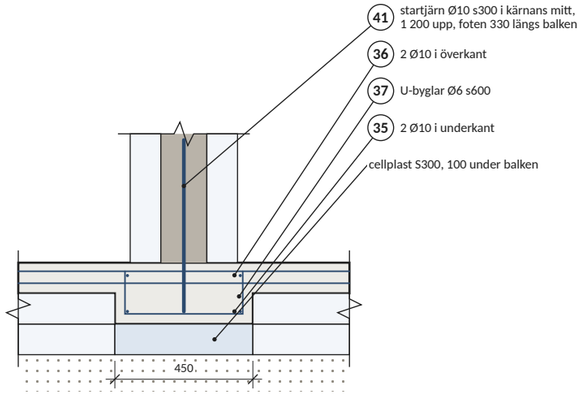


SEKTION B–B Balk under innervägg (V15)

Skala 1:20

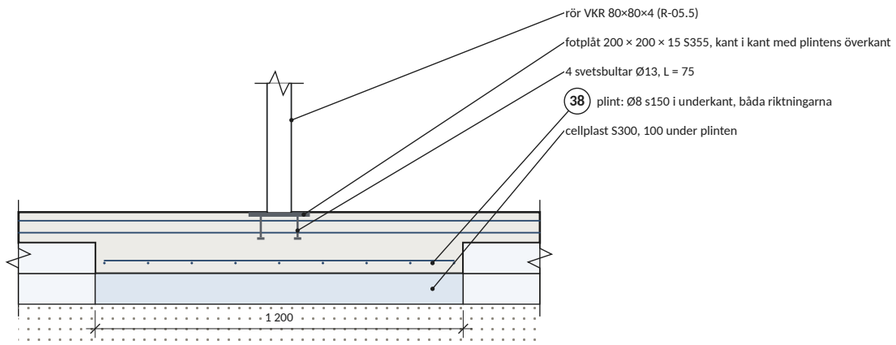

SEKTION C–C Plint under rör (P18, 1 200)

Skala 1:20

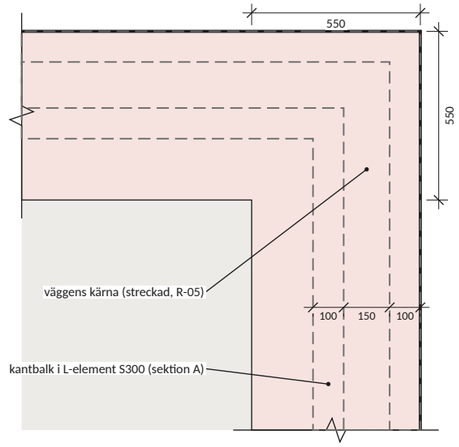

DETALJ D Yttre hörn i plan (V1/V14)

Skala 1:20

Samma vid alla hörn: kantbalken ut till väggens ytterliv.

Stålförteckning, B500B

Pos	Ø	Form	s	Anm
31	Ø6	rak	s150	UK x-led, hela plattan
32	Ø6	rak	s150	UK y-led, hela plattan
33	Ø6	rak	s150	ÖK x-led, hela plattan
34	Ø6	rak	s150	ÖK y-led, hela plattan
35	Ø10	rak	–	balkar, 2 i underkant
36	Ø10	rak	–	balkar, 2 i överkant
37	Ø6	U 145+390+145	s600	byglar i balkarna
38	Ø8	rak	s150	plintar, underkant
39	Ø10	rak 1 200	–	inåtgående hörn, 2 per hörn, ÖK
40	Ø10	L 1 360+330	s300	ytterväggarna, utsidan
41	Ø10	L 1 360+330	s300	innerväggarna, mitt

Anvisningar

1. Lägg L-elementen (fot S300) med ytterkanten i väggarnas ytterliv, S300 under innerbalkarna och plintarna och S100 under plattan i två skikt med plastfolie emellan; det övre skiktet går 50 mm in över L-elementens fot och fästs med plastspik.
2. Armera och fixera fotplåtarna i läge och höjd. Gjut bottenplattan med balkar och plintar i en gjutning; fotplåtarna gjuts in kant i kant med plintarnas överkant. Rugga ytan under väggarna.
3. Kontrollera före gjutning: armeringens läge och täckskikt (distanser), plintarnas läge och storlek, fotplåtarnas läge och höjd (±5 mm), startjärnen.
4. Plattan behöver inga fogar; golvbeläggning och tätskikt ska tåla krympsprickor (K-06).
5. Plan R-04.1, armering R-04.2.

Teckenförklaring

- betong C30/37
- cellplast S100
- L-element (fot S300), S300 under balkar och plintar
- väggens betongkärna (R-05)
- armering

Cellplast

	Utförande	Anm
S100	100 mm, övre skiktet	under plattan, 50 in över L-elementens fot
S100	100 mm, undre skiktet	plastfolie mellan skikten
S300	100 mm	under innerbalkarna och plintarna
L-element	S300, höjd 300, 600 × 1200 (t.ex. Finja)	längs hela kanten, ytterkant i väggarnas ytterliv

Rev	Avser	Datum	Sign
A	Första utgåvan	2026-10-16	VO

PROJEKT

Fritidshus Trebodar, Resö, Tanum

FASTIGHET

Resö 2:66, Tanums kommun · BYGG.2025.2278

INNEHÅLL

Bottenplatta
Sektioner, detaljer och förteckningar

SKALA	FORMAT	DATUM
1:10, 1:20, 1:50	A3	2026-10-16
UPPRÄTTAD: Viktor Ogeman	GRANSKAD: –	UNDERLAG: K-06 rev A, K-05 rev A
STATUS: **KONSTRUKTION**		REVISION: **A**

RITNINGSNUMMER

R-04.3