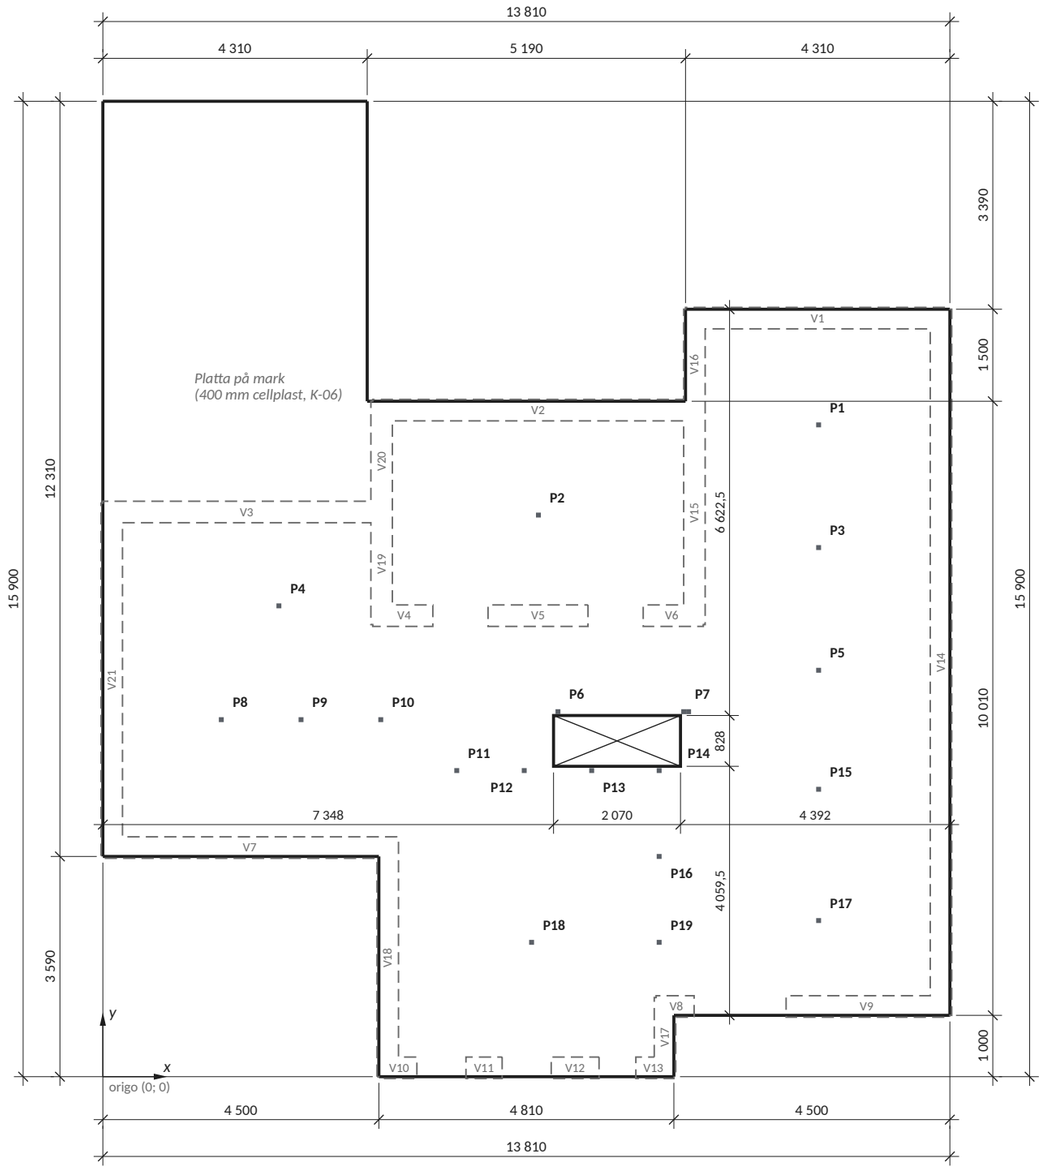


PLAN – ÖVERSIKT OCH YTTERMÅTT

Skala 1:100

0 1 2 3 4 5 m

Anvisningar

1. Betong C30/37, samma som källarväggarna (R-05), exponeringsklass XC1, livslängd 50 år. Armering B500B.
2. Täckskikt: underkant 20 mm, överkant 25 mm, kanter och hålkanter 25 mm, även mot de fria kanterna vid öppningarna i källarens ytterväggar.
3. Skarvlängd: Ø8 500, Ø10 650, Ø12 750 mm. Skarvar förskjuts minst 1,3 × skarvlängden.
4. Järnen i varje nät läggs i valfri ordning. Tilläggsjärn läggs i nätets lager.
5. Plattans kontur och trapphålets läge enligt denna ritning. Rörens lägen, se tabell på R-06.2.
6. Källarväggarna (Kub 350-150, R-05) under plattan streckade.

Teckenförklaring

- plattans kant
- källarvägg under plattan
- stålrör VKR 80×80×4 (K-05)

Ritningsförteckning R-06

Ritning	Innehåll	Skala
R-06.1	Översikt och yttermått	1:100
R-06.2	Armering i underkant	1:50
R-06.3	Armering i överkant	1:50
R-06.4	Sektioner, detaljer och stålförteckning	1:5, 1:10, 1:20

Rev	Avser	Datum	Sign
A	Första utgåvan	2026-10-08	VO

PROJEKT

Fritidshus Trebodar, Resö, Tanum

FASTIGHET

Resö 2:66, Tanums kommun · BYGG.2025.2278


INNEHÅLL

Mellanbjälklag
Översikt och yttermått

SKALA	FORMAT	DATUM
1:100	A3	2026-10-08
UPPRÄTTAD	GRANSKAD	UNDERLAG
Viktor Ogeman	–	K-05 rev A, K-06 rev A
STATUS		REVISION
KONSTRUKTION		**A**

RITNINGSNUMMER

R-06.1

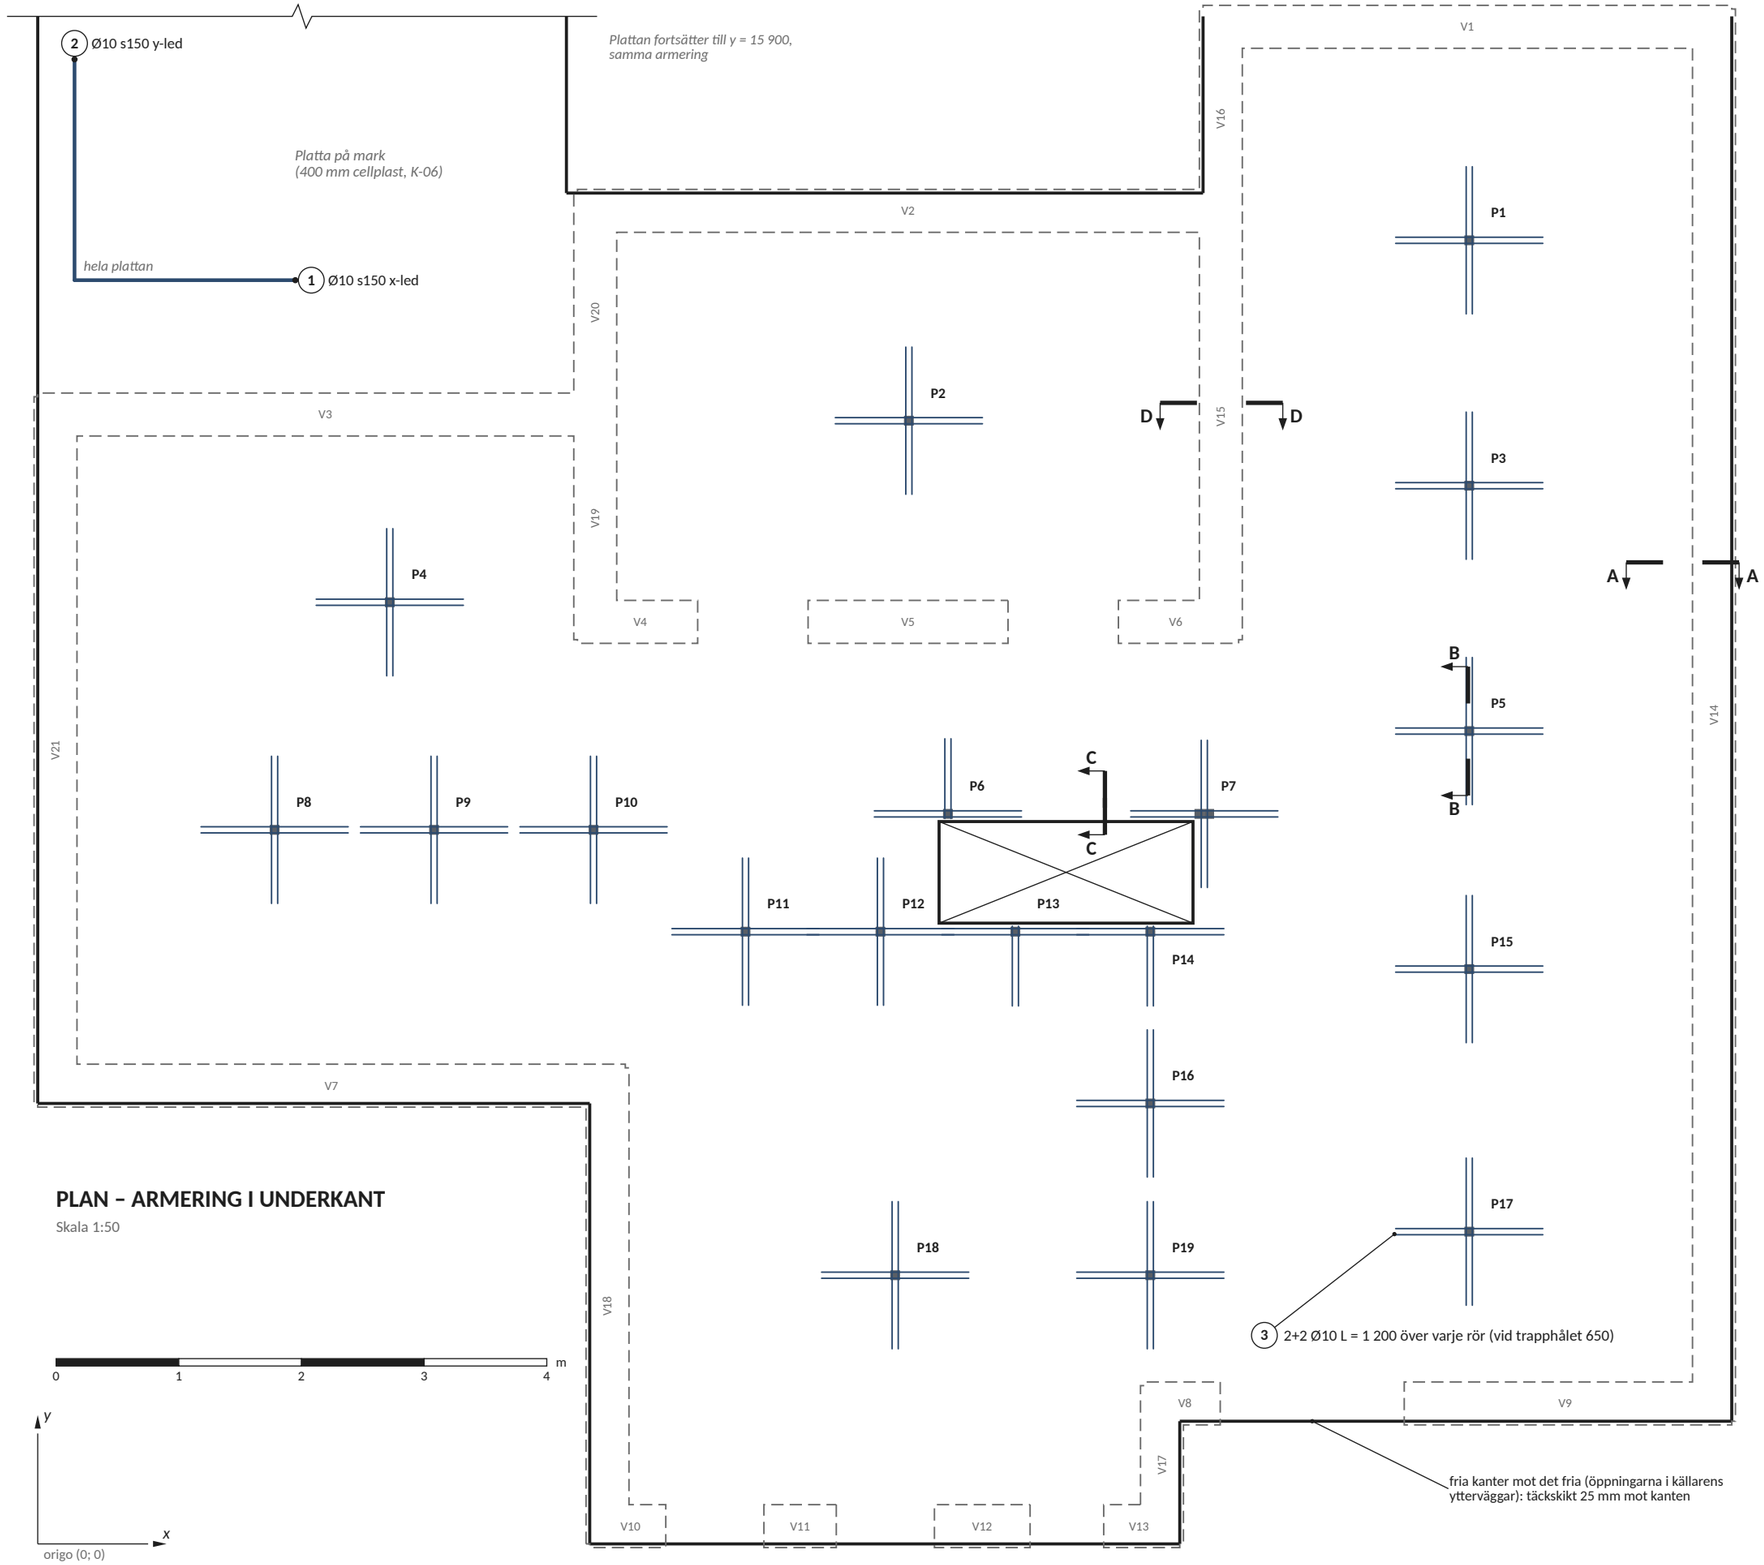

PLAN – ARMERING I UNDERKANT

Skala 1:50

Anvisningar

1. Allmänt och mått, se R-06.1.
2. Underkantsnätet läggs på distanser 20 mm, högst 0,8 m isär.
3. Minst två underkantsjärn i vardera riktningen ska passera över varje rör (SS-EN 1992-1-1 9.4.1(3)): pos 3, bundna till nätet. Vid trapphålet (P6, P13, P14) slutar järnen mot hålet 25 mm från hålkanten, L = 650.
4. Överkant, se R-06.3. Sektioner A–D, se R-06.4.

Teckenförklaring

- armering i underkant
- ① positionsnummer (stålförteckning R-06.4)
- källarvägg under plattan
- stålrör VKR 80×80×4 (K-05)

Rör och topplåtar

Rör	x	y	Topplåt
P1	11 670	10 625	80×80×8
P2	7 102	9 155	80×80×8
P3	11 670	8 625	80×80×8
P4	2 870	7 675	80×80×8
P5	11 670	6 625	80×80×8
P6	7 420	5 950	80×80×8
P7	9 470 och 9 550	5 950	två rör tätt intill varandra, 80×80×8 på vart
P8	1 931	5 820	80×80×8
P9	3 231	5 820	80×80×8
P10	4 531	5 820	80×80×8
P11	5 770	4 990	80×80×8
P12	6 870	4 990	80×80×8
P13	7 970	4 990	80×80×8
P14	9 070	4 990	80×80×8
P15	11 670	4 685	80×80×8
P16	9 070	3 590	80×80×8
P17	11 670	2 545	80×80×8
P18	6 990	2 190	80×80×8
P19	9 070	2 190	80×80×8

Rev	Avser	Datum	Sign
A	Första utgåvan	2026-10-08	VO

PROJEKT

Fritidshus Trebodar, Resö, Tanum

FASTIGHET

Resö 2:66, Tanums kommun · BYGG.2025.2278


INNEHÅLL

Mellanbjälklag
Armering i underkant

SKALA	FORMAT	DATUM
1:50	A3	2026-10-08
UPPRÄTTAD	GRANSKAD	UNDERLAG
Viktor Ogeman	–	K-05 rev A, K-06 rev A
STATUS		REVISION
KONSTRUKTION		**A**

RITNINGSNUMMER

R-06.2

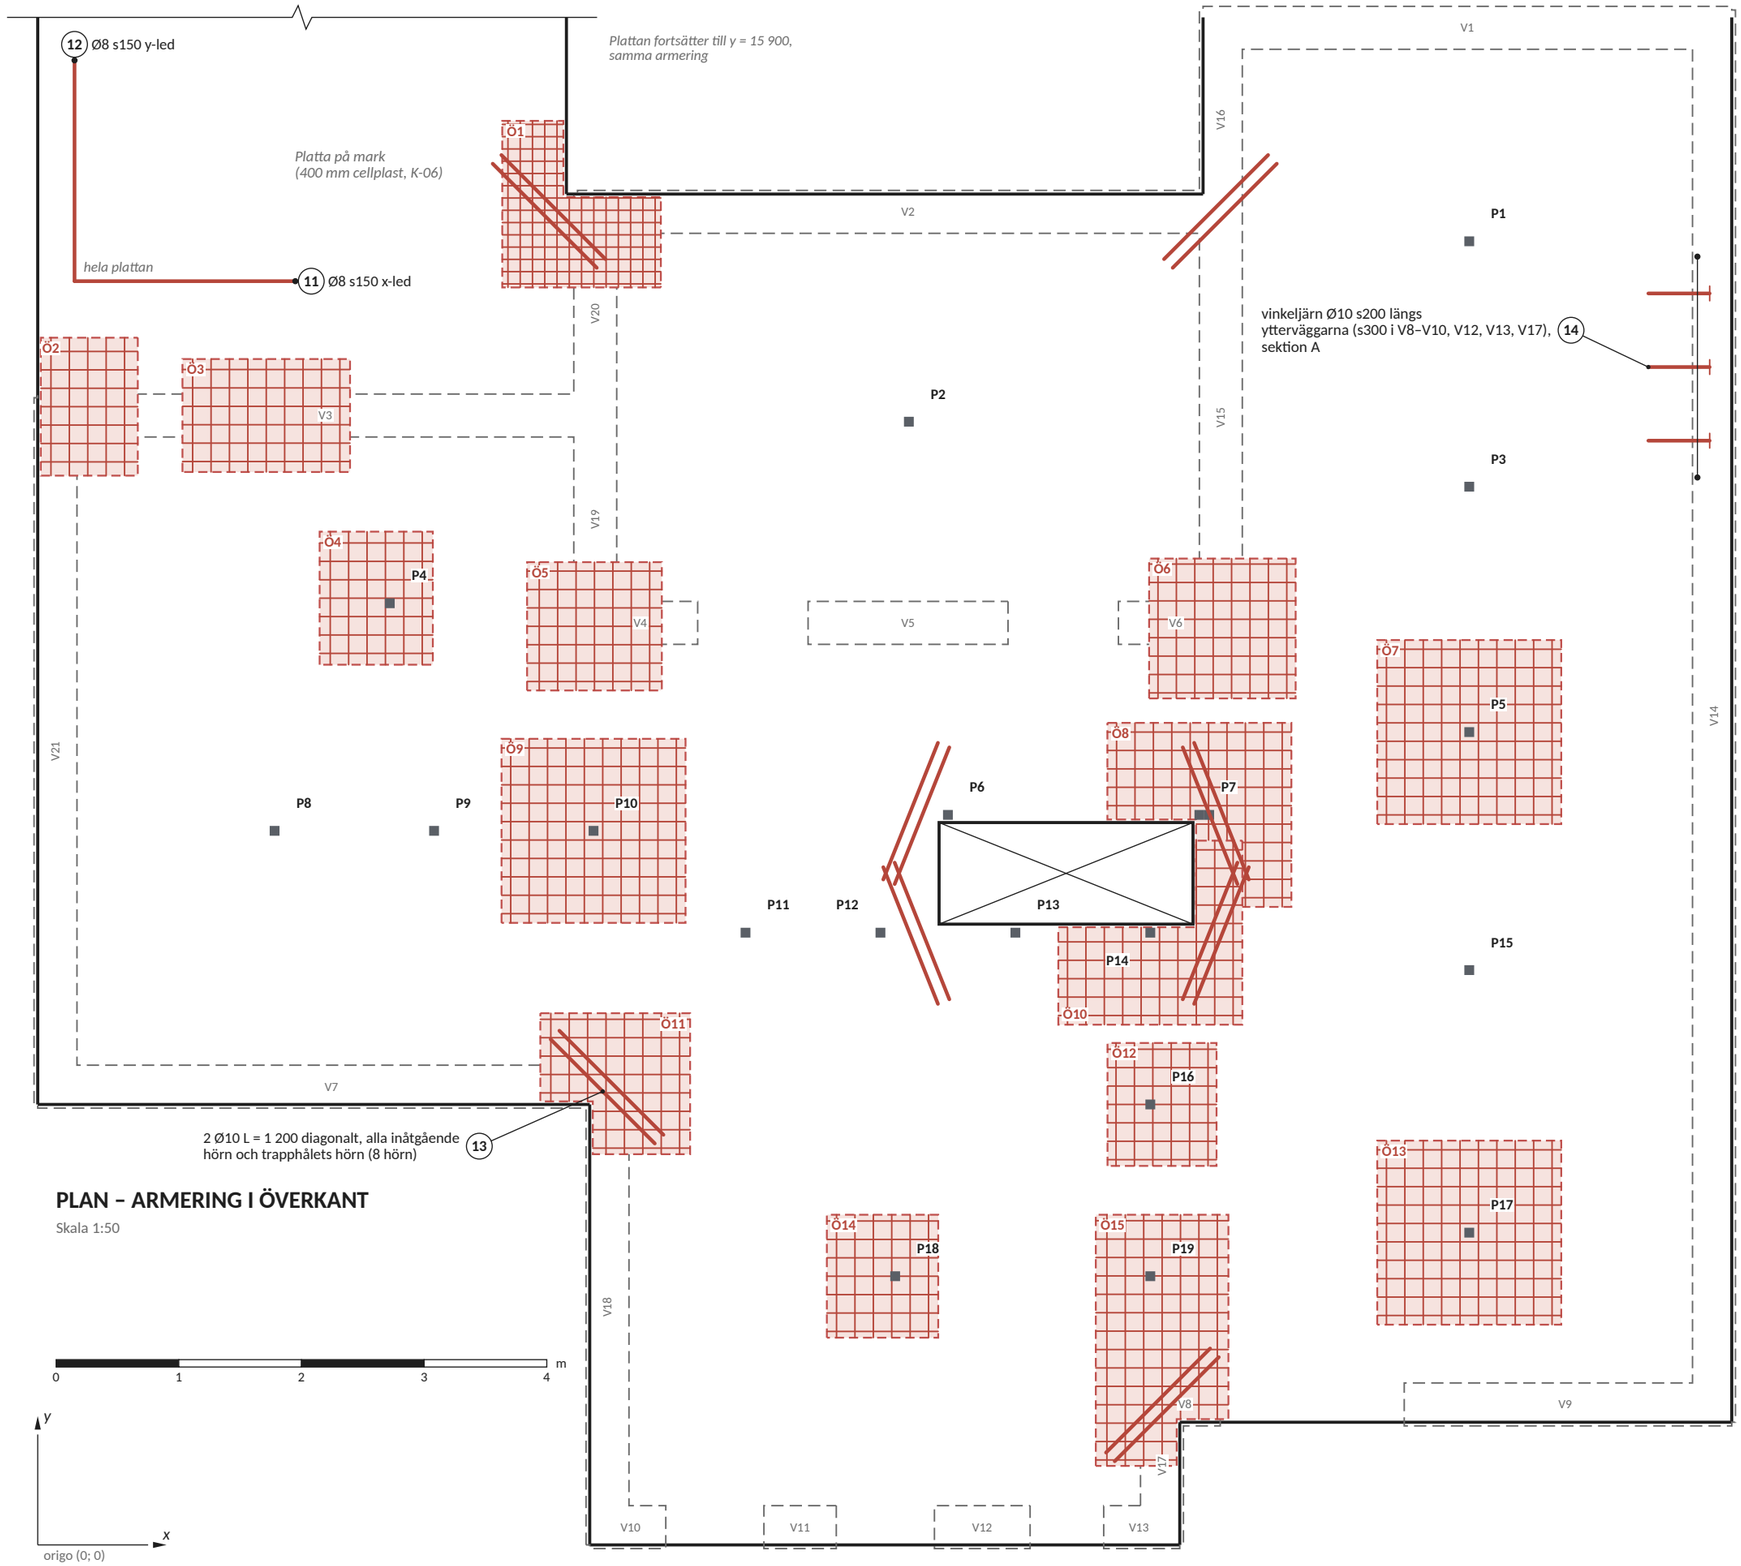

PLAN – ARMERING I ÖVERKANT

Skala 1:50

Anvisningar

1. Allmänt och mått, se R-06.1. Sektioner R-06.4.
2. Överkantsnätet läggs på armeringsstolar, högst 0,8 m isär.
3. Tilläggsjärnen i zonerna Ö1–Ö15 läggs i båda riktningarna i nätets lager och binds till nätet (s150: mitt emellan nätets järn). Där zonen når plattans kant förs järnen ut till kanten.
4. Vinkeljärnen pos 14 sätts i ytterväggarnas betongkärna, bundna till väggens lodräta järn och med samma avstånd (R-05.2), innan ytterväggarnas översta skift och bjälklaget gjuts (sektion A, K-06).

Teckenförklaring

- armering i överkant
- zon med tilläggsjärn i överkant
- fördelning av järn med samma position
- källarvägg under plattan
- stålrör VKR 80×80×4 (K-05)

Tilläggsjärn i överkant (antal × längd)

Zon	Järn	x-led	y-led	x (m)	y (m)
Ö1	Ø12 s100	14 st, 500–1 300	13 st, 750–1 400	3,79–5,08	10,25–11,61
Ö2	Ø8 s150	7 × 800	5 × 1 150	0,00–0,82	8,71–9,84
Ö3	Ø8 s150	6 × 1 400	9 × 950	1,18–2,55	8,74–9,67
Ö4	Ø8 s150	7 × 950	6 × 1 100	2,30–3,22	7,17–8,26
Ö5	Ø8 s150	7 × 1 100	7 × 1 050	3,99–5,09	6,96–8,01
Ö6	Ø10 s150	8 × 1 200	8 × 1 150	9,06–10,25	6,90–8,04
Ö7	Ø8 s150	10 × 1 500	10 × 1 500	10,92–12,42	5,88–7,38
Ö8	Ø10 s150	10 st, 800–1 500	10 st, 800–1 500	8,72–10,22	5,20–6,70
Ö9	Ø10 s150	10 × 1 500	10 × 1 500	3,78–5,28	5,07–6,57
Ö10	Ø10 s150	10 st, 400–1 500	10 st, 800–1 500	8,32–9,82	4,24–5,74
Ö11	Ø10 s150	8 st, 800–1 250	8 st, 750–1 150	4,10–5,32	3,18–4,33
Ö12	Ø8 s150	7 × 900	6 × 1 050	8,72–9,61	3,09–4,09
Ö13	Ø10 s150	10 × 1 500	10 × 1 500	10,92–12,42	1,79–3,29
Ö14	Ø8 s150	7 × 950	6 × 1 050	6,43–7,34	1,69–2,69
Ö15	Ø8 s150	14 st, 700–1 100	7 st, 1 700–2 050	8,63–9,71	0,64–2,69

Rev	Avser	Datum	Sign
A	Första utgåvan	2026-10-08	VO

PROJEKT

Fritidshus Trebodar, Resö, Tanum

FASTIGHET

Resö 2:66, Tanums kommun · BYGG.2025.2278

INNEHÅLL

Mellanbjälklag
Armering i överkant


SKALA	FORMAT	DATUM
1:50	A3	2026-10-08

UPPRÄTTAD	GRANSKAD	UNDERLAG
Viktor Ogeman	–	K-05 rev A, K-06 rev A

STATUS: **KONSTRUKTION** — REVISION: **A**


RITNINGSNUMMER

R-06.3

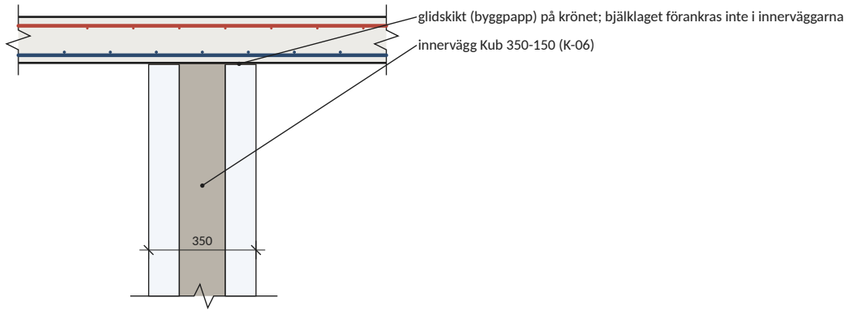


SEKTION D–D Innervägg (V15)

Skala 1:20

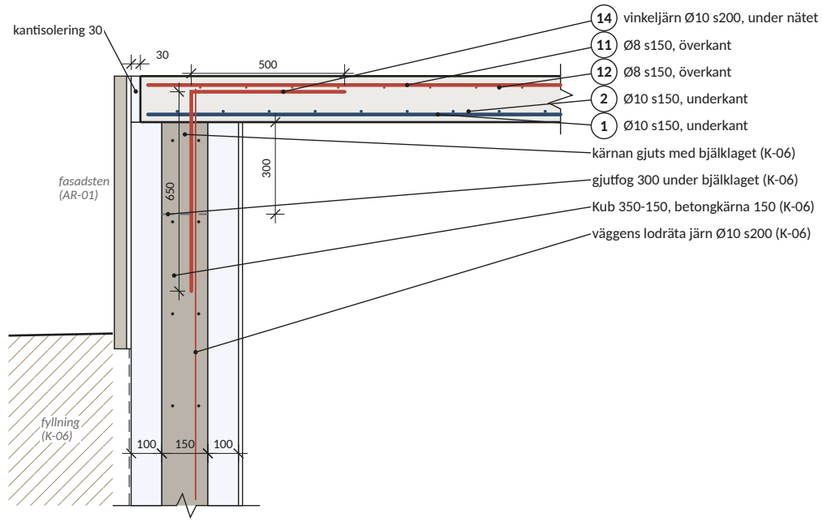


SEKTION A–A Yttervägg mot jord (V14)

Skala 1:20

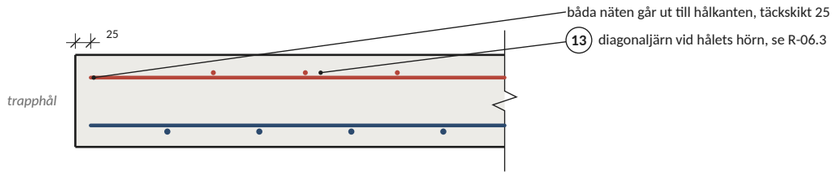

SEKTION C–C Trapphålets kant

Skala 1:10

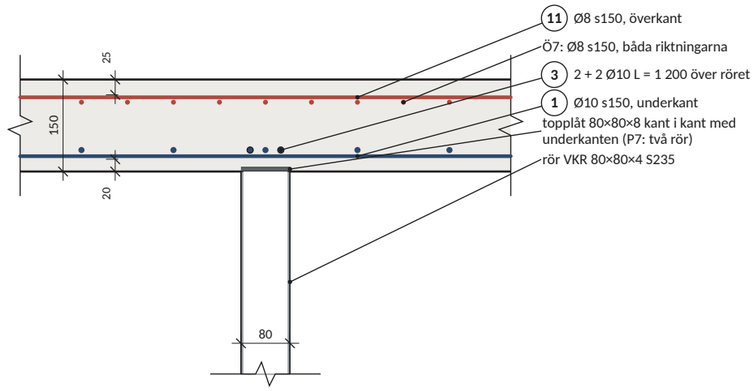

SEKTION B–B Vid rör (P5)

Skala 1:10

Anvisningar


1. Allmänt, se R-06.1.
2. Rörens topplåt gjuts in kant i kant med plattans underkant. Röret centreras under plåten. Rörens mitt enligt tabellen på R-06.2 och R-05.1; P7 är två rör tätt intill varandra.
3. Överkantsarmeringens höjd kontrolleras före gjutning, särskilt vid rören.
4. Ytterväggarnas översta halva skift gjuts samtidigt med bjälklaget, i den ordning K-06 anger. Bjälklagets form och stämp står för sig själva och hänger inte i Kub-elementen. Pos 14 binds till väggens lodräta järn före gjutning.
5. Innerväggarna gjuts i hela höjden före bjälklaget och får glidskikt (byggpapp) på krönet (R-05).
6. Formrivning tidigast när betongen nått cirka 70 % av fck (provkroppar eller mognadsberäkning). Last under byggtiden högst 5 kN/m², punktlaster över rör eller vägg.
7. Trägolv limmas först när betongens relativa fuktighet är under golvlimmets gräns (mätt enligt RBK). Våtrum får sprickupptagande tätskikt.
8. Plan: underkant R-06.2, överkant R-06.3.

Teckenförklaring

- armering i underkant
- armering i överkant
- betong C30/37
- betongkärna, Kub 350-150 (K-06)
- cellplast
- fyllning
- stål

Stålförteckning, B500B

Pos	Ø	Form	s	Anm
1	Ø10	rak	s150	UK x-led
2	Ø10	rak	s150	UK y-led
11	Ø8	rak	s150	ÖK x-led
12	Ø8	rak	s150	ÖK y-led
3	Ø10	rak 1 200	–	UK över rören
3	Ø10	rak 650	–	UK över rören, vid trapphålet
13	Ø10	rak 1 200	–	ÖK diagonalt
14	Ø10	L 650+500	s200/s300	vinkeljärn
Ö-Ø8	Ø8	rak	–	zoner R-06.3
Ö-Ø10	Ø10	rak	–	zoner R-06.3
Ö-Ø12	Ø12	rak	–	zoner R-06.3

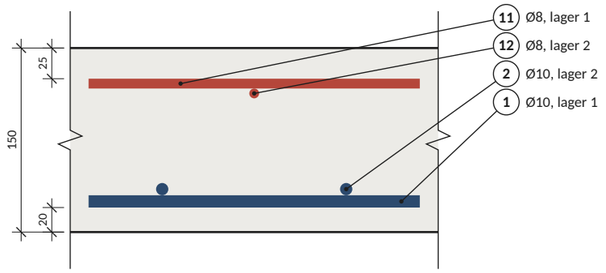

DETALJ E Armeringens lägen

Skala 1:5

Rev	Avser	Datum	Sign
A	Första utgåvan	2026-10-08	VO

PROJEKT

Fritidshus Trebodar, Resö, Tanum

FASTIGHET

Resö 2:66, Tanums kommun · BYGG.2025.2278

INNEHÅLL

Mellanbjälklag
Sektioner, detaljer och stålförteckning

SKALA	FORMAT	DATUM
1:5, 1:10, 1:20	A3	2026-10-08

UPPRÄTTAD	GRANSKAD	UNDERLAG
Viktor Ogeman	–	K-05 rev A, K-06 rev A

STATUS	REVISION
KONSTRUKTION	**A**

RITNINGSNUMMER

R-06.4