
Plan 1, golvet, belysningsstyrka

Skala 1:75

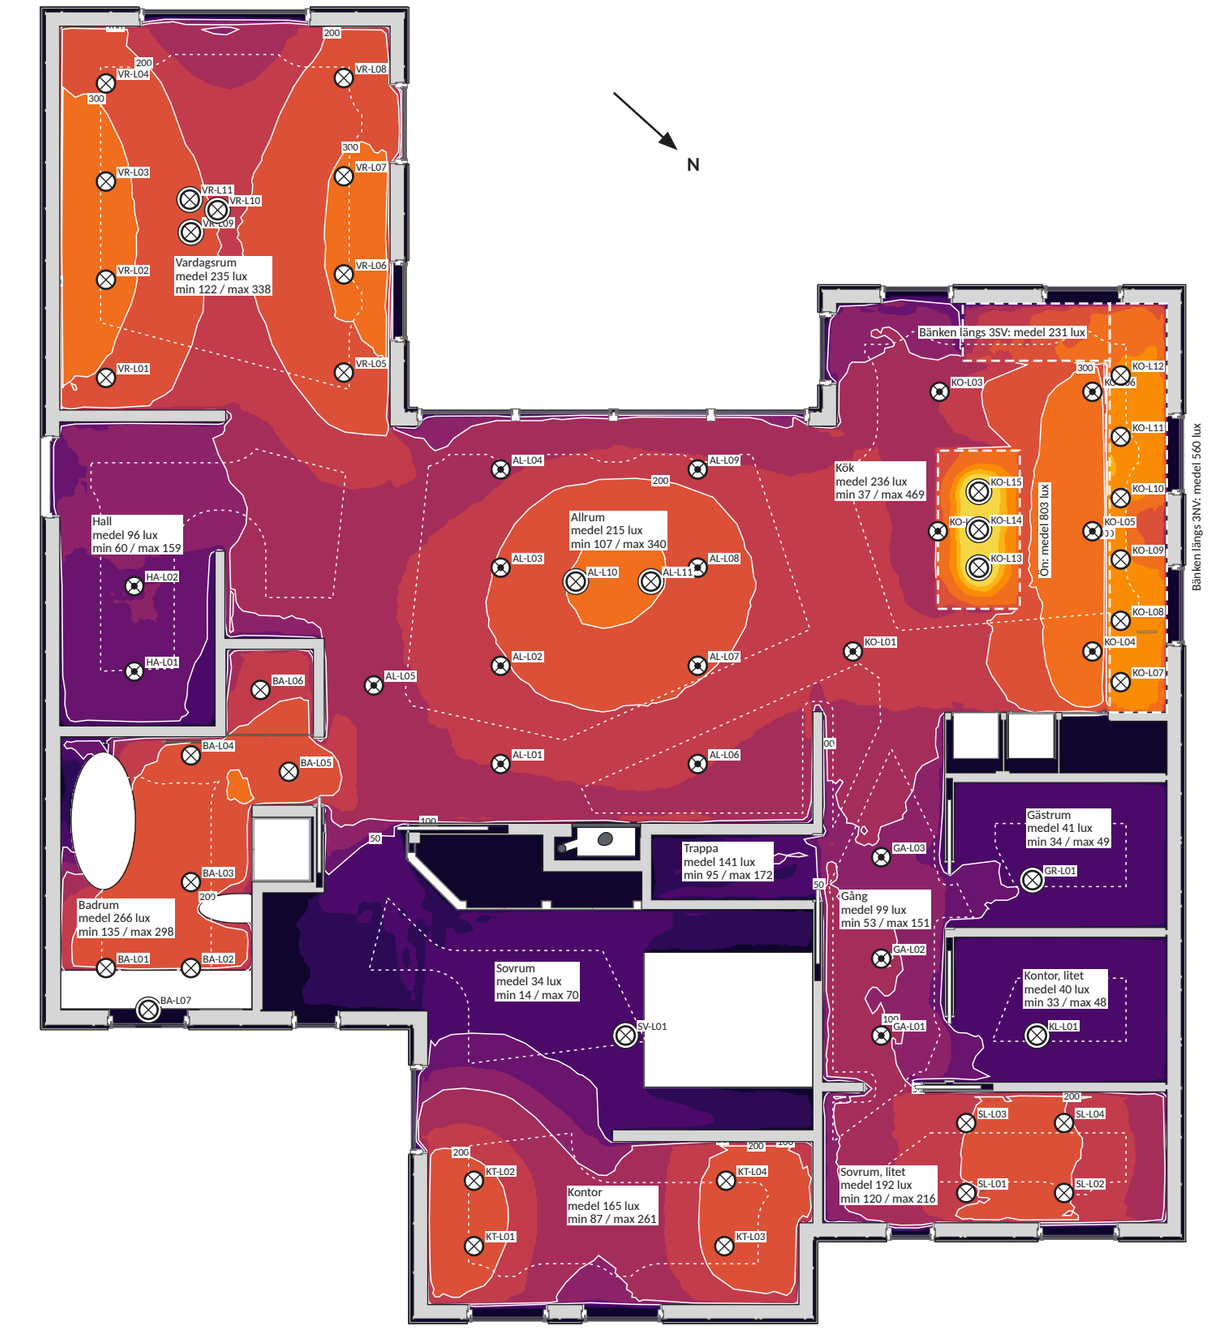

Belysningsstyrka, lux

5 000
2 000
1 000
750
500
300
200
150
100
75
50
20
10
0

Rum och delområden, lux

Rum	Medel	Min	Max	Jämnhet U_0
Allrum	215	107	340	0,50
Badrum	266	135	298	0,51
Bänken längs 3NV (0,91 m)	560	170	825	0,30
Bänken längs 3SV (0,91 m)	231	85	462	0,37
Gästrum	41	34	49	0,82
Gång	99	53	151	0,54
Hall	96	60	159	0,62
Kontor	165	87	261	0,53
Kontor, litet	40	33	48	0,83
Kök	236	37	469	0,16
Sovrum	34	14	70	0,42
Sovrum, litet	192	120	216	0,63
Trappa	141	95	172	0,67
Vardagsrum	235	122	338	0,52
Ön (0,91 m)	803	188	1 985	0,23

Anvisningar

1. Belysningsstyrkan på en vågrät yta 0,04 m över golvet, i rutor om 50 mm, ur renderingen i Blender (Cycles): armaturernas uppmätta ljusfördelning (tillverkarnas fotometrifiler), dagsljuset och reflexerna i rummen. Delområdena Bänken längs 3NV, Bänken längs 3SV och Ön mäts på en vågrät yta 0,91 m över golvet.
2. Tända: AL-T1 Allrum, tubspotar sydost; AL-T2 Allrum, tubspotar nordväst; AL-T3 Allrum, PH 5 över bordet; KO-T1 Kök, tubspotar mot taket; KO-T2 Kök, spotar mot bänken; KO-T3 Kök, Stav över ön; GA-T1 Gång, tubspotar; HA-T1 Hall, tubspotar; VR-T1 Vardagsrum, spotar sydost; VR-T2 Vardagsrum, spotar nordväst; VR-T3 Vardagsrum, VL45; BA-T1 Badrum, spotar; BA-T2 Badrum, lampan över tvättstället; SV-T1 Sovrum, glob; KT-T1 Kontor, spotar mot väggarna; SL-T1 Sovrum litet, spotar mot gaveln; SL-T2 Sovrum litet, spotar mot L1; KL-T1 Kontor litet, glob; GR-T1 Gästrum, glob; KA-T6 Källaren, det stora rummet; KA-T7 Källaren, det lilla rummet väster om KL2; KA-T8 Källaren, det lilla rummet öster om KL2; taklamporna kallare (10 LED-paneler 600 × 600 mm, 2 500 lm och 3 000 K).
3. Inget dagsljus (2026-12-21 kl. 22:00).
4. Statistiken per rum utan en kantzon på 0,5 m längs väggarna (SS-EN 12464-1), i små rum mindre, och utan inredningen på mätytan (skåp, säng och bänkskivor, vita på planen); jämnheten U_0 = minsta / medel. Rummen är de slutna ytorna mellan väggarna; en öppen planlösning delas mellan rummens namn.
5. Ritningen ritas med ./mod ljusplan (verktyg/modellering); mätytorna står i modellens el/matytor.py.

Teckenförklaring

- isolinje, med belysningsstyrkan
- rummets yta i statistiken (utan kantzonen)
- delområde med egen statistik
- armatur

Rev	Avser	Datum	Sign

PROJEKT

Fritidshus Trebodar, Resö, Tanum

FASTIGHET

Resö 2:66, Tanums kommun · BYGG.2025.2278

INNEHÅLL

Ljusplan
Plan 1, golvet

SKALA	FORMAT	DATUM
1:75	A3	2026-11-05

UPPRÄTTAD	GRANSKAD	UNDERLAG
Viktor Ogeman	–	Modellen, rendering


STATUS	REVISION
UTREDNING	**A**

RITNINGSNUMMER

U-04.1

Plan 1, bordshöjd 0,75 m, belysningsstyrka

Skala 1:75

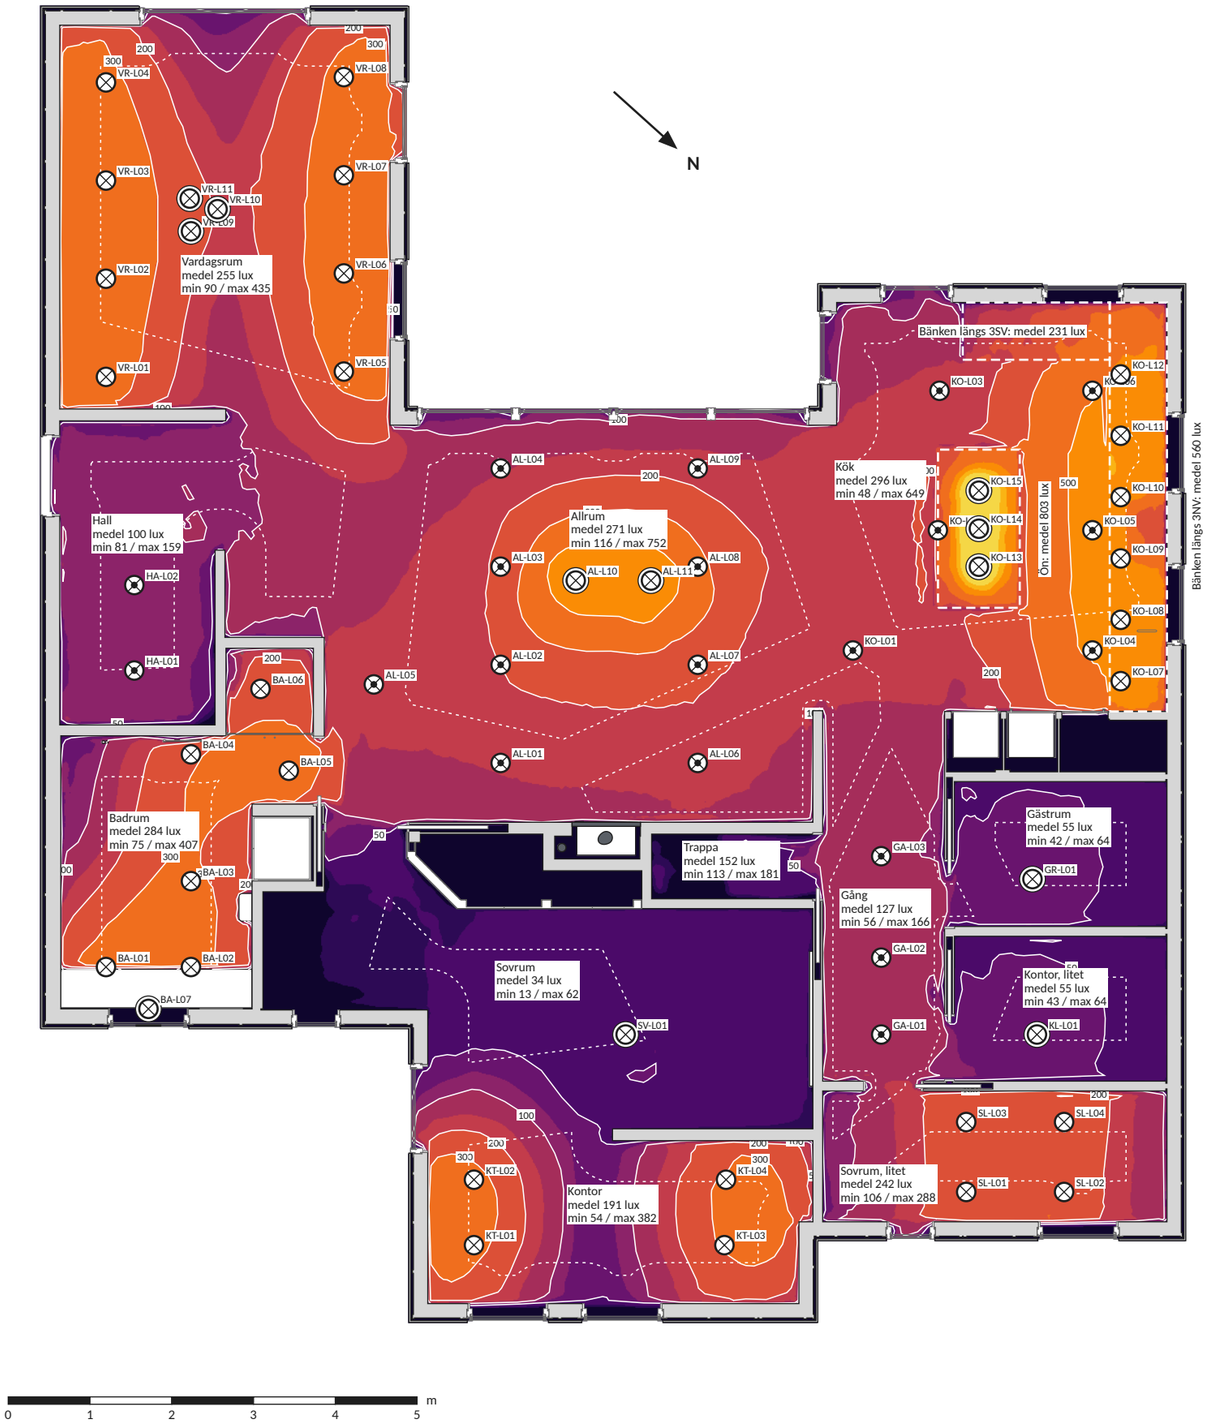

Belysningsstyrka, lux

5 000
2 000
1 000
750
500
300
200
150
100
75
50
20
10
0

Rum och delområden, lux

Rum	Medel	Min	Max	Jämnhet U_0
Allrum	271	116	752	0,43
Badrum	284	75	407	0,26
Bänken längs 3NV (0,91 m)	560	170	825	0,30
Bänken längs 3SV (0,91 m)	231	85	462	0,37
Gästrum	55	42	64	0,76
Gång	127	56	166	0,44
Hall	100	81	159	0,82
Kontor	191	54	382	0,28
Kontor, litet	55	43	64	0,78
Kök	296	48	649	0,16
Sovrum	34	13	62	0,38
Sovrum, litet	242	106	288	0,44
Trappa	152	113	181	0,74
Vardagsrum	255	90	435	0,35
Ön (0,91 m)	803	188	1 985	0,23

Anvisningar

1. Belysningsstyrkan på en vågrät yta 0,75 m över golvet, i rutor om 50 mm, ur renderingen i Blender (Cycles): armaturernas uppmätta ljusfördelning (tillverkarnas fotometrifiler), dagsljuset och reflexerna i rummen. Delområdena Bänken längs 3NV, Bänken längs 3SV och Ön mäts på en vågrät yta 0,91 m över golvet.
2. Tända: AL-T1 Allrum, tubspotar sydost; AL-T2 Allrum, tubspotar nordväst; AL-T3 Allrum, PH 5 över bordet; KO-T1 Kök, tubspotar mot taket; KO-T2 Kök, spotar mot bänken; KO-T3 Kök, Stav över ön; GA-T1 Gång, tubspotar; HA-T1 Hall, tubspotar; VR-T1 Vardagsrum, spotar sydost; VR-T2 Vardagsrum, spotar nordväst; VR-T3 Vardagsrum, VL45; BA-T1 Badrum, spotar; BA-T2 Badrum, lampan över tvättstället; SV-T1 Sovrum, glob; KT-T1 Kontor, spotar mot väggarna; SL-T1 Sovrum litet, spotar mot gaveln; SL-T2 Sovrum litet, spotar mot L1; KL-T1 Kontor litet, glob; GR-T1 Gästrum, glob; KA-T6 Källaren, det stora rummet; KA-T7 Källaren, det lilla rummet väster om KL2; KA-T8 Källaren, det lilla rummet öster om KL2; taklamporna kallare (10 LED-paneler 600 × 600 mm, 2 500 lm och 3 000 K).
3. Inget dagsljus (2026-12-21 kl. 22:00).
4. Statistiken per rum utan en kantzon på 0,5 m längs väggarna (SS-EN 12464-1), i små rum mindre, och utan inredningen på mätytan (skåp, säng och bänkskivor, vita på planen); jämnheten U_0 = minsta / medel. Rummen är de slutna ytorna mellan väggarna; en öppen planlösning delas mellan rummens namn.
5. Ritningen ritas med ./mod ljusplan (verktyg/modellering); mätytorna står i modellens el/matytor.py.

Teckenförklaring

- isolinje, med belysningsstyrkan
- rummets yta i statistiken (utan kantzonen)
- delområde med egen statistik
- armatur

Rev	Avser	Datum	Sign

PROJEKT

Fritidshus Trebodar, Resö, Tanum

FASTIGHET

Resö 2:66, Tanums kommun · BYGG.2025.2278

INNEHÅLL

Ljusplan
Plan 1, bordshöjd 0,75 m


SKALA	FORMAT	DATUM
1:75	A3	2026-11-05
UPPRÄTTAD	GRANSKAD	UNDERLAG
Viktor Ogeman	–	Modellen, rendering
STATUS		REVISION
UTREDNING		**A**

RITNINGSNUMMER

U-04.2

Köket, bänkskivorna 0,91 m, belysningsstyrka

Skala 1:50

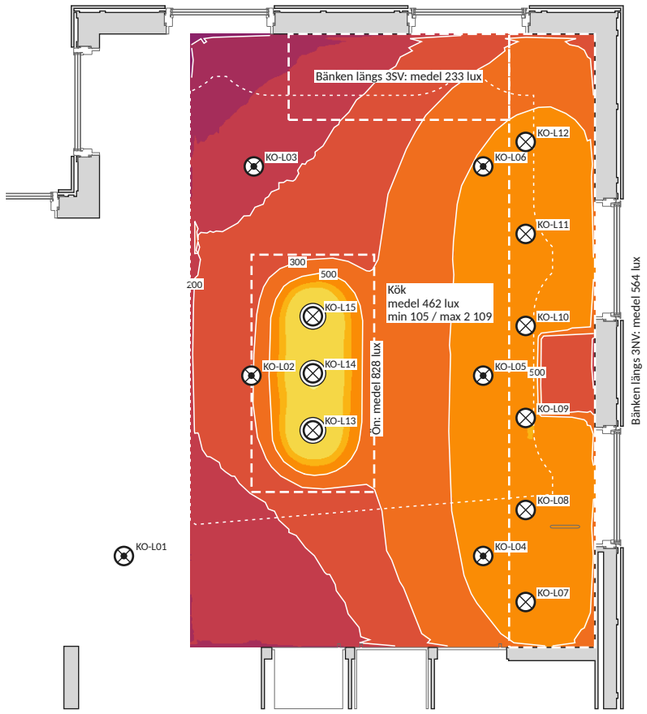

Belysningsstyrka, lux

5 000
2 000
1 000
750
500
300
200
150
100
75
50
20
10
0

Rum och delområden, lux

Rum	Medel	Min	Max	Jämnhet U_o
Bänken längs 3NV	564	173	765	0,31
Bänken längs 3SV	233	104	492	0,45
Kök	462	105	2 109	0,23
Ön	828	204	2 109	0,25

Anvisningar

1. Belysningsstyrkan på en vågrät yta 0,91 m över golvet, i rutor om 25 mm, ur renderingen i Blender (Cycles): armaturernas uppmätta ljusfördelning (tillverkarnas fotometrifiler), dagsljuset och reflexerna i rummen.
2. Tända: AL-T1 Allrum, tubspotar sydost; AL-T2 Allrum, tubspotar nordväst; AL-T3 Allrum, PH 5 över bordet; KO-T1 Kök, tubspotar mot taket; KO-T2 Kök, spotar mot bänken; KO-T3 Kök, Stav över ön; GA-T1 Gång, tubspotar; HA-T1 Hall, tubspotar; VR-T1 Vardagsrum, spotar sydost; VR-T2 Vardagsrum, spotar nordväst; VR-T3 Vardagsrum, VL45; BA-T1 Badrum, spotar; BA-T2 Badrum, lampan över tvättstället; SV-T1 Sovrum, glob; KT-T1 Kontor, spotar mot väggarna; SL-T1 Sovrum litet, spotar mot gaveln; SL-T2 Sovrum litet, spotar mot L1; KL-T1 Kontor litet, glob; GR-T1 Gästrum, glob; KA-T6 Källaren, det stora rummet; KA-T7 Källaren, det lilla rummet väster om KL2; KA-T8 Källaren, det lilla rummet öster om KL2; taklamporna kallare (10 LED-paneler 600 × 600 mm, 2 500 lm och 3 000 K).
3. Inget dagsljus (2026-12-21 kl. 22:00).
4. Statistiken per rum utan en kantzon på 0,5 m längs väggarna (SS-EN 12464-1), i små rum mindre, och utan inredningen på mätytan (skåp, säng och bänkskivor, vita på planen); jämnheten U_o = minsta / medel. Rummen är de slutna ytorna mellan väggarna; en öppen planlösning delas mellan rummens namn.
5. Ritningen ritas med ./mod ljusplan (verktyg/modellering); mätytorna står i modellens el/matytor.py.

Teckenförklaring

- isolinje, med belysningsstyrkan
- rummets yta i statistiken (utan kantzonen)
- delområde med egen statistik
- armatur

Rev	Avser	Datum	Sign

PROJEKT

Fritidshus Trebodar, Resö, Tanum

FASTIGHET

Resö 2:66, Tanums kommun · BYGG.2025.2278

INNEHÅLL

Ljusplan
Köket, bänkskivorna 0,91 m

SKALA	FORMAT	DATUM
1:50	A3	2026-11-05
UPPRÄTTAD: Viktor Ogeman	GRANSKAD: –	UNDERLAG: Modellen, rendering
STATUS: **UTREDNING**		REVISION: **A**

RITNINGSNUMMER

U-04.3

Källaren, golvet, belysningsstyrka

Skala 1:75



Belysningsstyrka, lux

5 000
2 000
1 000
750
500
300
200
150
100
75
50
20
10
0

Rum och delområden, lux

Rum	Medel	Min	Max	Jämnhet U_o
Hall	523	439	625	0,84
Källare	252	0	337	0,00
Rum söder om hallen	614	443	702	0,72
Rum söder om trapphallen	403	88	470	0,22
Rum öster om KL2	669	357	778	0,53
Stora rummet	510	103	697	0,20
Teknikrum	168	0	368	0,00
Trapphall	328	249	353	0,76

Anvisningar

1. Belysningsstyrkan på golvet, i rutor om 50 mm, ur renderingen i Blender (Cycles): armaturernas uppmätta ljusfördelning (tillverkarnas fotometrifiler), dagsljuset och reflexerna i rummen.
2. Tända: AL-T1 Allrum, tubspotar sydost; AL-T2 Allrum, tubspotar nordväst; AL-T3 Allrum, PH 5 över bordet; KO-T1 Kök, tubspotar mot taket; KO-T2 Kök, spotar mot bänken; KO-T3 Kök, Stav över ön; GA-T1 Gång, tubspotar; HA-T1 Hall, tubspotar; VR-T1 Vardagsrum, spotar sydost; VR-T2 Vardagsrum, spotar nordväst; VR-T3 Vardagsrum, VL45; BA-T1 Badrum, spotar; BA-T2 Badrum, lampan över tvättstället; SV-T1 Sovrum, glob; KT-T1 Kontor, spotar mot väggarna; SL-T1 Sovrum litet, spotar mot gaveln; SL-T2 Sovrum litet, spotar mot L1; KL-T1 Kontor litet, glob; GR-T1 Gästrum, glob; KA-T6 Källaren, det stora rummet; KA-T7 Källaren, det lilla rummet väster om KL2; KA-T8 Källaren, det lilla rummet öster om KL2; taklamporna kallare (10 LED-paneler 600 × 600 mm, 2 500 lm och 3 000 K).
3. Inget dagsljus (2026-12-21 kl. 22:00).
4. Statistiken per rum utan en kantzon på 0,5 m längs väggarna (SS-EN 12464-1), i små rum mindre, och utan inredningen på mätytan (skåp, säng och bänkskivor, vita på planen); jämnheten U_o = minsta / medel. Rummen är de slutna ytorna mellan väggarna; en öppen planlösning delas mellan rummens namn.
5. Ritningen ritas med ./mod ljusplan (verktyg/modellering); mätytorna står i modellens el/matytor.py.

Teckenförklaring

- isolinje, med belysningsstyrkan
- rummets yta i statistiken (utan kantzonen)
- delområde med egen statistik
- armatur
- taklampa (LED-panel)

Rev	Avser	Datum	Sign

PROJEKT

Fritidshus Trebodar, Resö, Tanum

FASTIGHET

Resö 2:66, Tanums kommun · BYGG.2025.2278

INNEHÅLL

Ljusplan
Källaren, golvet

SKALA	FORMAT	DATUM
1:75	A3	2026-11-05
UPPRÄTTAD	GRANSKAD	UNDERLAG
Viktor Ogeman	–	Modellen, rendering
STATUS		REVISION
UTREDNING		**A**

RITNINGSNUMMER

U-04.4