Plan 1, golvet, belysningsstyrka

Skala 1:75



Belysningsstyrka, lux

5 000
2 000
1 000
750
500
300
200
150
100
75
50
20
10
0

Rum och delområden, lux

Rum	Medel	Min	Max	Jämnhet U_0
Allrum	204	109	333	0,53
Badrum	0	0	0	0,00
Bänken längs 3NV (0,91 m)	580	199	764	0,34
Bänken längs 3SV (0,91 m)	233	92	465	0,39
Gästrum	37	34	38	0,92
Gång	95	79	110	0,83
Hall	94	55	168	0,59
Kontor	163	84	258	0,52
Kontor, litet	36	33	38	0,91
Kök	236	35	449	0,15
Sovrum	27	5	67	0,20
Sovrum, litet	178	86	214	0,48
Trappa	6	5	7	0,82
Vardagsrum	234	125	343	0,53
Ön (0,91 m)	810	184	2 150	0,23

Anvisningar

1. Belysningsstyrkan på golvet, i rutor om 50 mm, ur renderingen i Blender (Cycles): armaturernas uppmätta ljusfördelning (tillverkarnas fotometrifiler), dagsljuset och reflexerna i rummen. Delområdena Bänken längs 3NV, Bänken längs 3SV och Ön mäts på en vågrät yta 0,91 m över golvet.
2. Tända: AL-T1 Allrum, tubspotar sydost; AL-T2 Allrum, tubspotar nordväst; AL-T3 Allrum, PH 5 över bordet; KO-T1 Kök, tubspotar mot taket; KO-T2 Kök, spotar mot bänken; KO-T3 Kök, Stav över ön; GA-T1 Gång, tubspotar; HA-T1 Hall, tubspotar; VR-T1 Vardagsrum, spotar sydost; VR-T2 Vardagsrum, spotar nordväst; VR-T3 Vardagsrum, VL45; SV-T1 Sovrum, glob; KT-T1 Kontor, spotar mot väggarna; SL-T1 Sovrum litet, spotar mot gaveln; SL-T2 Sovrum litet, spotar mot L1; KL-T1 Kontor litet, glob; GR-T1 Gästrum, glob; taklamporna kallare (16 LED-paneler 600 × 600 mm, 2 500 lm och 3 000 K).
3. Inget dagsljus (2026-12-21 kl. 22:00).
4. Statistiken per rum utan en kantzon på 0,5 m längs väggarna (SS-EN 12464-1), i små rum mindre, och utan inredningen på mätytan (skåp, säng och bänkskivor, vita på planen); jämnheten U_0 = minsta / medel. Rummen är de slutna ytorna mellan väggarna; en öppen planlösning delas mellan rummens namn.
5. Ritningen ritas med ./mod ljusplan (verktyg/modellering); mätytorna står i modellens el/matytor.py.

Teckenförklaring

- isolinje, med belysningsstyrkan
- rummets yta i statistiken (utan kantzonen)
- delområde med egen statistik
- armatur

Rev	Avser	Datum	Sign

PROJEKT

Fritidshus Trebodar, Resö, Tanum

FASTIGHET

Resö 2:66, Tanums kommun · BYGG.2025.2278

INNEHÅLL

Ljusplan
Plan 1, golvet


SKALA	FORMAT	DATUM
1:75	A3	2026-11-05
UPPRÄTTAD	GRANSKAD	UNDERLAG
Viktor Ogeman	–	Modellen, rendering
STATUS		REVISION
UTREDNING		**A**

RITNINGSNUMMER

U-04.1

Plan 1, bordshöjd 0,75 m, belysningsstyrka

Skala 1:75

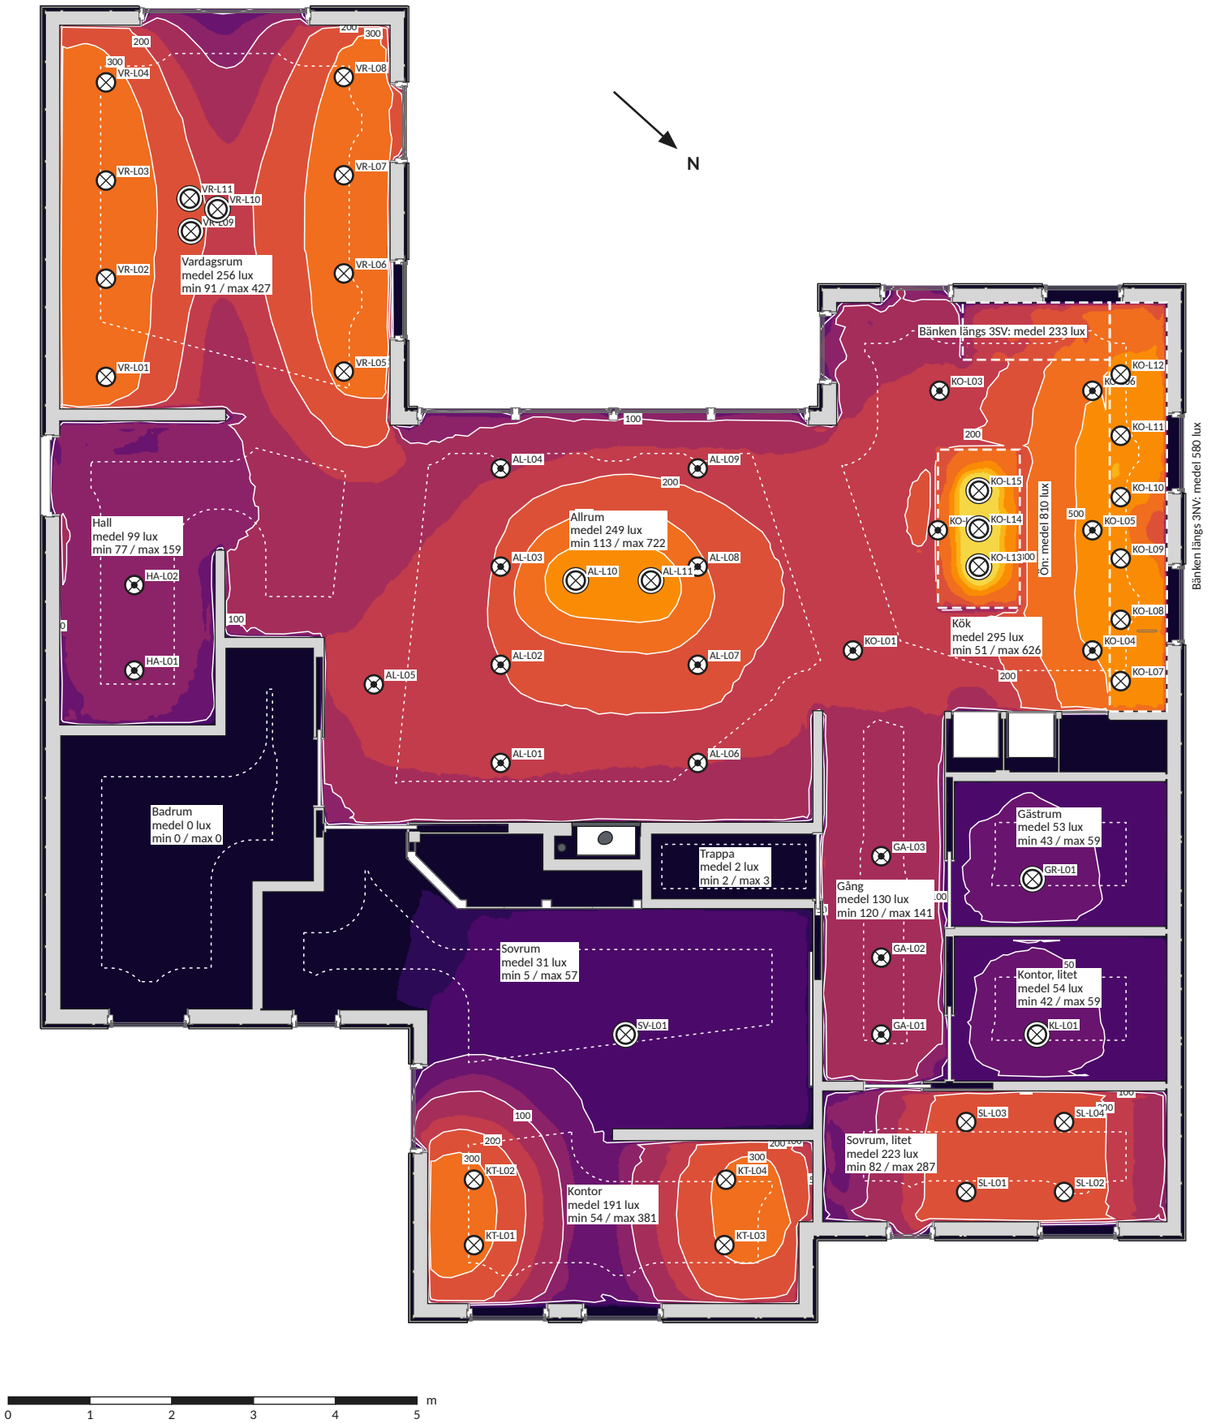

Belysningsstyrka, lux

5 000
2 000
1 000
750
500
300
200
150
100
75
50
20
10
0

Rum och delområden, lux

Rum	Medel	Min	Max	Jämnhet U_0
Allrum	249	113	722	0,45
Badrum	0	0	0	0,00
Bänken längs 3NV (0,91 m)	580	199	764	0,34
Bänken längs 3SV (0,91 m)	233	92	465	0,39
Gästrum	53	43	59	0,81
Gång	130	120	141	0,92
Hall	99	77	159	0,78
Kontor	191	54	381	0,28
Kontor, litet	54	42	59	0,78
Kök	295	51	626	0,17
Sovrum	31	5	57	0,16
Sovrum, litet	223	82	287	0,37
Trappa	2	2	3	0,75
Vardagsrum	256	91	427	0,36
Ön (0,91 m)	810	184	2 150	0,23

Anvisningar

1. Belysningsstyrkan på en vågrät yta 0,75 m över golvet, i rutor om 50 mm, ur renderingen i Blender (Cycles): armaturernas uppmätta ljusfördelning (tillverkarnas fotometrifiler), dagsljuset och reflexerna i rummen. Delområdena Bänken längs 3NV, Bänken längs 3SV och Ön mäts på en vågrät yta 0,91 m över golvet.
2. Tända: AL-T1 Allrum, tubspotar sydost; AL-T2 Allrum, tubspotar nordväst; AL-T3 Allrum, PH 5 över bordet; KO-T1 Kök, tubspotar mot taket; KO-T2 Kök, spotar mot bänken; KO-T3 Kök, Stav över ön; GA-T1 Gång, tubspotar; HA-T1 Hall, tubspotar; VR-T1 Vardagsrum, spotar sydost; VR-T2 Vardagsrum, spotar nordväst; VR-T3 Vardagsrum, VL45; SV-T1 Sovrum, glob; KT-T1 Kontor, spotar mot väggarna; SL-T1 Sovrum litet, spotar mot gaveln; SL-T2 Sovrum litet, spotar mot L1; KL-T1 Kontor litet, glob; GR-T1 Gästrum, glob; taklamporna kallare (16 LED-paneler 600 × 600 mm, 2 500 lm och 3 000 K).
3. Inget dagsljus (2026-12-21 kl. 22:00).
4. Statistiken per rum utan en kantzon på 0,5 m längs väggarna (SS-EN 12464-1), i små rum mindre, och utan inredningen på mätytan (skåp, säng och bänkskivor, vita på planen); jämnheten U_0 = minsta / medel. Rummen är de slutna ytorna mellan väggarna; en öppen planlösning delas mellan rummens namn.
5. Ritningen ritas med ./mod ljusplan (verktyg/modellering); mätytorna står i modellens el/matytor.py.

Teckenförklaring

- isolinje, med belysningsstyrkan
- rummets yta i statistiken (utan kantzonen)
- delområde med egen statistik
- armatur

Rev	Avser	Datum	Sign

PROJEKT

Fritidshus Trebodar, Resö, Tanum

FASTIGHET

Resö 2:66, Tanums kommun · BYGG.2025.2278

INNEHÅLL

Ljusplan
Plan 1, bordshöjd 0,75 m


SKALA	FORMAT	DATUM
1:75	A3	2026-11-05
UPPRÄTTAD	GRANSKAD	UNDERLAG
Viktor Ogeman	–	Modellen, rendering
STATUS		REVISION
UTREDNING		**A**

RITNINGSNUMMER

U-04.2

Köket, bänkskivorna 0,91 m, belysningsstyrka

Skala 1:50

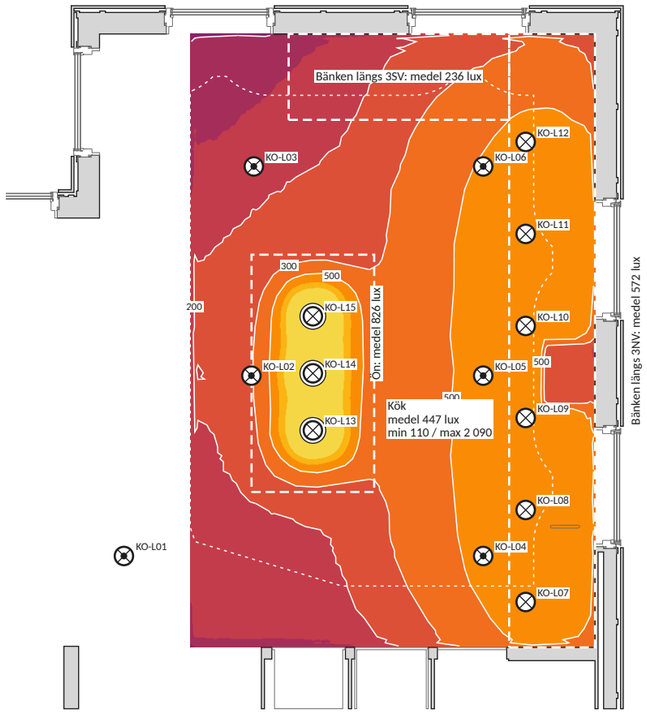

Belysningsstyrka, lux

5 000
2 000
1 000
750
500
300
200
150
100
75
50
20
10
0

Rum och delområden, lux

Rum	Medel	Min	Max	Jämnhet U_o
Bänken längs 3NV	572	151	754	0,26
Bänken längs 3SV	236	101	490	0,43
Kök	447	110	2 090	0,25
Ön	826	211	2 090	0,26

Anvisningar

1. Belysningsstyrkan på en vågrät yta 0,91 m över golvet, i rutor om 25 mm, ur renderingen i Blender (Cycles): armaturernas uppmätta ljusfördelning (tillverkarnas fotometrifiler), dagsljuset och reflexerna i rummen.
2. Tända: AL-T1 Allrum, tubspotar sydost; AL-T2 Allrum, tubspotar nordväst; AL-T3 Allrum, PH 5 över bordet; KO-T1 Kök, tubspotar mot taket; KO-T2 Kök, spotar mot bänken; KO-T3 Kök, Stav över ön; GA-T1 Gång, tubspotar; HA-T1 Hall, tubspotar; VR-T1 Vardagsrum, spotar sydost; VR-T2 Vardagsrum, spotar nordväst; VR-T3 Vardagsrum, VL45; SV-T1 Sovrum, glob; KT-T1 Kontor, spotar mot väggarna; SL-T1 Sovrum litet, spotar mot gaveln; SL-T2 Sovrum litet, spotar mot L1; KL-T1 Kontor litet, glob; GR-T1 Gästrum, glob; taklamporna kallare (16 LED-paneler 600 × 600 mm, 2 500 lm och 3 000 K).
3. Inget dagsljus (2026-12-21 kl. 22:00).
4. Statistiken per rum utan en kantzon på 0,5 m längs väggarna (SS-EN 12464-1), i små rum mindre, och utan inredningen på mätytan (skåp, säng och bänkskivor, vita på planen); jämnheten U_o = minsta / medel. Rummen är de slutna ytorna mellan väggarna; en öppen planlösning delas mellan rummens namn.
5. Ritningen ritas med ./mod ljusplan (verktyg/modellering); mätytorna står i modellens el/matytor.py.

Teckenförklaring

- isolinje, med belysningsstyrkan
- rummets yta i statistiken (utan kantzonen)
- delområde med egen statistik
- armatur

Rev	Avser	Datum	Sign

PROJEKT

Fritidshus Trebodar, Resö, Tanum

FASTIGHET

Resö 2:66, Tanums kommun · BYGG.2025.2278

INNEHÅLL

Ljusplan
Köket, bänkskivorna 0,91 m

SKALA	FORMAT	DATUM
1:50	A3	2026-11-05

UPPRÄTTAD	GRANSKAD	UNDERLAG
Viktor Ogeman	–	Modellen, rendering

STATUS	REVISION
UTREDNING	**A**

RITNINGSNUMMER

U-04.3

Källaren, golvet, belysningsstyrka

Skala 1:75



0 1 2 3 4 5 m

Belysningsstyrka, lux

5 000
2 000
1 000
750
500
300
200
150
100
75
50
20
10
0

Rum och delområden, lux

Rum	Medel	Min	Max	Jämnhet U_0
Källare	199	40	290	0,20

Anvisningar

1. Belysningsstyrkan på golvet, i rutor om 50 mm, ur renderingen i Blender (Cycles): armaturernas uppmätta ljusfördelning (tillverkarnas fotometrifiler), dagsljuset och reflexerna i rummen.
2. Tända: AL-T1 Allrum, tubspotar sydost; AL-T2 Allrum, tubspotar nordväst; AL-T3 Allrum, PH 5 över bordet; KO-T1 Kök, tubspotar mot taket; KO-T2 Kök, spotar mot bänken; KO-T3 Kök, Stav över ön; GA-T1 Gång, tubspotar; HA-T1 Hall, tubspotar; VR-T1 Vardagsrum, spotar sydost; VR-T2 Vardagsrum, spotar nordväst; VR-T3 Vardagsrum, VL45; SV-T1 Sovrum, glob; KT-T1 Kontor, spotar mot väggarna; SL-T1 Sovrum litet, spotar mot gaveln; SL-T2 Sovrum litet, spotar mot L1; KL-T1 Kontor litet, glob; GR-T1 Gästrum, glob; taklamporna kallare (16 LED-paneler 600 × 600 mm, 2 500 lm och 3 000 K).
3. Inget dagsljus (2026-12-21 kl. 22:00).
4. Statistiken per rum utan en kantzon på 0,5 m längs väggarna (SS-EN 12464-1), i små rum mindre, och utan inredningen på mätytan (skåp, säng och bänkskivor, vita på planen); jämnheten U_0 = minsta / medel. Rummen är de slutna ytorna mellan väggarna; en öppen planlösning delas mellan rummens namn.
5. Ritningen ritas med ./mod ljusplan (verktyg/modellering); mätytorna står i modellens el/matytor.py.

Teckenförklaring

- isolinje, med belysningsstyrkan
- rummets yta i statistiken (utan kantzonen)
- delområde med egen statistik
- armatur
- taklampa (LED-panel)

Rev	Avser	Datum	Sign

PROJEKT

Fritidshus Trebodar, Resö, Tanum

FASTIGHET

Resö 2:66, Tanums kommun · BYGG.2025.2278

INNEHÅLL

Ljusplan
Källaren, golvet

SKALA	FORMAT	DATUM
1:75	A3	2026-11-05
UPPRÄTTAD	GRANSKAD	UNDERLAG
Viktor Ogeman	–	Modellen, rendering
STATUS		REVISION
UTREDNING		**A**

RITNINGSNUMMER

U-04.4