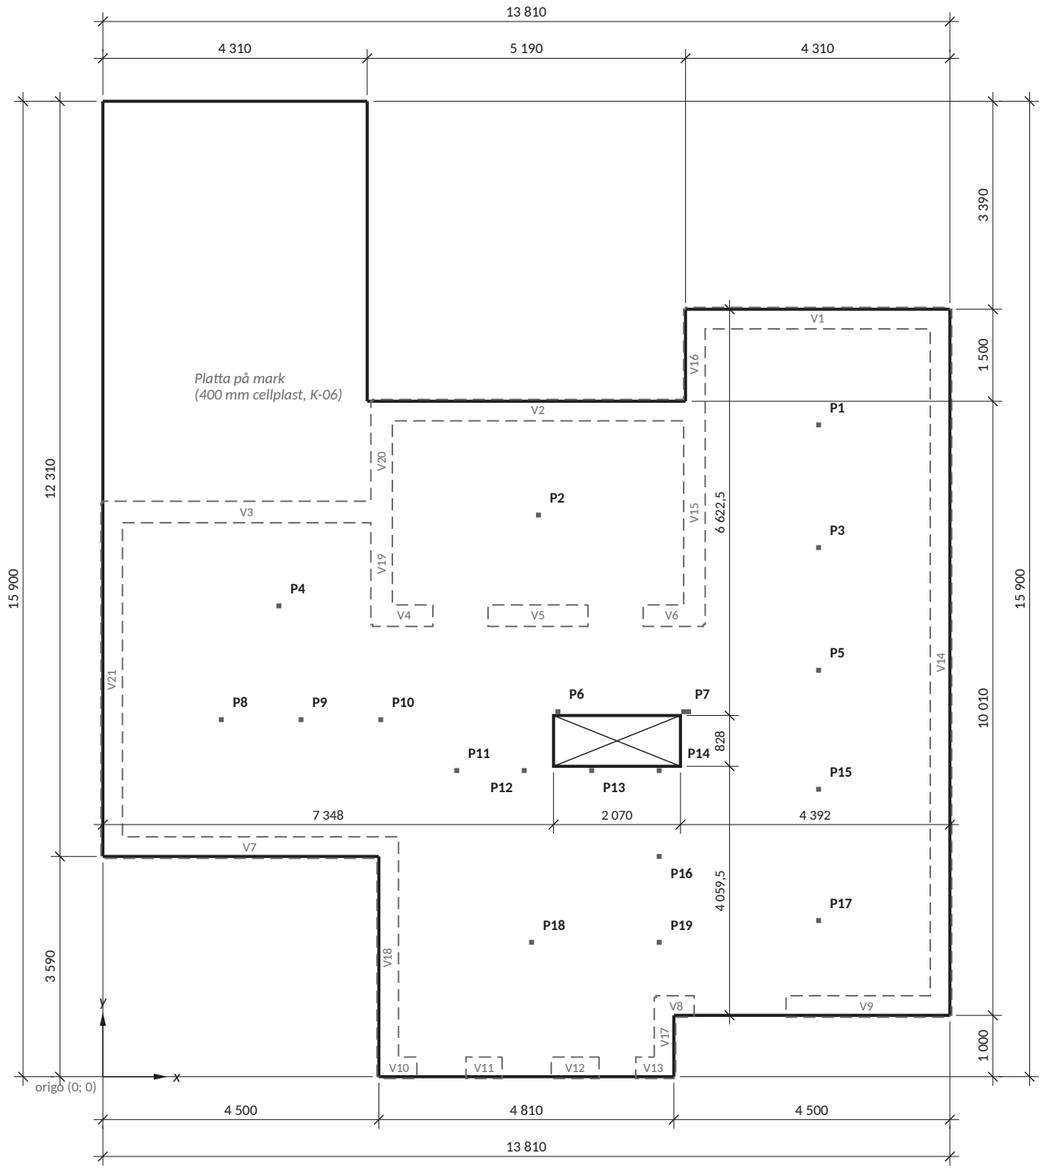


PLAN – ÖVERSIKT OCH YTTERMÅTT

Skala 1:100

0 1 2 3 4 5 m

Anvisningar

1. Betong C25/30, exponeringsklass XC1, livslängd 50 år. Armering B500B.
2. Täckskikt: underkant 20 mm, överkant 25 mm, kanter och hålkanter 25 mm, även mot de fria kanterna vid öppningarna i källarens ytterväggar.
3. Skarvlängd: Ø8 500, Ø10 650, Ø12 750 mm. Skarvar förskjuts minst 1,3 × skarvlängden.
4. Järnen i varje nät läggs i valfri ordning. Tilläggsjärn läggs i nätets lager.
5. Koordinater i mm enligt K-05; origo i skärningen mellan plattkanterna x = 0 och y = 0. Mått, se R-03.1.
6. Plattans kontur och trapphålets läge enligt denna ritning. Rörens lägen, se tabell på R-03.2.
7. Källarväggarna (Kub 350-150, R-04) under plattan streckade.

Teckenförklaring

- plattans kant
- källarvägg under plattan
- stålrör VKR 80×80×4 (K-05)

Ritningsförteckning R-03

Ritning	Innehåll	Skala
R-03.1	Översikt och yttermått	1:100
R-03.2	Armering i underkant	1:50
R-03.3	Armering i överkant	1:50
R-03.4	Sektioner, detaljer och stålförteckning	1:5, 1:10, 1:20

Rev	Avser	Datum	Sign
A	Första utgåvan	2026-10-08	VO

PROJEKT
Fritidshus Trebodar, Resö, Tanum


FASTIGHET
Resö 2:66, Tanums kommun · BYGG.2025.2278

INNEHÅLL
Mellanbjälklag
Översikt och yttermått

SKALA	FORMAT	DATUM
1:100	A3	2026-10-08
UPPRÄTTAD	GRANSKAD	UNDERLAG
Viktor Ogeman	–	K-05 rev A, K-06
STATUS		REVISION
FÖR GRANSKNING		**A**

RITNINGSNUMMER

R-03.1

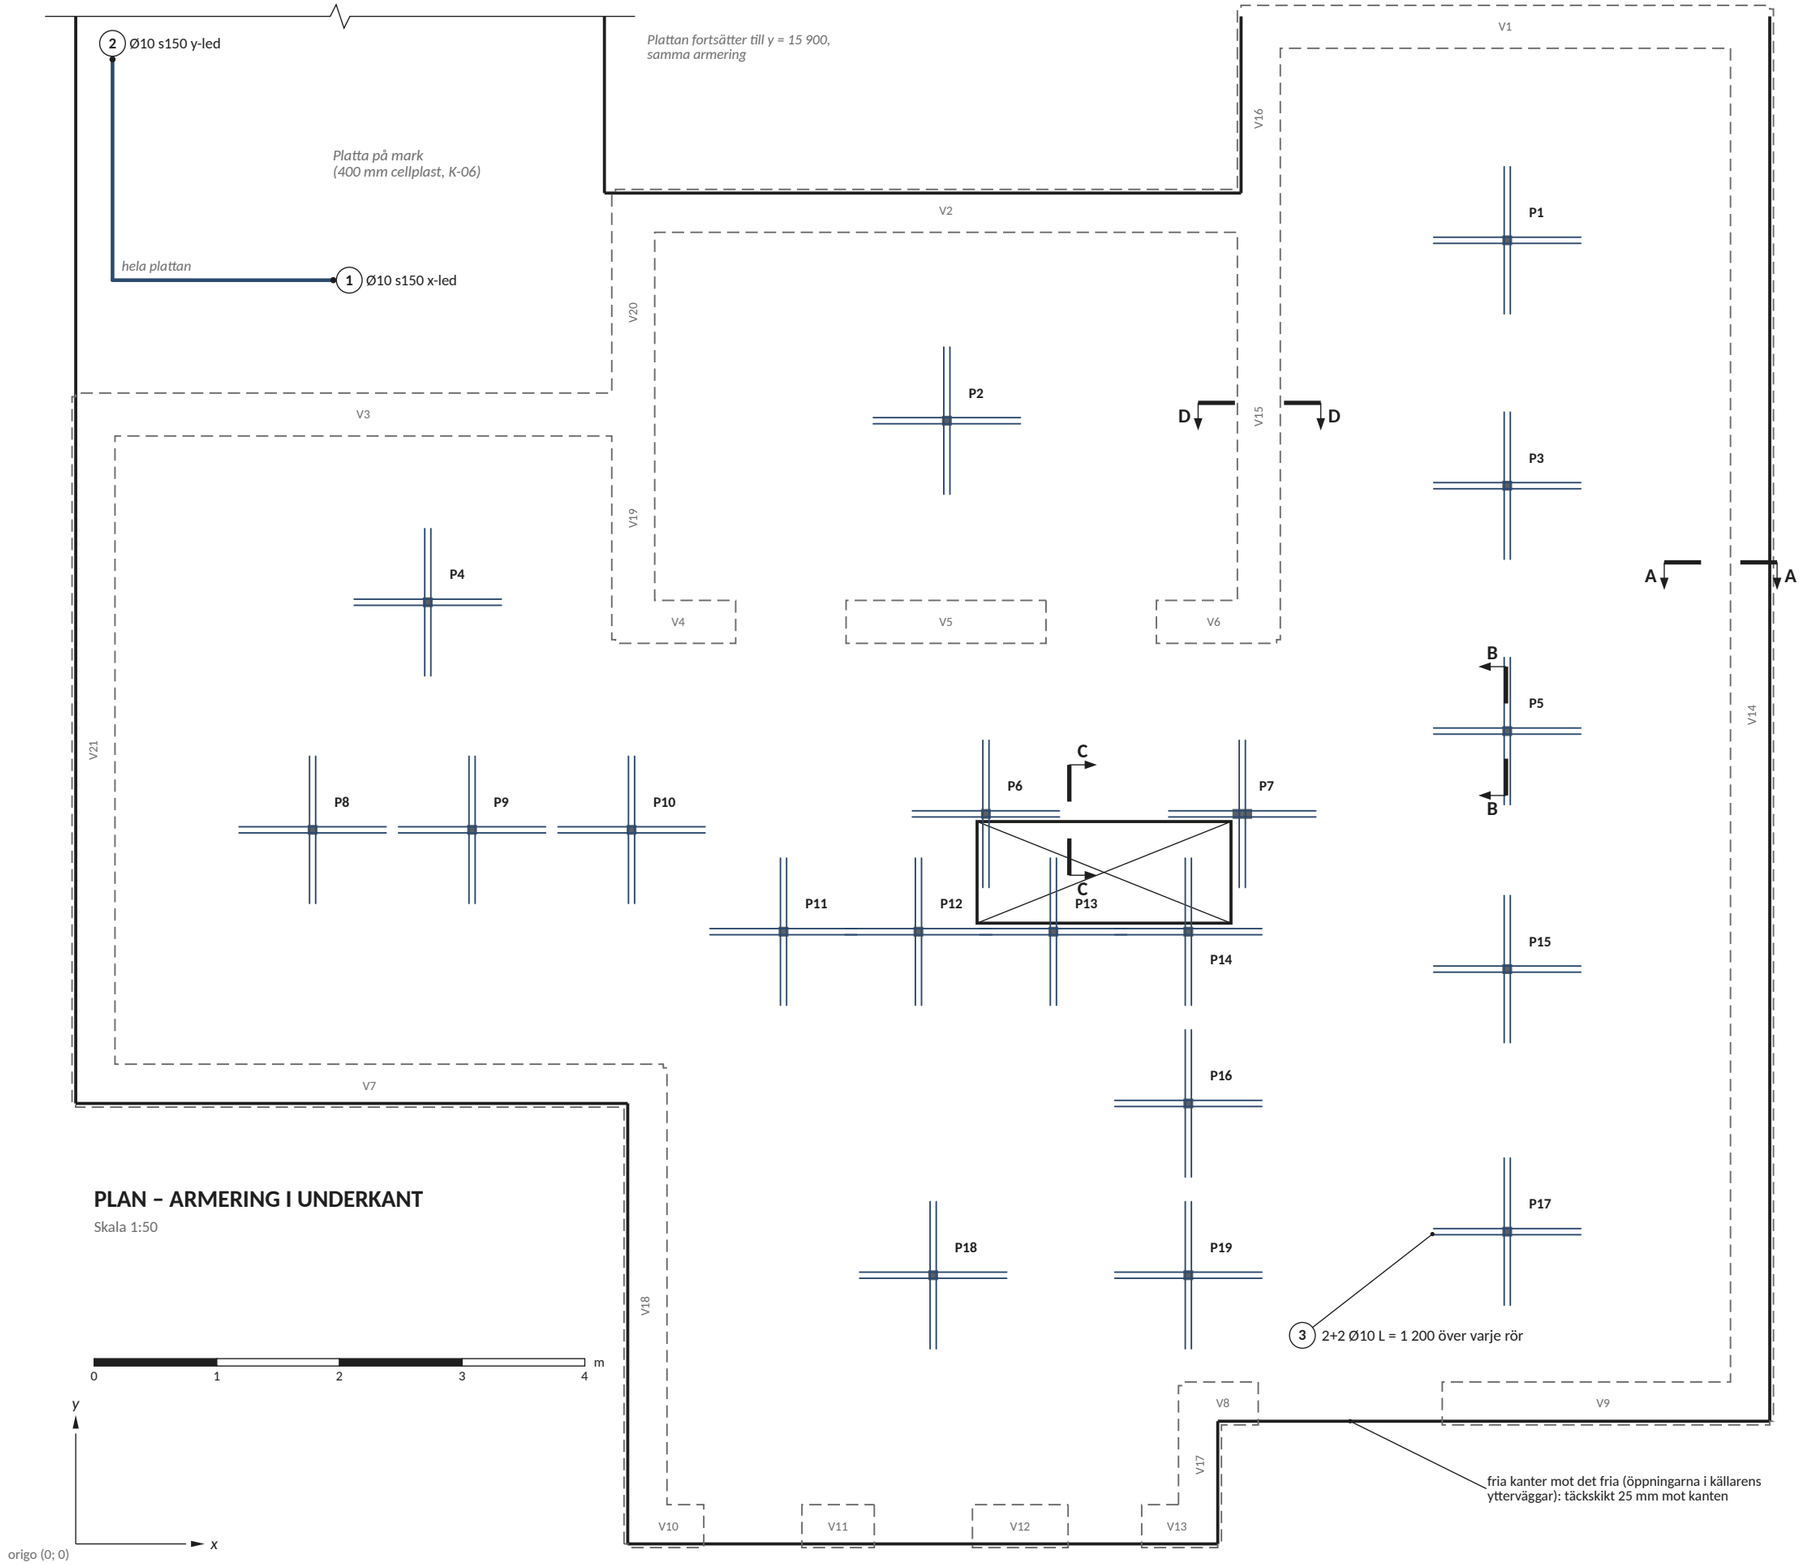

PLAN – ARMERING I UNDERKANT

Skala 1:50

Anvisningar

1. Betong C25/30, exponeringsklass XC1, livslängd 50 år. Armering B500B.
2. Täckskikt: underkant 20 mm, överkant 25 mm, kanter och hålkanter 25 mm, även mot de fria kanterna vid öppningarna i källarens ytterväggar.
3. Skarvlängd: Ø8 500, Ø10 650, Ø12 750 mm. Skarvar förskjuts minst 1,3 × skarvlängden.
4. Järnen i varje nät läggs i valfri ordning. Tilläggsjärn läggs i nätets lager.
5. Koordinater i mm enligt K-05; origo i skärningen mellan plattkanterna x = 0 och y = 0. Mått, se R-03.1.
6. Underkantsnätet läggs på distanser 20 mm, högst 0,8 m isär.
7. Minst två underkantsjärn i vardera riktningen ska passera över varje rör (SS-EN 1992-1-1 9.4.1(3)): pos 3, bundna till nätet.
8. Överkant, se R-03.3. Sektioner A–D, se R-03.4.

Teckenförklaring

- armering i underkant
- (1) positionsnummer (stålförteckning R-03.4)
- – – – källarvägg under plattan
- ■ stålrör VKR 80×80×4 (K-05)

Rör och topplåtar

Rör	x	y	Topplåt
P1	11 670	10 625	80×80×8
P2	7 102	9 155	80×80×8
P3	11 670	8 625	80×80×8
P4	2 870	7 675	80×80×8
P5	11 670	6 625	80×80×8
P6	7 420	5 950	80×80×8
P7	9 470 och 9 550	5 950	två rör tätt intill varandra, 80×80×8 på vart
P8	1 931	5 820	80×80×8
P9	3 231	5 820	80×80×8
P10	4 531	5 820	80×80×8
P11	5 770	4 990	80×80×8
P12	6 870	4 990	80×80×8
P13	7 970	4 990	80×80×8
P14	9 070	4 990	80×80×8
P15	11 670	4 685	80×80×8
P16	9 070	3 590	80×80×8
P17	11 670	2 545	80×80×8
P18	6 990	2 190	80×80×8
P19	9 070	2 190	80×80×8

Rev	Avser	Datum	Sign
A	Första utgåvan	2026-10-08	VO

PROJEKT

Fritidshus Trebodar, Resö, Tanum

FASTIGHET

Resö 2:66, Tanums kommun · BYGG.2025.2278


INNEHÅLL

Mellanbjälklag
Armering i underkant

SKALA	FORMAT	DATUM
1:50	A3	2026-10-08
UPPRÄTTAD	GRANSKAD	UNDERLAG
Viktor Ogeman	–	K-05 rev A, K-06
STATUS		REVISION
FÖR GRANSKNING		**A**

RITNINGSNUMMER

R-03.2

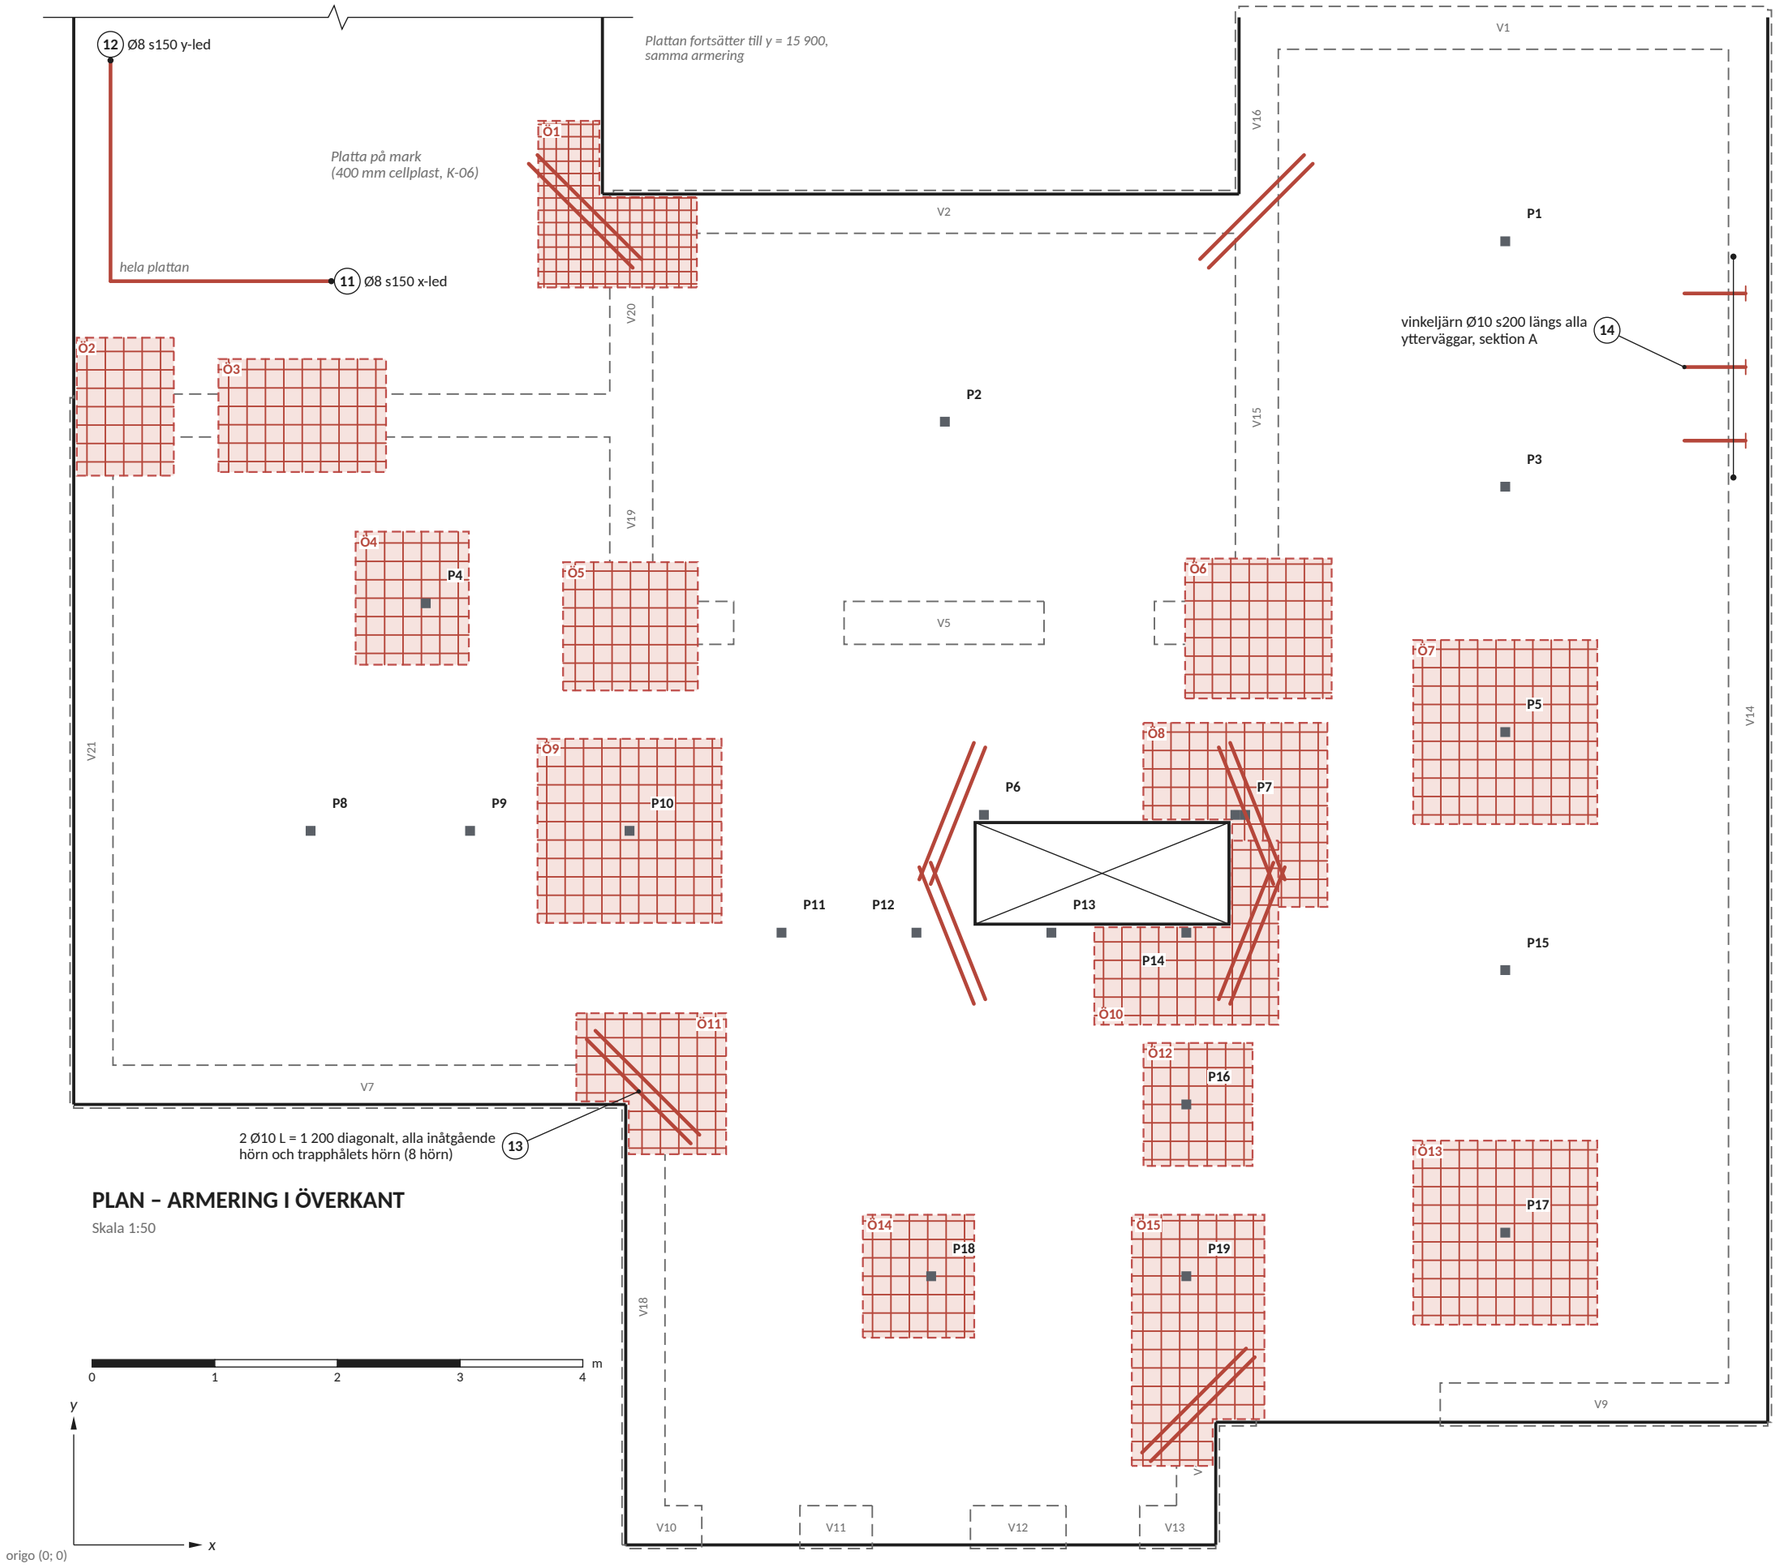

PLAN – ARMERING I ÖVERKANT

Skala 1:50

Anvisningar

1. Allmänt, se R-03.2. Mått R-03.1, sektioner R-03.4.
2. Överkantsnätet läggs på armeringsstolar, högst 0,8 m isär.
3. Tilläggsjärnen i zonerna Ö1–Ö15 läggs i båda riktningarna i nätets lager och binds till nätet (s150: mitt emellan nätets järn). Där zonen når plattans kant förs järnen ut till kanten.
4. Vinkeljärnen pos 14 sätts i ytterväggarnas betongkärna, bundna till väggens lodräta järn, innan väggarnas översta skift och bjälklaget gjuts (sektion A, K-06).

Teckenförklaring

- armering i överkant
- zon med tilläggsjärn i överkant
- fördelning av järn med samma position
- källarvägg under plattan
- stålrör VKR 80×80×4 (K-05)

Tilläggsjärn i överkant (antal × längd)

Zon	Järn	x-led	y-led	x (m)	y (m)
Ö1	Ø12 s100	14 st, 500–1 300	13 st, 750–1 400	3,79–5,08	10,25–11,61
Ö2	Ø8 s150	7 × 800	5 × 1 150	0,00–0,82	8,71–9,84
Ö3	Ø8 s150	6 × 1 400	9 × 950	1,18–2,55	8,74–9,67
Ö4	Ø8 s150	7 × 950	6 × 1 100	2,30–3,22	7,17–8,26
Ö5	Ø8 s150	7 × 1 100	7 × 1 050	3,99–5,09	6,96–8,01
Ö6	Ø10 s150	8 × 1 200	8 × 1 150	9,06–10,25	6,90–8,04
Ö7	Ø8 s150	10 × 1 500	10 × 1 500	10,92–12,42	5,88–7,38
Ö8	Ø10 s150	10 st, 800–1 500	10 st, 800–1 500	8,72–10,22	5,20–6,70
Ö9	Ø10 s150	10 × 1 500	10 × 1 500	3,78–5,28	5,07–6,57
Ö10	Ø10 s150	10 st, 400–1 500	10 st, 800–1 500	8,32–9,82	4,24–5,74
Ö11	Ø10 s150	8 st, 800–1 250	8 st, 750–1 150	4,10–5,32	3,18–4,33
Ö12	Ø8 s150	7 × 900	6 × 1 050	8,72–9,61	3,09–4,09
Ö13	Ø10 s150	10 × 1 500	10 × 1 500	10,92–12,42	1,79–3,29
Ö14	Ø8 s150	7 × 950	6 × 1 050	6,43–7,34	1,69–2,69
Ö15	Ø8 s150	14 st, 700–1 100	7 st, 1 700–2 050	8,63–9,71	0,64–2,69

Rev	Avser	Datum	Sign
A	Första utgåvan	2026-10-08	VO

PROJEKT

Fritidshus Trebodar, Resö, Tanum

FASTIGHET

Resö 2:66, Tanums kommun · BYGG.2025.2278


INNEHÅLL

Mellanbjälklag
Armering i överkant

SKALA	FORMAT	DATUM
1:50	A3	2026-10-08
UPPRÄTTAD	GRANSKAD	UNDERLAG
Viktor Ogeman	–	K-05 rev A, K-06
STATUS		REVISION
FÖR GRANSKNING		**A**


RITNINGSNUMMER

R-03.3

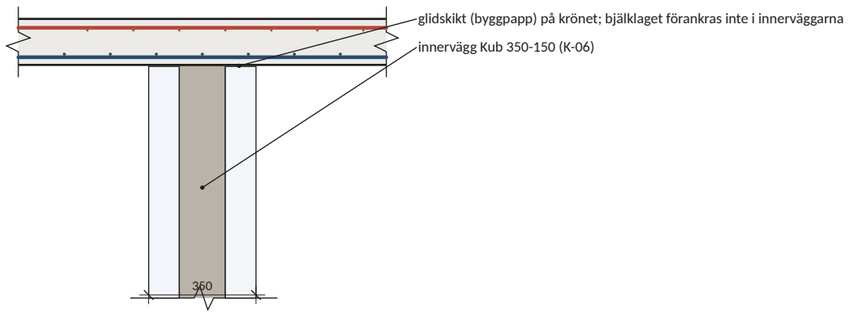


SEKTION D–D Innervägg (V15)

Skala 1:20

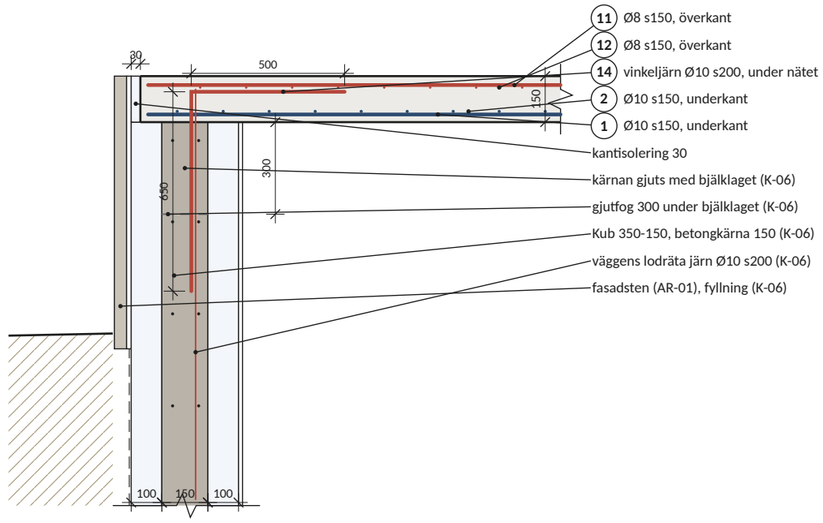

SEKTION A–A Yttervägg mot jord (V14)

Skala 1:20

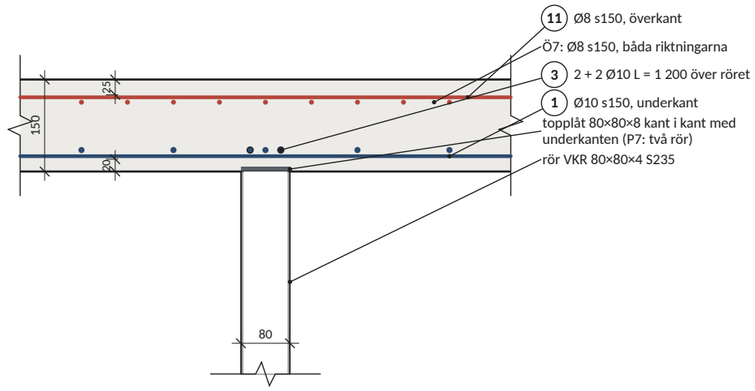

SEKTION B–B Vid rör (P5)

Skala 1:10

Anvisningar

1. Betong C25/30, exponeringsklass XC1, livslängd 50 år. Armering B500B.
2. Täckskikt: underkant 20 mm, överkant 25 mm, kanter och hålkanter 25 mm, även mot de fria kanterna vid öppningarna i källarens ytterväggar.
3. Skarvlängd: Ø8 500, Ø10 650, Ø12 750 mm. Skarvar förskjuts minst 1,3 × skarvlängden.
4. Järnen i varje nät läggs i valfri ordning. Tilläggsjärn läggs i nätets lager.
5. Rörens topplåt gjuts in kant i kant med plattans underkant. Röret centreras under plåten. Rörens mitt enligt tabellen på R-03.2 och R-04.1; P7 är två rör tätt intill varandra.
6. Överkantsarmeringens höjd kontrolleras före gjutning, särskilt vid rören.
7. Ytterväggarnas översta halva skift gjuts samtidigt med bjälklaget, i den ordning K-06 anger. Bjälklagets form och stämp står för sig själva och hänger inte i Kub-elementen. Pos 14 binds till väggens lodräta järn före gjutning.
8. Innerväggarna får glidskikt (byggpapp) på krönet.
9. Formrivning tidigast när betongen nått cirka 70 % av fck (provkroppar eller mognadsberäkning). Last under byggtiden högst 5 kN/m², punktlaster över rör eller vägg.
10. Trägolv limmas först när betongens relativa fuktighet är under golvlimmets gräns (mätt enligt RBK). Våtrum får sprickupptagande tätskikt.
11. Plan: underkant R-03.2, överkant R-03.3.


Teckenförklaring

- armering i underkant
- armering i överkant
- betong C25/30
- betongkärna, Kub 350-150 (K-06)
- cellplast
- fyllning
- stål

Stålförteckning, B500B


Pos	Ø	Form	s	Antal	L (mm)	Total (m)	Vikt (kg)	Anm
1	Ø10	rak	s150	122	var.	1 063	656	UK x-led
2	Ø10	rak	s150	106	var.	1 057	652	UK y-led
11	Ø8	rak	s150	122	var.	1 057	417	ÖK x-led
12	Ø8	rak	s150	106	var.	1 053	416	ÖK y-led
3	Ø10	rak	–	76	1 200	91	56	UK över rören
13	Ø10	rak	–	16	1 200	19	12	ÖK diagonalt
14	Ø10	L 650+500	s200	243	1 150	279	172	vinkeljärn
Ö-Ø8	Ø8	rak	–	121	var.	140	55	zoner R-03.3
Ö-Ø10	Ø10	rak	–	112	var.	138	85	zoner R-03.3
Ö-Ø12	Ø12	rak	–	27	var.	26	23	zoner R-03.3
						Summa	2 546	Ø8: 888 + Ø10: 1 634 + Ø12: 23

Näten räknade över hela plattan (även plattan på mark) med en skarv per 12 m stång. Skarvlängd Ø8 500, Ø10 650, Ø12 750 mm.

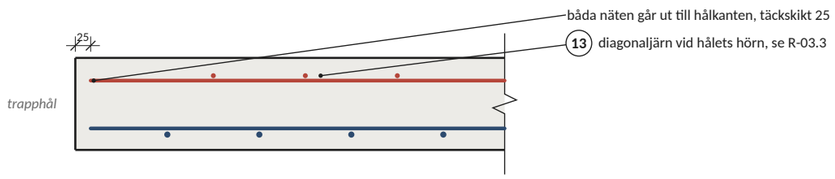

SEKTION C–C Trapphålets kant

Skala 1:10

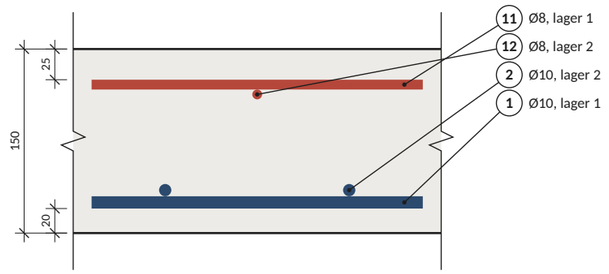

DETALJ E Armeringens lägen

Skala 1:5

Rev	Avser	Datum	Sign
A	Första utgåvan	2026-10-08	VO

PROJEKT

Fritidshus Trebodar, Resö, Tanum

FASTIGHET

Resö 2:66, Tanums kommun · BYGG.2025.2278

INNEHÅLL

Mellanbjälklag
Sektioner, detaljer och stålförteckning

SKALA	FORMAT	DATUM
1:5, 1:10, 1:20	A3	2026-10-08
UPPRÄTTAD	GRANSKAD	UNDERLAG
Viktor Ogeman	–	K-05 rev A, K-06
STATUS		REVISION
FÖR GRANSKNING		**A**

RITNINGSNUMMER

R-03.4