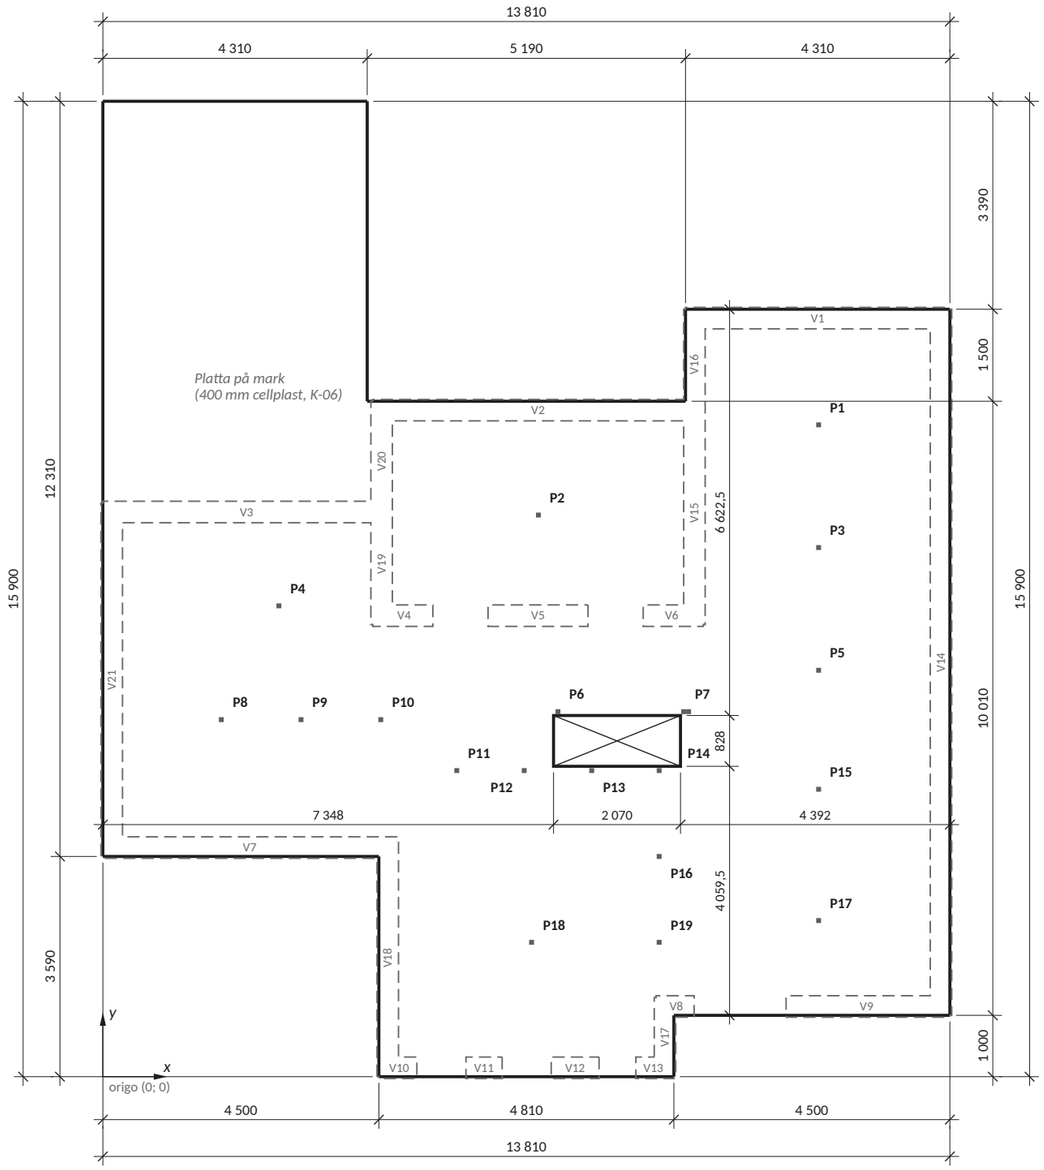



## PLAN – ÖVERSIKT OCH YTTERMÅTT

Skala 1:100

0 1 2 3 4 5 m

### Anvisningar

1. Betong C25/30, exponeringsklass XC1, livslängd 50 år. Armering B500B. Bjälklaget får gjutas med källarväggarnas betong, B30 enligt Sundolitt (K-06, R-05).
2. Täckskikt: underkant 20 mm, överkant 25 mm, kanter och hålkanter 25 mm, även mot de fria kanterna vid öppningarna i källarens ytterväggar.
3. Skarvlängd: Ø8 500, Ø10 650, Ø12 750 mm. Skarvar förskjuts minst 1,3 × skarvlängden.
4. Järnen i varje nät läggs i valfri ordning. Tilläggsjärn läggs i nätets lager.
5. Koordinater i mm enligt K-05; origo i skärningen mellan plattkanterna x = 0 och y = 0. Mått, se R-06.1.
6. Plattans kontur och trapphålets läge enligt denna ritning. Rörens lägen, se tabell på R-06.2.
7. Källarväggarna (Kub 350-150, R-05) under plattan streckade.

### Teckenförklaring

- plattans kant
- källarvägg under plattan
- stålrör VKR 80×80×4 (K-05)

### Ritningsförteckning R-06

| Ritning | Innehåll | Skala |
|---|---|---|
| R-06.1 | Översikt och yttermått | 1:100 |
| R-06.2 | Armering i underkant | 1:50 |
| R-06.3 | Armering i överkant | 1:50 |
| R-06.4 | Sektioner, detaljer och stålförteckning | 1:5, 1:10, 1:20 |

| Rev | Avser | Datum | Sign |
|---|---|---|---|
| A | Första utgåvan | 2026-10-08 | VO |

PROJEKT

**Fritidshus Trebodar, Resö, Tanum**

FASTIGHET

Resö 2:66, Tanums kommun · BYGG.2025.2278


INNEHÅLL

**Mellanbjälklag**
**Översikt och yttermått**

| SKALA | FORMAT | DATUM |
|---|---|---|
| 1:100 | A3 | 2026-10-08 |
| UPPRÄTTAD | GRANSKAD | UNDERLAG |
| Viktor Ogeman | – | K-05 rev A, K-06 rev A |
| STATUS | | REVISION |
| **KONSTRUKTION** | | **A** |

RITNINGSNUMMER

# R-06.1

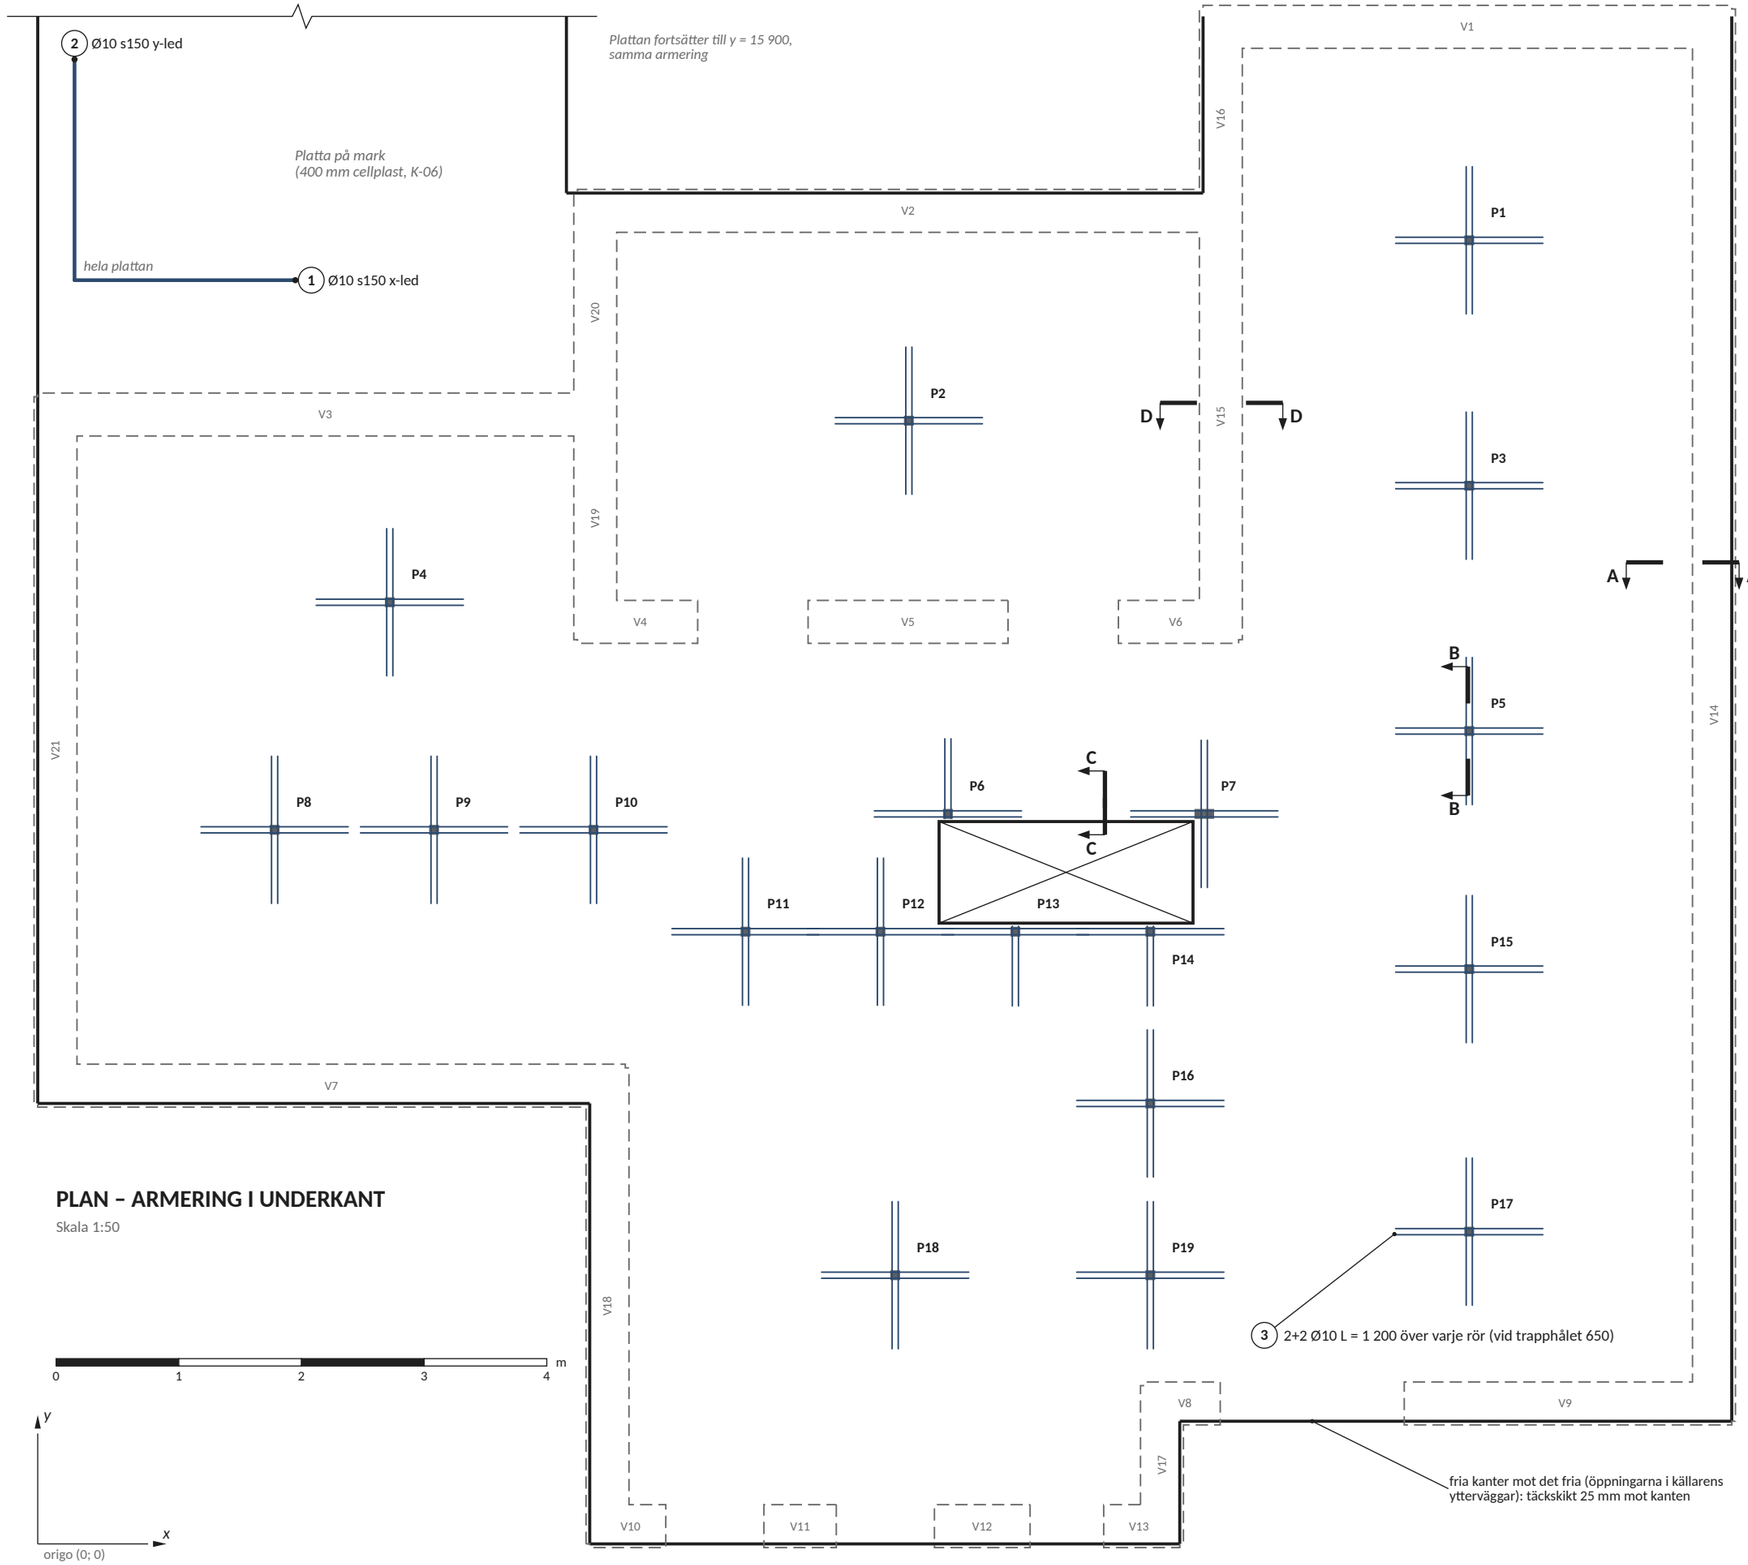


## PLAN – ARMERING I UNDERKANT

Skala 1:50

## Anvisningar

1. Betong C25/30, exponeringsklass XC1, livslängd 50 år. Armering B500B. Bjälklaget får gjutas med källarväggarnas betong, B30 enligt Sundolitt (K-06, R-05).
2. Täckskikt: underkant 20 mm, överkant 25 mm, kanter och hålkanter 25 mm, även mot de fria kanterna vid öppningarna i källarens ytterväggar.
3. Skarvlängd: Ø8 500, Ø10 650, Ø12 750 mm. Skarvar förskjuts minst 1,3 × skarvlängden.
4. Järnen i varje nät läggs i valfri ordning. Tilläggsjärn läggs i nätets lager.
5. Koordinater i mm enligt K-05; origo i skärningen mellan plattkanterna x = 0 och y = 0. Mått, se R-06.1.
6. Underkantsnätet läggs på distanser 20 mm, högst 0,8 m isär.
7. Minst två underkantsjärn i vardera riktningen ska passera över varje rör (SS-EN 1992-1-1 9.4.1(3)): pos 3, bundna till nätet. Vid trapphålet (P6, P13, P14) slutar järnen mot hålet 25 mm från hålkanten, L = 650.
8. Överkant, se R-06.3. Sektioner A–D, se R-06.4.

## Teckenförklaring

- armering i underkant
- ① positionsnummer (stålförteckning R-06.4)
- – – – källarvägg under plattan
- stålrör VKR 80×80×4 (K-05)

## Rör och topplåtar

| Rör | x | y | Topplåt |
|---|---|---|---|
| P1 | 11 670 | 10 625 | 80×80×8 |
| P2 | 7 102 | 9 155 | 80×80×8 |
| P3 | 11 670 | 8 625 | 80×80×8 |
| P4 | 2 870 | 7 675 | 80×80×8 |
| P5 | 11 670 | 6 625 | 80×80×8 |
| P6 | 7 420 | 5 950 | 80×80×8 |
| P7 | 9 470 och 9 550 | 5 950 | två rör tätt intill varandra, 80×80×8 på vart |
| P8 | 1 931 | 5 820 | 80×80×8 |
| P9 | 3 231 | 5 820 | 80×80×8 |
| P10 | 4 531 | 5 820 | 80×80×8 |
| P11 | 5 770 | 4 990 | 80×80×8 |
| P12 | 6 870 | 4 990 | 80×80×8 |
| P13 | 7 970 | 4 990 | 80×80×8 |
| P14 | 9 070 | 4 990 | 80×80×8 |
| P15 | 11 670 | 4 685 | 80×80×8 |
| P16 | 9 070 | 3 590 | 80×80×8 |
| P17 | 11 670 | 2 545 | 80×80×8 |
| P18 | 6 990 | 2 190 | 80×80×8 |
| P19 | 9 070 | 2 190 | 80×80×8 |

| Rev | Avser | Datum | Sign |
|---|---|---|---|
| A | Första utgåvan | 2026-10-08 | VO |

PROJEKT

**Fritidshus Trebodar, Resö, Tanum**

FASTIGHET

Resö 2:66, Tanums kommun · BYGG.2025.2278


INNEHÅLL

**Mellanbjälklag**
**Armering i underkant**

| SKALA | FORMAT | DATUM |
|---|---|---|
| 1:50 | A3 | 2026-10-08 |
| UPPRÄTTAD | GRANSKAD | UNDERLAG |
| Viktor Ogeman | – | K-05 rev A, K-06 rev A |
| STATUS | | REVISION |
| **KONSTRUKTION** | | **A** |

RITNINGSNUMMER

# R-06.2

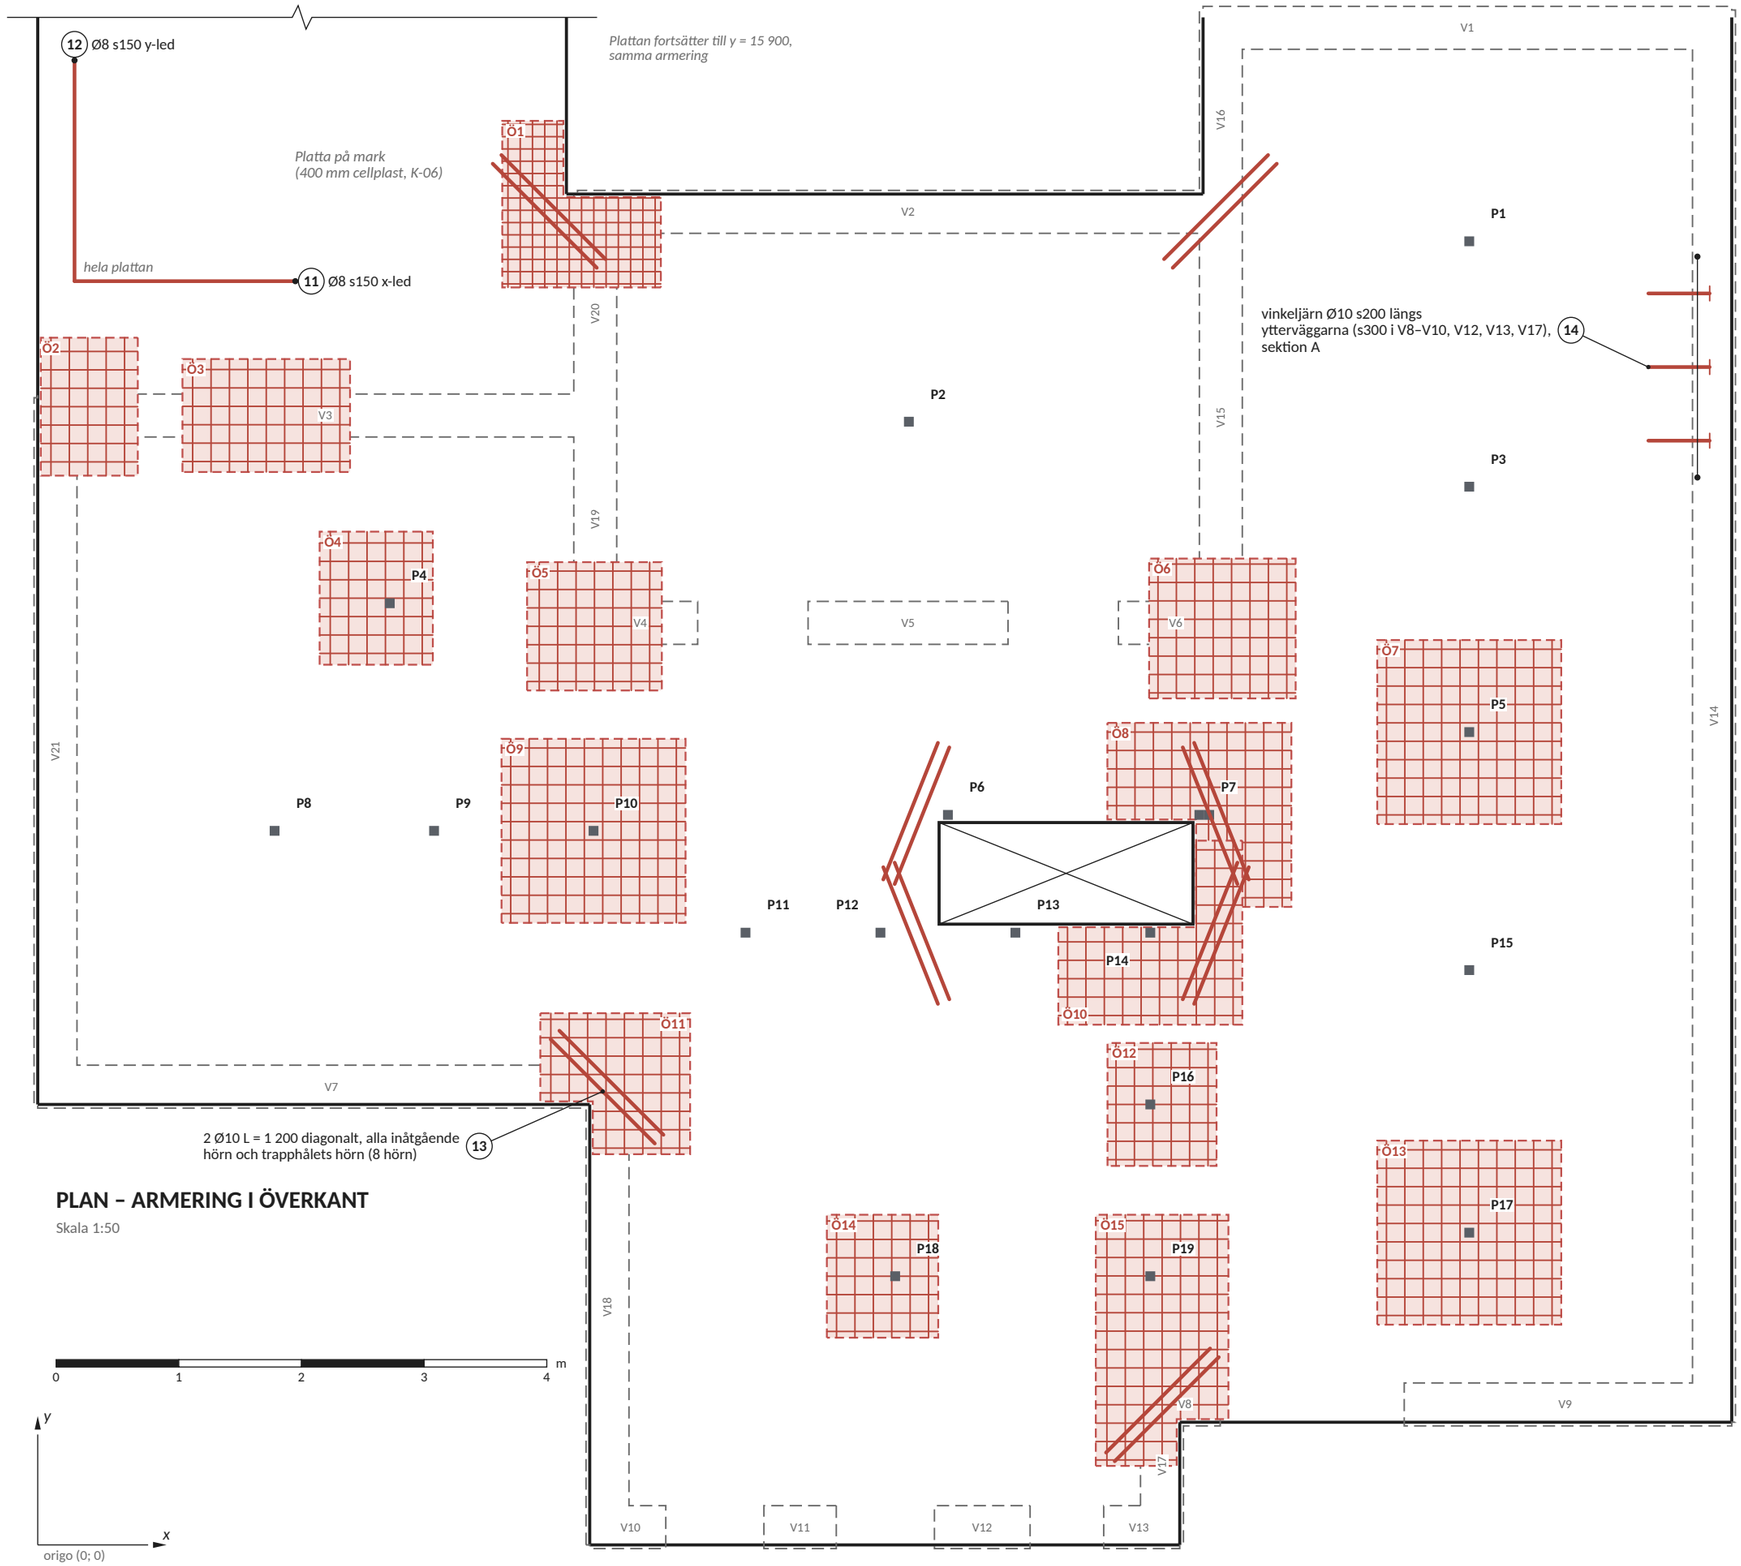


## PLAN – ARMERING I ÖVERKANT

Skala 1:50

### Anvisningar

1. Allmänt, se R-06.2. Mått R-06.1, sektioner R-06.4.
2. Överkantsnätet läggs på armeringsstolar, högst 0,8 m isär.
3. Tilläggsjärnen i zonerna Ö1–Ö15 läggs i båda riktningarna i nätets lager och binds till nätet (s150: mitt emellan nätets järn). Där zonen når plattans kant förs järnen ut till kanten.
4. Vinkeljärnen pos 14 sätts i ytterväggarnas betongkärna, bundna till väggens lodräta järn och med samma avstånd (R-05.2), innan ytterväggarnas översta skift och bjälklaget gjuts (sektion A, K-06).

### Teckenförklaring

- armering i överkant
- zon med tilläggsjärn i överkant
- fördelning av järn med samma position
- källarvägg under plattan
- stålrör VKR 80×80×4 (K-05)

### Tilläggsjärn i överkant (antal × längd)

| Zon | Järn | x-led | y-led | x (m) | y (m) |
|---|---|---|---|---|---|
| Ö1 | Ø12 s100 | 14 st, 500–1 300 | 13 st, 750–1 400 | 3,79–5,08 | 10,25–11,61 |
| Ö2 | Ø8 s150 | 7 × 800 | 5 × 1 150 | 0,00–0,82 | 8,71–9,84 |
| Ö3 | Ø8 s150 | 6 × 1 400 | 9 × 950 | 1,18–2,55 | 8,74–9,67 |
| Ö4 | Ø8 s150 | 7 × 950 | 6 × 1 100 | 2,30–3,22 | 7,17–8,26 |
| Ö5 | Ø8 s150 | 7 × 1 100 | 7 × 1 050 | 3,99–5,09 | 6,96–8,01 |
| Ö6 | Ø10 s150 | 8 × 1 200 | 8 × 1 150 | 9,06–10,25 | 6,90–8,04 |
| Ö7 | Ø8 s150 | 10 × 1 500 | 10 × 1 500 | 10,92–12,42 | 5,88–7,38 |
| Ö8 | Ø10 s150 | 10 st, 800–1 500 | 10 st, 800–1 500 | 8,72–10,22 | 5,20–6,70 |
| Ö9 | Ø10 s150 | 10 × 1 500 | 10 × 1 500 | 3,78–5,28 | 5,07–6,57 |
| Ö10 | Ø10 s150 | 10 st, 400–1 500 | 10 st, 800–1 500 | 8,32–9,82 | 4,24–5,74 |
| Ö11 | Ø10 s150 | 8 st, 800–1 250 | 8 st, 750–1 150 | 4,10–5,32 | 3,18–4,33 |
| Ö12 | Ø8 s150 | 7 × 900 | 6 × 1 050 | 8,72–9,61 | 3,09–4,09 |
| Ö13 | Ø10 s150 | 10 × 1 500 | 10 × 1 500 | 10,92–12,42 | 1,79–3,29 |
| Ö14 | Ø8 s150 | 7 × 950 | 6 × 1 050 | 6,43–7,34 | 1,69–2,69 |
| Ö15 | Ø8 s150 | 14 st, 700–1 100 | 7 st, 1 700–2 050 | 8,63–9,71 | 0,64–2,69 |

| Rev | Avser | Datum | Sign |
|---|---|---|---|
| A | Första utgåvan | 2026-10-08 | VO |

PROJEKT

**Fritidshus Trebodar, Resö, Tanum**

FASTIGHET

Resö 2:66, Tanums kommun · BYGG.2025.2278

INNEHÅLL

**Mellanbjälklag**
**Armering i överkant**

| SKALA | FORMAT | DATUM |
|---|---|---|
| 1:50 | A3 | 2026-10-08 |

| UPPRÄTTAD | GRANSKAD | UNDERLAG |
|---|---|---|
| Viktor Ogeman | – | K-05 rev A, K-06 rev A |

STATUS


**KONSTRUKTION**

REVISION

**A**


RITNINGSNUMMER

**R-06.3**

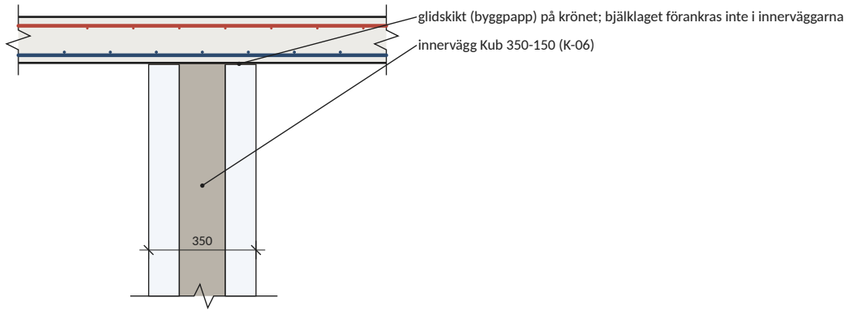



### SEKTION D–D  Innervägg (V15)

Skala 1:20

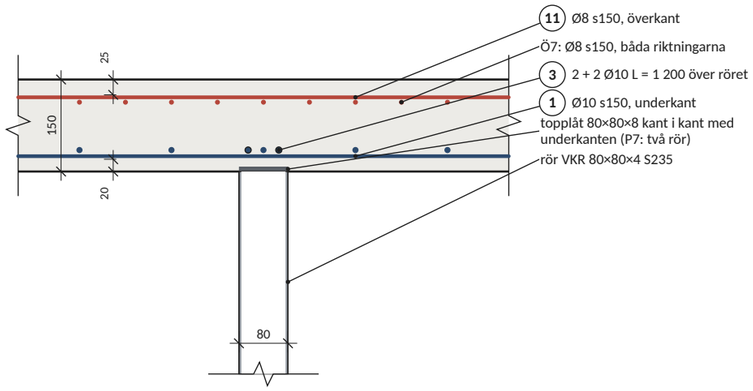



### SEKTION B–B  Vid rör (P5)

Skala 1:10

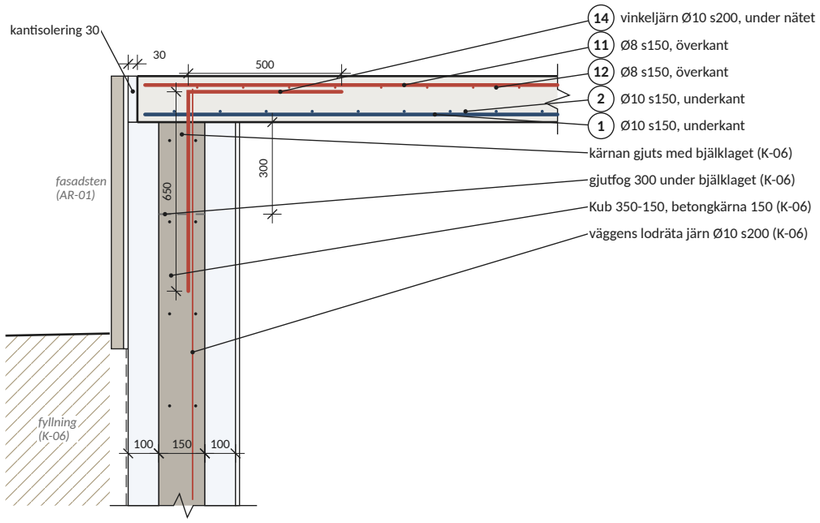


### SEKTION A–A  Yttervägg mot jord (V14)

Skala 1:20

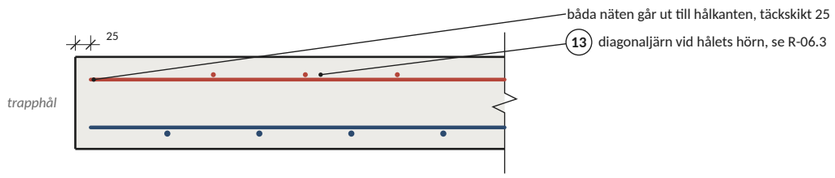


### SEKTION C–C  Trapphålets kant

Skala 1:10

## Anvisningar

1. Betong C25/30, exponeringsklass XC1, livslängd 50 år. Armering B500B. Bjälklaget får gjutas med källarväggarnas betong, B30 enligt Sundolitt (K-06, R-05).
2. Täckskikt: underkant 20 mm, överkant 25 mm, kanter och hålkanter 25 mm, även mot de fria kanterna vid öppningarna i källarens ytterväggar.
3. Skarvlängd: Ø8 500, Ø10 650, Ø12 750 mm. Skarvar förskjuts minst 1,3 × skarvlängden.
4. Järnen i varje nät läggs i valfri ordning. Tilläggsjärn läggs i nätets lager.
5. Rörens topplåt gjuts in kant i kant med plattans underkant. Röret centreras under plåten. Rörens mitt enligt tabellen på R-06.2 och R-05.1; P7 är två rör tätt intill varandra.
6. Överkantsarmeringens höjd kontrolleras före gjutning, särskilt vid rören.
7. Ytterväggarnas översta halva skift gjuts samtidigt med bjälklaget, i den ordning K-06 anger. Bjälklagets form och stämp står för sig själva och hänger inte i Kub-elementen. Pos 14 binds till väggens lodräta järn före gjutning.
8. Innerväggarna gjuts i hela höjden före bjälklaget och får glidskikt (byggpapp) på krönet (R-05).
9. Formrivning tidigast när betongen nått cirka 70 % av fck (provkroppar eller mognadsberäkning). Last under byggtiden högst 5 kN/m², punktlaster över rör eller vägg.
10. Trägolv limmas först när betongens relativa fuktighet är under golvlimmets gräns (mätt enligt RBK). Våtrum får sprickupptagande tätskikt.
11. Plan: underkant R-06.2, överkant R-06.3.


## Teckenförklaring

- armering i underkant
- armering i överkant
- betong C25/30
- betongkärna, Kub 350-150 (K-06)
- cellplast
- fyllning
- stål

## Stålförteckning, B500B

| Pos | Ø | Form | s | Antal | L (mm) | Total (m) | Vikt (kg) | Anm |
|---|---|---|---|---|---|---|---|---|
| 1 | Ø10 | rak | s150 | 122 | var. | 1 063 | 656 | UK x-led |
| 2 | Ø10 | rak | s150 | 106 | var. | 1 057 | 652 | UK y-led |
| 11 | Ø8 | rak | s150 | 122 | var. | 1 057 | 417 | ÖK x-led |
| 12 | Ø8 | rak | s150 | 106 | var. | 1 053 | 416 | ÖK y-led |
| 3 | Ø10 | rak | – | 70 | 1 200 | 84 | 52 | UK över rören |
| 3 | Ø10 | rak | – | 6 | 650 | 4 | 2 | UK över rören, vid trapphålet |
| 13 | Ø10 | rak | – | 16 | 1 200 | 19 | 12 | ÖK diagonalt |
| 14 | Ø10 | L 650+500 | s200/s300 | 236 | 1 150 | 271 | 167 | vinkeljärn |
| Ö-Ø8 | Ø8 | rak | – | 121 | var. | 140 | 55 | zoner R-06.3 |
| Ö-Ø10 | Ø10 | rak | – | 112 | var. | 138 | 85 | zoner R-06.3 |
| Ö-Ø12 | Ø12 | rak | – | 27 | var. | 26 | 23 | zoner R-06.3 |
| | | | | | | Summa | 2 539 | Ø8: 888 + Ø10: 1 627 + Ø12: 23 |

Näten räknade över hela plattan (även plattan på mark) med en skarv per 12 m stång. Skarvlängd Ø8 500, Ø10 650, Ø12 750 mm.

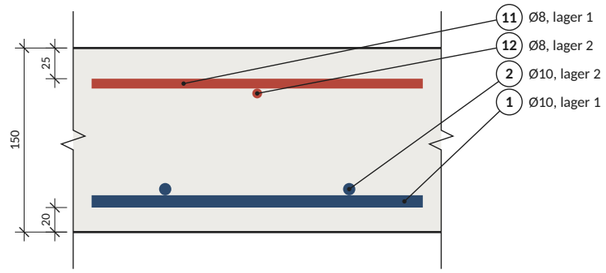


### DETALJ E  Armeringens lägen

Skala 1:5

| Rev | Avser | Datum | Sign |
|---|---|---|---|
| A | Första utgåvan | 2026-10-08 | VO |

PROJEKT

**Fritidshus Trebodar, Resö, Tanum**

FASTIGHET

Resö 2:66, Tanums kommun · BYGG.2025.2278

INNEHÅLL

**Mellanbjälklag**
**Sektioner, detaljer och stålförteckning**

| SKALA | FORMAT | DATUM |
|---|---|---|
| 1:5, 1:10, 1:20 | A3 | 2026-10-08 |
| UPPRÄTTAD | GRANSKAD | UNDERLAG |
| Viktor Ogeman | – | K-05 rev A, K-06 rev A |
| STATUS | | REVISION |
| **KONSTRUKTION** | | **A** |

RITNINGSNUMMER

**R-06.4**