


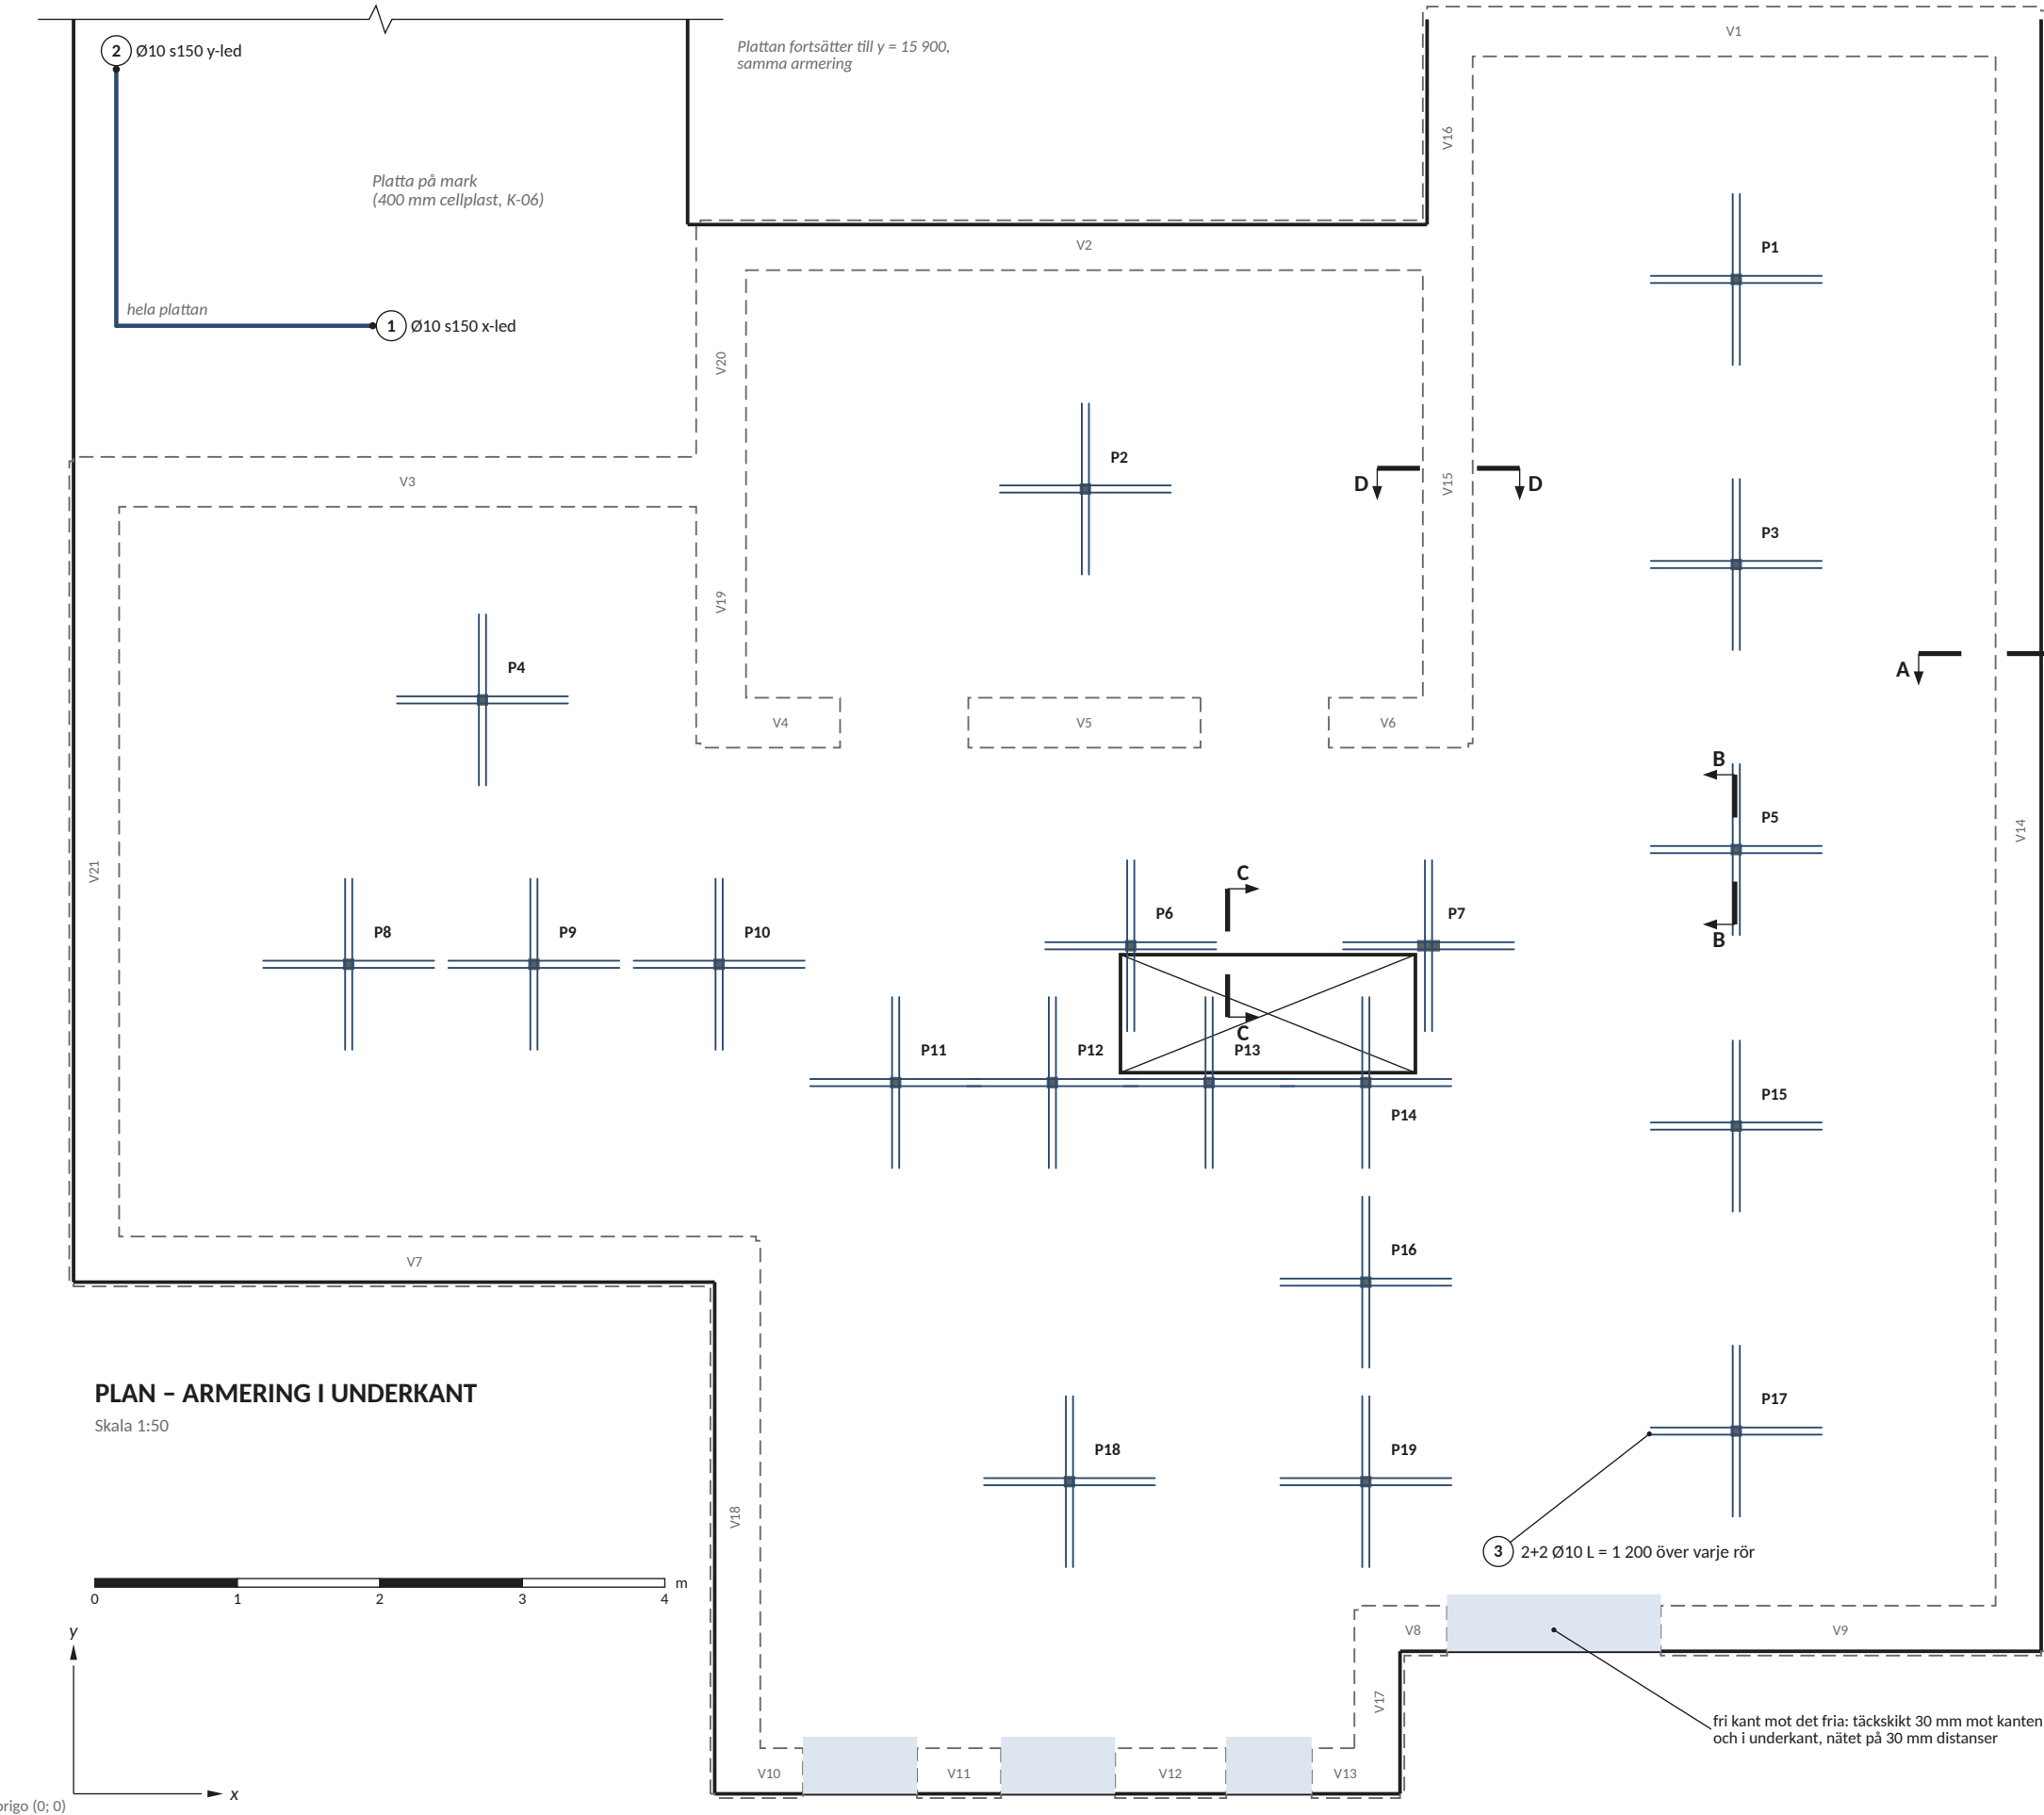



- Anvisningar**
- Betong C25/30, exponeringsklass XC3 (vct ≤ 0,55), livslängd 50 år. Armering B500B.
 - Täckskikt: underkant 20 mm, överkant 25 mm, kanter och hålkantar 25 mm. Vid öppningarna i källarens ytterväggar (kant mot det fria): 30 mm mot kanten och i underkant inom 400 mm från kanten, se R-03.2.
 - Skarvlängd: Ø8 500, Ø10 650, Ø12 750 mm. Skarvar förskjuts minst 1,3 x skarvlängden.
 - Järnen i varje nät läggs i valfri ordning. Tilläggsjärn läggs i nätets lager.
 - Koordinater i mm enligt K-05; origo i skärningen mellan plattkanterna x = 0 och y = 0. Mått, se R-03.1.
 - Underkantsnätet läggs på distanser 20 mm, högst 0,8 m isär, och 30 mm i de blå områdena vid öppningarna i källarens ytterväggar.
 - Minst två underkantsjärn i vardera riktningen ska passera över varje rör (SS-EN 1992-1-1 9.4.1(3)); pos 3, bundna till nätet.
 - Överkant, se R-03.3. Sektioner A–D, se R-03.4.


- Teckenförklaring**
- armering i underkant
 - fri kant mot det fria: täckskikt 30 mm
 - ① positionsnummer (stålförteckning R-03.4)
 - - - Lecavägg under plattan
 - stålrör VKR 80×80×4 (K-05)

Rör	x	y	Topplåt
P1	11 670	10 625	80×80×8
P2	7 102	9 155	80×80×8
P3	11 670	8 625	80×80×8
P4	2 870	7 675	80×80×8
P5	11 670	6 625	80×80×8
P6	7 420	5 950	80×80×8
P7	9 470 och 9 550	5 950	två rör tätt intill varandra, 80×80×8 på vart
P8	1 931	5 820	80×80×8
P9	3 231	5 820	80×80×8
P10	4 531	5 820	80×80×8
P11	5 770	4 990	80×80×8
P12	6 870	4 990	80×80×8
P13	7 970	4 990	80×80×8
P14	9 070	4 990	80×80×8
P15	11 670	4 685	80×80×8
P16	9 070	3 590	80×80×8
P17	11 670	2 545	80×80×8
P18	6 990	2 190	80×80×8
P19	9 070	2 190	80×80×8

Rev	Avser	Datum	Sign
A	Första utgåvan	2026-10-08	VO


PROJEKT
Fritidshus Trebodar, Resö, Tanum
FASTIGHET
Resö 2:66, Tanums kommun · BYGG.2025.2278
INNEHÅLL

Mellanbjälklag Armering i underkant		
SKALA	FORMAT	DATUM
1:50	A3	2026-10-08
UPPRÄTTAD	GRANSKAD	UNDERLAG
Viktor Ogeman	–	K-05 rev A, K-06
STATUS		REVISION
FÖR GRANSKNING		A
RITNINGNUMMER		

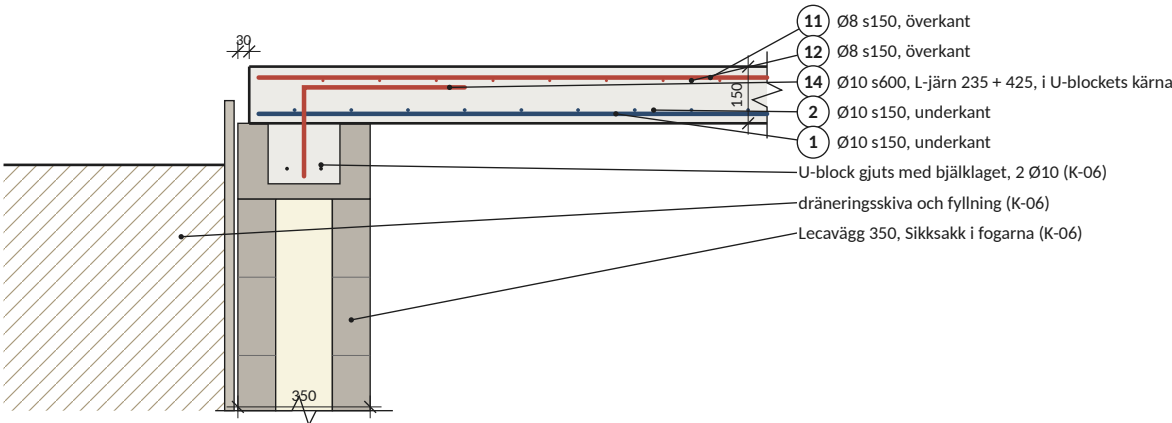


SEKTION A-A Yttervägg mot jord (V14)

Skala 1:20

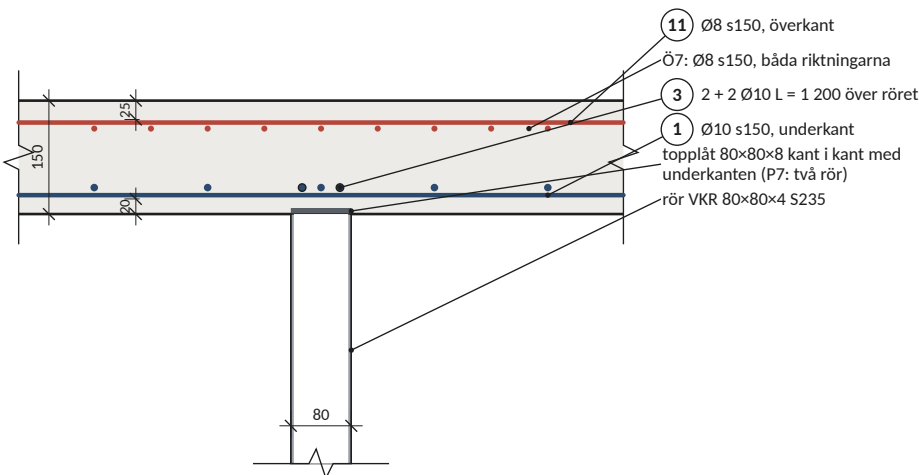


SEKTION B-B Vid rör (P5)

Skala 1:10

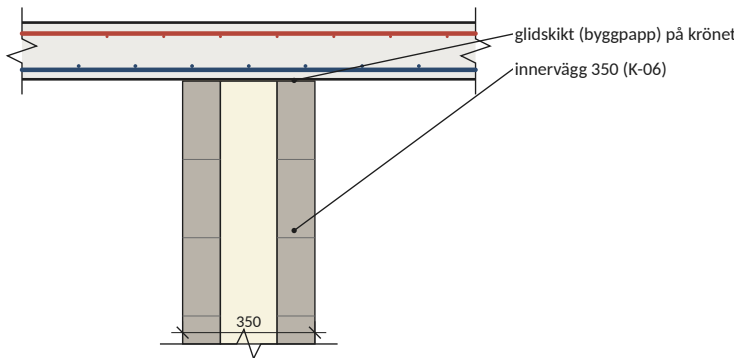


SEKTION D-D Innervägg (V15)

Skala 1:20

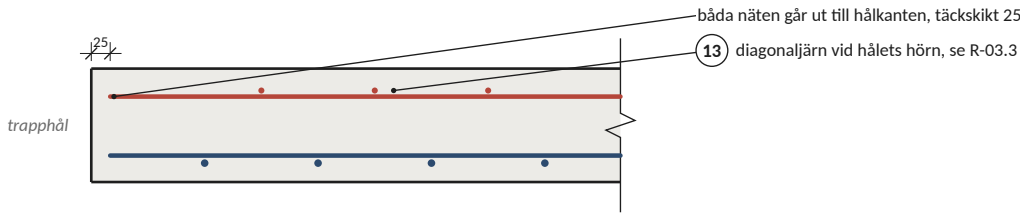

SEKTION C-C Trapphålets kant

Skala 1:10

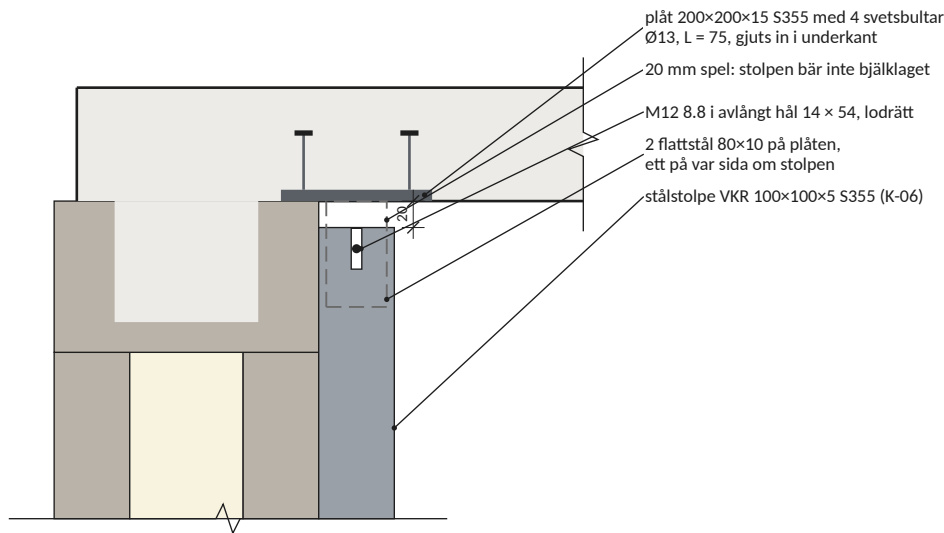


DETALJ E Stålstolpens topp, system A (K-06)

Skala 1:10

Stålförteckning, B500B

Pos	Ø	Form	s	Antal	L (mm)	Total (m)	Vikt (kg)	Anm
1	Ø10	rak	s150	122	var.	1 063	656	UK x-led
2	Ø10	rak	s150	106	var.	1 057	652	UK y-led
11	Ø8	rak	s150	122	var.	1 057	417	ÖK x-led
12	Ø8	rak	s150	106	var.	1 053	416	ÖK y-led
3	Ø10	rak	-	76	1 200	91	56	UK över rören
13	Ø10	rak	-	16	1 200	19	12	ÖK diagonalt
14	Ø10	L 235+425	s600	86	660	57	35	U-block
Ö-Ø8	Ø8	rak	-	152	var.	171	68	zoner R-03.3
Ö-Ø10	Ø10	rak	-	71	var.	86	53	zoner R-03.3
Ö-Ø12	Ø12	rak	-	66	var.	79	71	zoner R-03.3
Summa							2 436	Ø8: 901 + Ø10: 1 465 + Ø12: 71

Näten raknade över hela plattan (även plattan på mark) med en skarv per 12 m stång. Skarvslängd Ø8 500, Ø10 650, Ø12 750 mm.

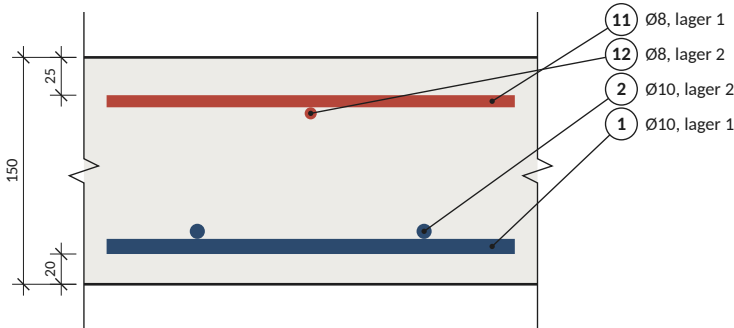

DETALJ F Armeringens lägen

Skala 1:5

Anvisningar

- Betong C25/30, exponeringsklass XC3 (vct ≤ 0,55), livslängd 50 år. Armering B500B.
- Täckskikt: underkant 20 mm, överkant 25 mm, kanter och hållkanter 25 mm. Vid öppningarna i källarens ytterväggar (kant mot det fria): 30 mm mot kanten och i underkant inom 400 mm från kanten, se R-03.2.
- Skarvlängd: Ø8 500, Ø10 650, Ø12 750 mm. Skarvar förskjuts minst 1,3 x skarvlängden.
- Järnen i varje nät läggs i valfri ordning. Tilläggsjärn läggs i nätets lager.
- Rörens topplåt gjuts in kant i kant med plattans underkant. Röret centreras under plåten. Rörens lägen ±40 mm enligt tabellen på R-03.2; P7 är två rör tätt intill varandra.
- Överkantsarmeringens höjd kontrolleras före gjutning, särskilt vid rören.
- U-blocket i ytterväggarna gjuts samtidigt med bjälklaget. Pos 14 sätts i U-blocket före gjutning.
- Innerväggarna får glidskikt (byggpapp) på krönet.
- Formrivning tidigast när betongen nått cirka 70 % av fck (provkroppar eller mognadsberäkning). Last under byggtiden högst 5 kN/m², punktlaster över rör eller vägg.
- Trägolvlimmas först när betongens relativa fuktighet är under golvlimmets gräns (mätt enligt RBK). Våtrum får sprickupptagande tätskikt.
- 11.Detailj E gäller stål stolparna i system A (K-06): V14 och V21.
- 12.Plan: underkant R-03.2, överkant R-03.3.

Teckenförklaring

- armering i underkant
- armering i överkant
- betong C25/30
- Leca (lättklinker)
- isolering
- fyllning
- stål

Rev	Avser	Datum	Sign
A	Första utgåvan	2026-10-08	VO

PROJEKT

Fritidshus Trebodar, Resö, Tanum

FASTIGHET

Resö 2:66, Tanums kommun · BYGG.2025.2278

INNEHÅLL

Mellanbjälklag Sektioner, detaljer och stålförteckning

SKALA	FORMAT	DATUM
1:5, 1:10, 1:20	A3	2026-10-08
UPPRÄTTAD	GRANSKAD	UNDERLAG
Viktor Ogeman	–	K-05 rev A, K-06
STATUS		REVISION
FÖR GRANSKNING		A
RITNINGNUMMER		

R-03.4