
## Plan, utsättningspunkter

Skala 1:100

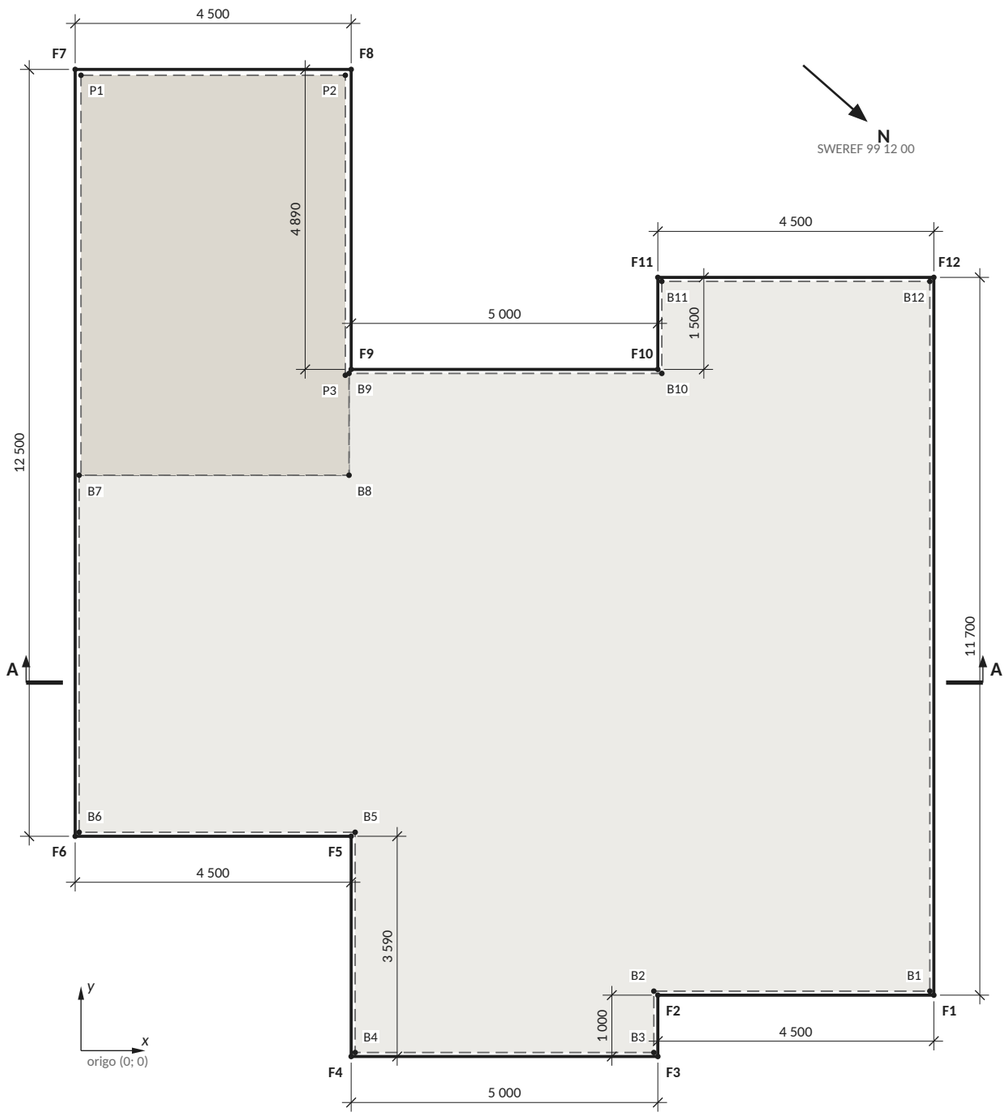


## Utsättningspunkter, SWEREF 99 12 00

x, y i mm (K-05), N, E och höjder i m. Höjder i RH2000 och relativt fixpunkten FIX (+7,760).

### Fasadens utsida (F)

| Punkt | x | y | N | E |
|---|---|---|---|---|
| F1 | 13 905 | 905 | 6 520 175,041 | 102 362,162 |
| F2 | 9 405 | 905 | 6 520 171,660 | 102 365,132 |
| F3 | 9 405 | −95 | 6 520 172,320 | 102 365,883 |
| F4 | 4 405 | −95 | 6 520 168,563 | 102 369,183 |
| F5 | 4 405 | 3 495 | 6 520 166,194 | 102 366,485 |
| F6 | −95 | 3 495 | 6 520 162,813 | 102 369,455 |
| F7 | −95 | 15 995 | 6 520 154,564 | 102 360,062 |
| F8 | 4 405 | 15 995 | 6 520 157,945 | 102 357,093 |
| F9 | 4 405 | 11 105 | 6 520 161,172 | 102 360,767 |
| F10 | 9 405 | 11 105 | 6 520 164,929 | 102 357,468 |
| F11 | 9 405 | 12 605 | 6 520 163,939 | 102 356,341 |
| F12 | 13 905 | 12 605 | 6 520 167,321 | 102 353,371 |

### Bottenplattans kant (B), L-elementens ytterkant, ök +6,250 (FIX −1,510)

| Punkt | x | y | N | E |
|---|---|---|---|---|
| B1 | 13 840 | 970 | 6 520 174,949 | 102 362,156 |
| B2 | 9 340 | 970 | 6 520 171,568 | 102 365,126 |
| B3 | 9 340 | −30 | 6 520 172,228 | 102 365,877 |
| B4 | 4 470 | −30 | 6 520 168,569 | 102 369,091 |
| B5 | 4 470 | 3 560 | 6 520 166,200 | 102 366,393 |
| B6 | −30 | 3 560 | 6 520 162,819 | 102 369,363 |
| B7 | −30 | 9 380 | 6 520 158,978 | 102 364,990 |
| B8 | 4 370 | 9 380 | 6 520 162,284 | 102 362,086 |
| B9 | 4 370 | 11 040 | 6 520 161,189 | 102 360,839 |
| B10 | 9 470 | 11 040 | 6 520 165,021 | 102 357,474 |
| B11 | 9 470 | 12 540 | 6 520 164,031 | 102 356,347 |
| B12 | 13 840 | 12 540 | 6 520 167,314 | 102 353,463 |

### Plattan på marks kant (P), ök +8,500 (FIX +0,740)


| Punkt | x | y | N | E |
|---|---|---|---|---|
| P1 | 0 | 15 900 | 6 520 154,698 | 102 360,071 |
| P2 | 4 310 | 15 900 | 6 520 157,937 | 102 357,227 |
| P3 | 4 310 | 11 010 | 6 520 161,164 | 102 360,901 |

### Fixpunkt FIX, +7,760

| Punkt | x | y | N | E |
|---|---|---|---|---|
| FIX | 16 628,8 | 42 302,7 | 6 520 149,770 | 102 329,260 |

## Översikt, fixpunkt

Skala 1:500

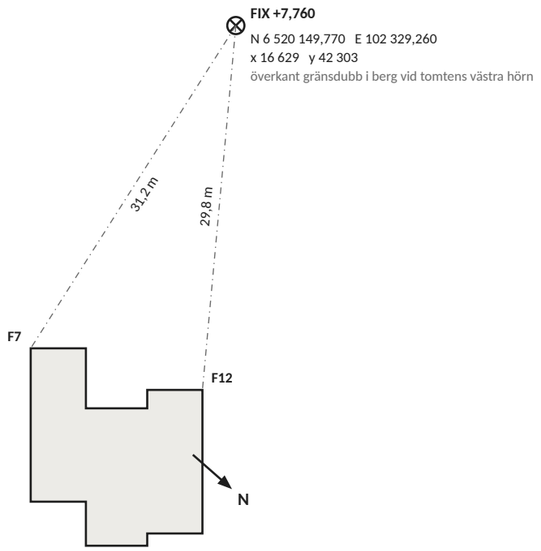


## Anvisningar

1. Koordinater i SWEREF 99 12 00 (Tanums kommun), höjder i RH2000 (AR-02.2). Mått i mm. x, y är husets koordinater, samma som i K-05 och på R-03–R-06: origo i skärningen mellan mellanbjälklagets kanter x = 0 och y = 0.
2. Utstakning och lägeskontroll görs av certifierad mättekniker (krav i bygglovet BYGG.2025.2278).
3. Höjdreferens: fixpunkten FIX, byggfixen på nybyggnadskartan (2025-11-12): överkant gränsdubb i berg vid tomtens västra hörn, +7,760. Alla höjder anges i RH2000 och relativt dubben. Dubbens läge är angivet i cm.
4. Fasadens hörn F1–F12 är utsättningsdata. Bottenplattans (B) och plattan på marks (P) punkter är beräknade med samma läge:
5. E = E0 + (x cos θ − y sin θ)/1 000, N = N0 + (x sin θ + y cos θ)/1 000, med θ = 131,290900°, E0 = 102 372,0179, N0 = 6 520 165,1905.
6. Plattan på mark (P, tillbyggnaden) har sin kant i mellanbjälklagets kant, 95 mm innanför fasaden. Den ansluter till källarväggarna mot B7–B9.

## Teckenförklaring

- fasadens utsida (F)
- bottenplattan (B), L-elementens ytterkant
- plattan på mark (P)
- utsättningspunkt

| Rev | Avser | Datum | Sign |
|---|---|---|---|
| A | Första utgåvan | 2026-10-31 | VO |

PROJEKT

**Fritidshus Trebodar, Resö, Tanum**

FASTIGHET

Resö 2:66, Tanums kommun · BYGG.2025.2278

INNEHÅLL

**Utsättning**
**Plan och koordinater**


| SKALA | FORMAT | DATUM |
|---|---|---|
| 1:100, 1:500 | A3 | 2026-10-31 |
| UPPRÄTTAD | GRANSKAD | UNDERLAG |
| Viktor Ogeman | – | Bygglov, NBK, K-05, R-05 |
| STATUS | | REVISION |
| **KONSTRUKTION** | | **A** |

RITNINGSNUMMER

**AR-02.1**

## Sektion A–A, y = 6 000 (princip)

Skala 1:50

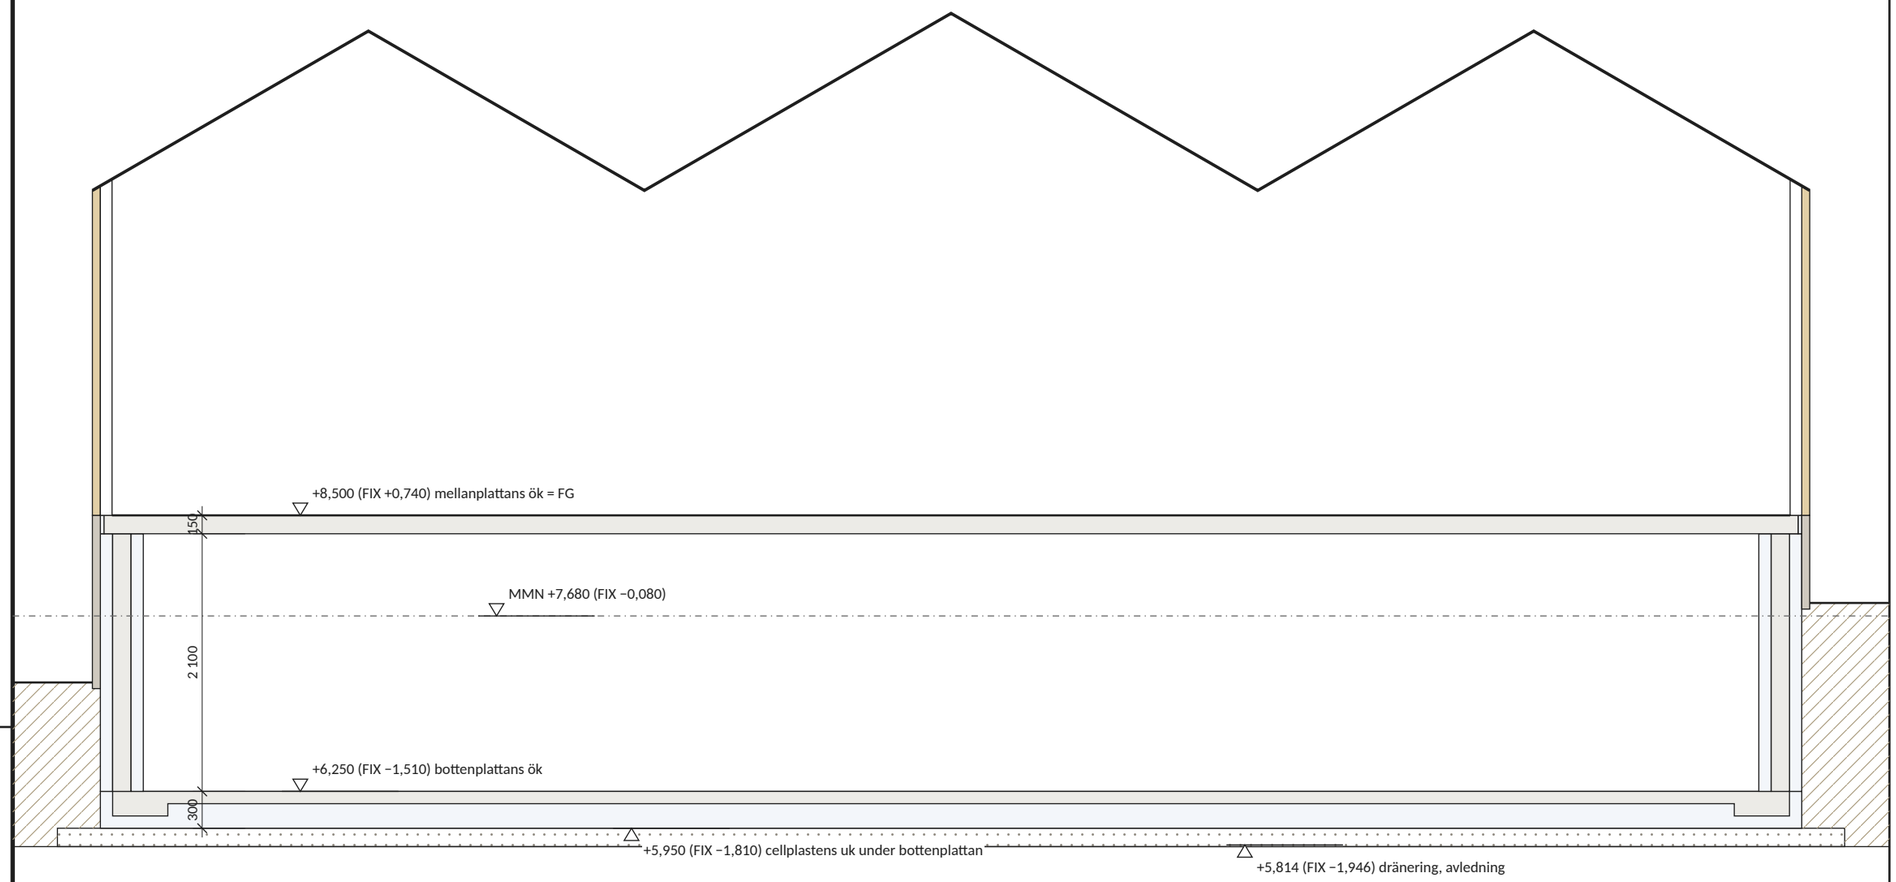


### Höjder, RH2000

| Nivå | RH2000 (m) | Relativt FIX (m) | Underlag |
|---|---|---|---|
| Mellanplattans överkant = FG, färdigt golv plan 1 | +8,500 | +0,740 | bygglov; betonggolv |
| Fixpunkt FIX, överkant gränsdubb i berg vid tomtens västra hörn | +7,760 | ±0 | nybyggnadskartan 2025-11-12 (byggfix) |
| MMN, medelmarknivå | +7,680 | −0,080 | bygglov |
| Bottenplattans överkant | +6,250 | −1,510 | mellanplattans ök − 150 − 2 100 (K-05, K-06) |
| Cellplastens underkant under bottenplattan | +5,950 | −1,810 | − platta 100 − cellplast 200 (R-04) |
| Dränering, tillgänglig nivå för avledning | +5,814 | −1,946 | – |

### Anvisningar

1. Höjder i RH2000 och relativt fixpunkten FIX (+7,760, gränsdubb i berg, se AR-02.1), i m. Mått i mm. Sektionen är en principskiss. Snittets läge: AR-02.1.
2. FG +8,500 är mellanplattans överkant.
3. Bottenplattans cellplast läggs på avjämnad makadam (R-04).

### Teckenförklaring

- takplanets ovansida
- MMN
- betong
- cellplast
- fasadsten (AR-01)
- beklädnad, plan 1
- makadam
- mark

| Rev | Avser | Datum | Sign |
|---|---|---|---|
| A | Första utgåvan | 2026-10-31 | VO |

PROJEKT

**Fritidshus Trebodar, Resö, Tanum**

FASTIGHET

Resö 2:66, Tanums kommun · BYGG.2025.2278

INNEHÅLL

**Utsättning**
**Sektion och höjder**

| SKALA | FORMAT | DATUM |
|---|---|---|
| 1:50 | A3 | 2026-10-31 |

| UPPRÄTTAD | GRANSKAD | UNDERLAG |
|---|---|---|
| Viktor Ogeman | – | Bygglov, NBK, K-05, R-05 |

| STATUS | REVISION |
|---|---|
| **KONSTRUKTION** | **A** |

RITNINGSNUMMER

# AR-02.2