Plan 1, golvet, belysningsstyrka

Skala 1:75



Belysningsstyrka, lux

5 000
2 000
1 000
750
500
300
200
150
100
75
50
20
10
0

Rum och delområden, lux

Rum	Medel	Min	Max	Jämnhet U_0
Allrum	217	100	334	0,46
Badrum	268	135	383	0,50
Bänken längs 3NV (0,91 m)	568	164	771	0,29
Bänken längs 3SV (0,91 m)	233	97	480	0,41
Gästrum	39	34	47	0,88
Gång	103	48	178	0,47
Hall	99	65	157	0,66
Kontor	165	87	262	0,53
Kontor, litet	42	33	53	0,79
Kök	235	20	460	0,09
Sovrum	34	13	69	0,39
Sovrum, litet	193	115	221	0,60
Trappa	139	102	165	0,73
Vardagsrum	236	123	343	0,52
Ön (0,91 m)	811	203	2 050	0,25

Anvisningar

1. Belysningsstyrkan på en vågrät yta 0,04 m över golvet, i rutor om 50 mm, ur renderingen i Blender (Cycles): armaturernas uppmätta ljusfördelning (tillverkarnas fotometrifiler), dagsljuset och reflexerna i rummen. Delområdena Bänken längs 3NV, Bänken längs 3SV och Ön mäts på en vågrät yta 0,91 m över golvet.
2. Tända: AL-T1 Allrum, tubspotar sydost; AL-T2 Allrum, tubspotar nordväst; AL-T3 Allrum, PH 5 över bordet; KO-T1 Kök, tubspotar mot taket; KO-T2 Kök, spotar mot bänken; KO-T3 Kök, Stav över ön; GA-T1 Gång, tubspotar; HA-T1 Hall, tubspotar; VR-T1 Vardagsrum, spotar sydost; VR-T2 Vardagsrum, spotar nordväst; VR-T3 Vardagsrum, VL45; BA-T1 Badrum, spotar; BA-T2 Badrum, lampan över tvättstället; SV-T1 Sovrum, glob; KT-T1 Kontor, spotar mot väggarna; SL-T1 Sovrum litet, spotar mot gaveln; SL-T2 Sovrum litet, spotar mot L1; KL-T1 Kontor litet, glob; GR-T1 Gästrum, glob; KA-T6 Källaren, det stora rummet; KA-T7 Källaren, det lilla rummet väster om KL2; KA-T8 Källaren, det lilla rummet öster om KL2; KA-T1 Källaren, trapphallen; KA-T2 Källaren, tvättstugan; KA-T3 Källaren, rummen norr om V4–V6, västra delen; KA-T4 Källaren, rummen norr om V4–V6, östra delen; KA-T5 Källaren, rummet söder om trapphallen.
3. Inget dagsljus (2026-12-21 kl. 22:00).
4. Statistiken per rum utan en kantzon på 0,5 m längs väggarna (SS-EN 12464-1), i små rum mindre, och utan inredningen på mätytan (skåp, säng, bänkskivor och källartrappan, vita på planen); jämnheten U_0 = minsta / medel. Rummen är de slutna ytorna mellan väggarna; en öppen planlösning delas mellan rummens namn.
5. Ritningen ritas med ./mod ljusplan (verktyg/modellering); mätytorna står i modellens el/matytor.py.

Teckenförklaring

- isolinje, med belysningsstyrkan
- rummets yta i statistiken (utan kantzonen)
- delområde med egen statistik
- armatur

Rev	Avser	Datum	Sign

PROJEKT

Fritidshus Trebodar, Resö, Tanum

FASTIGHET

Resö 2:66, Tanums kommun · BYGG.2025.2278

INNEHÅLL

Ljusplan
Plan 1, golvet


SKALA	FORMAT	DATUM
1:75	A3	2026-11-05
UPPRÄTTAD	GRANSKAD	UNDERLAG
Viktor Ogeman	–	Modellen, rendering
STATUS		REVISION
UTREDNING		**A**

RITNINGSNUMMER

U-04.1

Plan 1, bordshöjd 0,75 m, belysningsstyrka

Skala 1:75

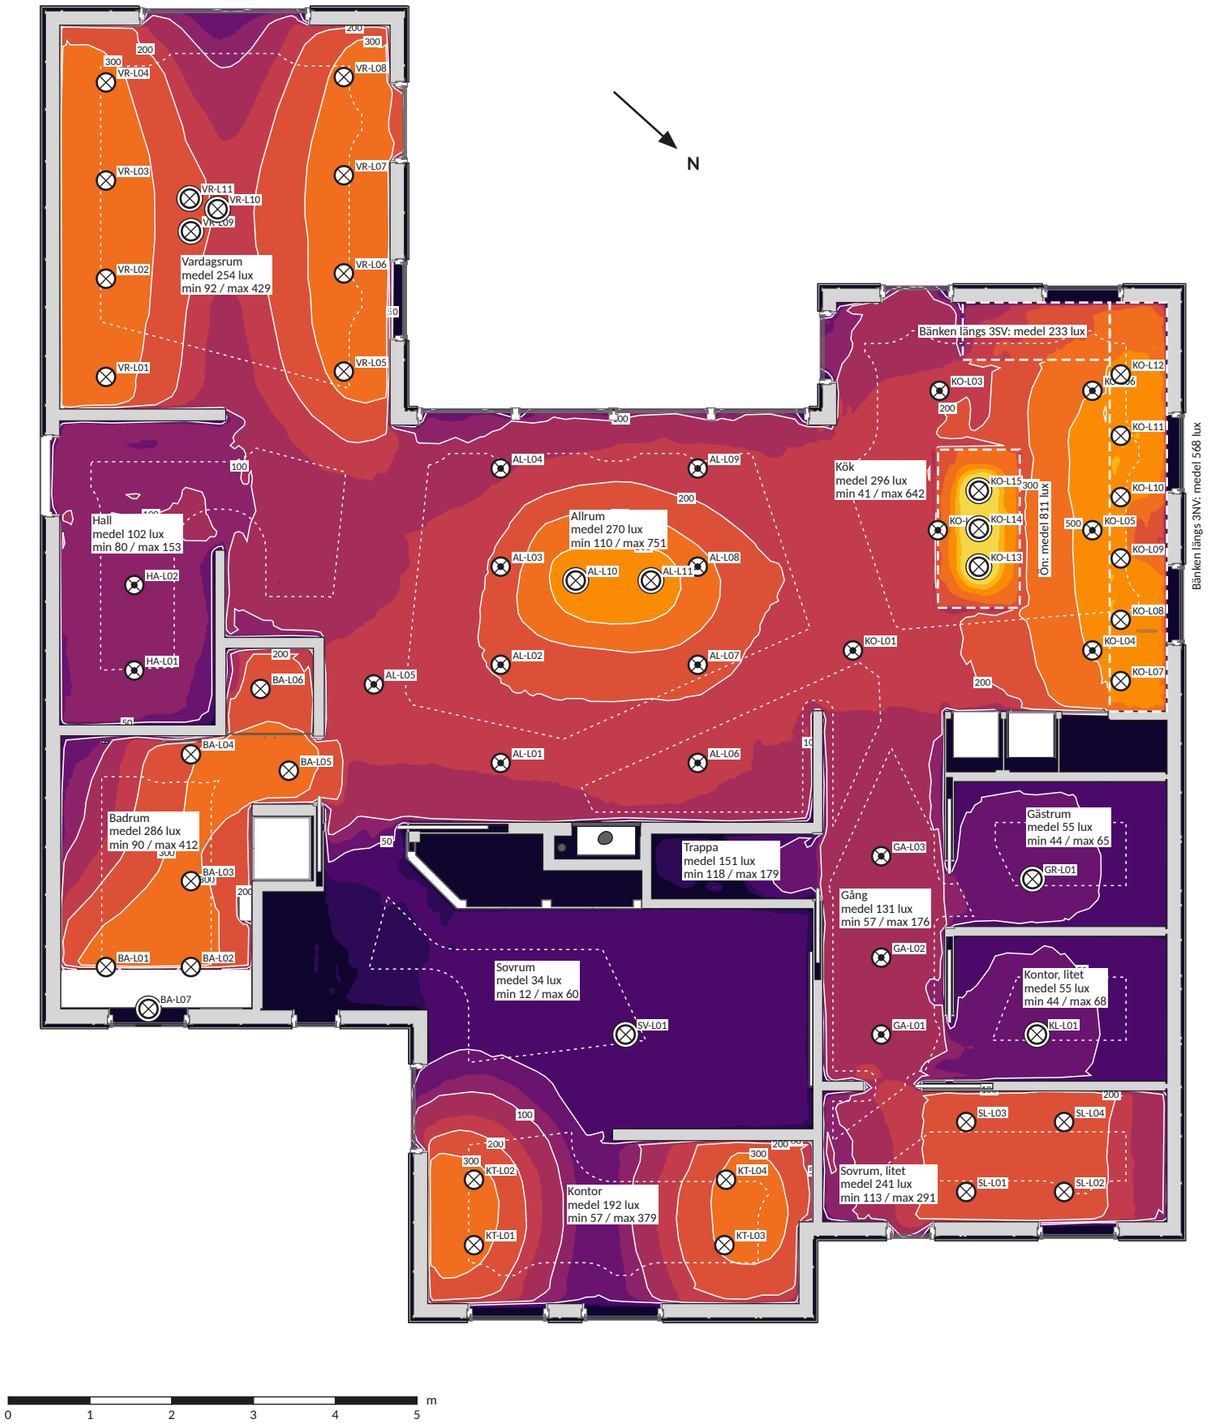

Belysningsstyrka, lux

5 000
2 000
1 000
750
500
300
200
150
100
75
50
20
10
0

Rum och delområden, lux

Rum	Medel	Min	Max	Jämnhet U_0
Allrum	270	110	751	0,41
Badrum	286	90	412	0,31
Bänken längs 3NV (0,91 m)	568	164	771	0,29
Bänken längs 3SV (0,91 m)	233	97	480	0,41
Gästrum	55	44	65	0,80
Gång	131	57	176	0,43
Hall	102	80	153	0,79
Kontor	192	57	379	0,30
Kontor, litet	55	44	68	0,81
Kök	296	41	642	0,14
Sovrum	34	12	60	0,36
Sovrum, litet	241	113	291	0,47
Trappa	151	118	179	0,78
Vardagsrum	254	92	429	0,36
Ön (0,91 m)	811	203	2 050	0,25

Anvisningar

1. Belysningsstyrkan på en vågrät yta 0,75 m över golvet, i rutor om 50 mm, ur renderingen i Blender (Cycles): armaturernas uppmätta ljusfördelning (tillverkarnas fotometrifiler), dagsljuset och reflexerna i rummen. Delområdena Bänken längs 3NV, Bänken längs 3SV och Ön mäts på en vågrät yta 0,91 m över golvet.
2. Tända: AL-T1 Allrum, tubspotar sydost; AL-T2 Allrum, tubspotar nordväst; AL-T3 Allrum, PH 5 över bordet; KO-T1 Kök, tubspotar mot taket; KO-T2 Kök, spotar mot bänken; KO-T3 Kök, Stav över ön; GA-T1 Gång, tubspotar; HA-T1 Hall, tubspotar; VR-T1 Vardagsrum, spotar sydost; VR-T2 Vardagsrum, spotar nordväst; VR-T3 Vardagsrum, VL45; BA-T1 Badrum, spotar; BA-T2 Badrum, lampan över tvättstället; SV-T1 Sovrum, glob; KT-T1 Kontor, spotar mot väggarna; SL-T1 Sovrum litet, spotar mot gaveln; SL-T2 Sovrum litet, spotar mot L1; KL-T1 Kontor litet, glob; GR-T1 Gästrum, glob; KA-T6 Källaren, det stora rummet; KA-T7 Källaren, det lilla rummet väster om KL2; KA-T8 Källaren, det lilla rummet öster om KL2; KA-T1 Källaren, trapphallen; KA-T2 Källaren, tvättstugan; KA-T3 Källaren, rummen norr om V4–V6, västra delen; KA-T4 Källaren, rummen norr om V4–V6, östra delen; KA-T5 Källaren, rummet söder om trapphallen.
3. Inget dagsljus (2026-12-21 kl. 22:00).
4. Statistiken per rum utan en kantzon på 0,5 m längs väggarna (SS-EN 12464-1), i små rum mindre, och utan inredningen på mätytan (skåp, säng, bänkskivor och källartrappan, vita på planen); jämnheten U_0 = minsta / medel. Rummen är de slutna ytorna mellan väggarna; en öppen planlösning delas mellan rummens namn.
5. Ritningen ritas med ./mod ljusplan (verktyg/modellering); mätytorna står i modellens el/matytor.py.

Teckenförklaring

- isolinje, med belysningsstyrkan
- rummets yta i statistiken (utan kantzonen)
- delområde med egen statistik
- armatur

Rev	Avser	Datum	Sign

PROJEKT

Fritidshus Trebodar, Resö, Tanum

FASTIGHET

Resö 2:66, Tanums kommun · BYGG.2025.2278

INNEHÅLL

Ljusplan
Plan 1, bordshöjd 0,75 m


SKALA	FORMAT	DATUM
1:75	A3	2026-11-05
UPPRÄTTAD	GRANSKAD	UNDERLAG
Viktor Ogeman	–	Modellen, rendering
STATUS		REVISION
UTREDNING		**A**

RITNINGSNUMMER

U-04.2

Köket, bänkskivorna 0,91 m, belysningsstyrka

Skala 1:50

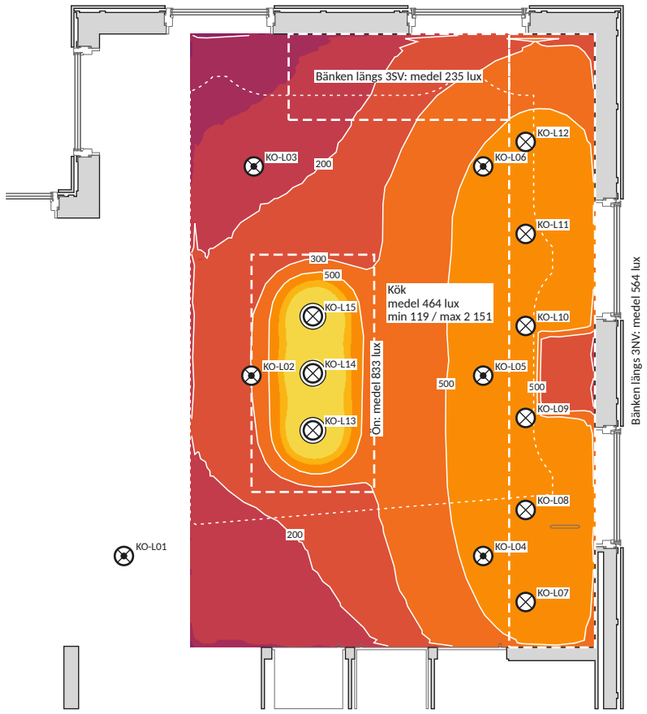

Belysningsstyrka, lux

5 000
2 000
1 000
750
500
300
200
150
100
75
50
20
10
0

Rum och delområden, lux

Rum	Medel	Min	Max	Jämnhet U_o
Bänken längs 3NV	564	147	750	0,26
Bänken längs 3SV	235	111	493	0,47
Kök	464	119	2 151	0,26
Ön	833	215	2 151	0,26

Anvisningar

1. Belysningsstyrkan på en vågrät yta 0,91 m över golvet, i rutor om 25 mm, ur renderingen i Blender (Cycles): armaturernas uppmätta ljusfördelning (tillverkarnas fotometrifiler), dagsljuset och reflexerna i rummen.
2. Tända: AL-T1 Allrum, tubspotar sydost; AL-T2 Allrum, tubspotar nordväst; AL-T3 Allrum, PH 5 över bordet; KO-T1 Kök, tubspotar mot taket; KO-T2 Kök, spotar mot bänken; KO-T3 Kök, Stav över ön; GA-T1 Gång, tubspotar; HA-T1 Hall, tubspotar; VR-T1 Vardagsrum, spotar sydost; VR-T2 Vardagsrum, spotar nordväst; VR-T3 Vardagsrum, VL45; BA-T1 Badrum, spotar; BA-T2 Badrum, lampan över tvättstället; SV-T1 Sovrum, glob; KT-T1 Kontor, spotar mot väggarna; SL-T1 Sovrum litet, spotar mot gaveln; SL-T2 Sovrum litet, spotar mot L1; KL-T1 Kontor litet, glob; GR-T1 Gästrum, glob; KA-T6 Källaren, det stora rummet; KA-T7 Källaren, det lilla rummet väster om KL2; KA-T8 Källaren, det lilla rummet öster om KL2; KA-T1 Källaren, trapphallen; KA-T2 Källaren, tvättstugan; KA-T3 Källaren, rummen norr om V4–V6, västra delen; KA-T4 Källaren, rummen norr om V4–V6, östra delen; KA-T5 Källaren, rummet söder om trapphallen.
3. Inget dagsljus (2026-12-21 kl. 22:00).
4. Statistiken per rum utan en kantzon på 0,5 m längs väggarna (SS-EN 12464-1), i små rum mindre, och utan inredningen på mätytan (skåp, säng, bänkskivor och källartrappan, vita på planen); jämnheten U_o = minsta / medel. Rummen är de slutna ytorna mellan väggarna; en öppen planlösning delas mellan rummens namn.
5. Ritningen ritas med ./mod ljusplan (verktyg/modellering); mätytorna står i modellens el/matytor.py.

Teckenförklaring

- isolinje, med belysningsstyrkan
- rummets yta i statistiken (utan kantzonen)
- delområde med egen statistik
- armatur

Rev	Avser	Datum	Sign

PROJEKT

Fritidshus Trebodar, Resö, Tanum

FASTIGHET

Resö 2:66, Tanums kommun · BYGG.2025.2278

INNEHÅLL

Ljusplan
Köket, bänkskivorna 0,91 m

SKALA	FORMAT	DATUM
1:50	A3	2026-11-05

UPPRÄTTAD	GRANSKAD	UNDERLAG
Viktor Ogeman	–	Modellen, rendering

STATUS	REVISION
UTREDNING	**A**

RITNINGSNUMMER

U-04.3

Källaren, golvet, belysningsstyrka

Skala 1:75



Belysningsstyrka, lux

5 000
2 000
1 000
750
500
300
200
150
100
75
50
20
10
0

Rum och delområden, lux

Rum	Medel	Min	Max	Jämnhet U_0
Rum söder om hallen	537	217	631	0,40
Rum söder om trapphallen	485	231	761	0,48
Rum öster om KL2	644	357	719	0,55
Rummen norr om V4–V6	558	186	735	0,33
Stora rummet	511	79	690	0,16
Teknikrum	66	0	355	0,00
Trapphall	646	201	883	0,31
Tvättstugan vid V3	558	179	740	0,32
Tvättstugan, hallen	541	258	739	0,48

Anvisningar

1. Belysningsstyrkan på golvet, i rutor om 50 mm, ur renderingen i Blender (Cycles): armaturernas uppmätta ljusfördelning (tillverkarnas fotometrifiler), dagsljuset och reflexerna i rummen.
2. Tända: AL-T1 Allrum, tubspotar sydost; AL-T2 Allrum, tubspotar nordväst; AL-T3 Allrum, PH 5 över bordet; KO-T1 Kök, tubspotar mot taket; KO-T2 Kök, spotar mot bänken; KO-T3 Kök, Stav över ön; GA-T1 Gång, tubspotar; HA-T1 Hall, tubspotar; VR-T1 Vardagsrum, spotar sydost; VR-T2 Vardagsrum, spotar nordväst; VR-T3 Vardagsrum, VL45; BA-T1 Badrum, spotar; BA-T2 Badrum, lampan över tvättstället; SV-T1 Sovrum, glob; KT-T1 Kontor, spotar mot väggarna; SL-T1 Sovrum litet, spotar mot gaveln; SL-T2 Sovrum litet, spotar mot L1; KL-T1 Kontor litet, glob; GR-T1 Gästrum, glob; KA-T6 Källaren, det stora rummet; KA-T7 Källaren, det lilla rummet väster om KL2; KA-T8 Källaren, det lilla rummet öster om KL2; KA-T1 Källaren, trapphallen; KA-T2 Källaren, tvättstugan; KA-T3 Källaren, rummen norr om V4–V6, västra delen; KA-T4 Källaren, rummen norr om V4–V6, östra delen; KA-T5 Källaren, rummet söder om trapphallen.
3. Inget dagsljus (2026-12-21 kl. 22:00).
4. Statistiken per rum utan en kantzon på 0,5 m längs väggarna (SS-EN 12464-1), i små rum mindre, och utan inredningen på mätytan (skåp, säng, bänkskivor och källartrappan, vita på planen); jämnheten U_0 = minsta / medel. Rummen är de slutna ytorna mellan väggarna; en öppen planlösning delas mellan rummens namn.
5. Ritningen ritas med ./mod ljusplan (verktyg/modellering); mätytorna står i modellens el/matytor.py.

Teckenförklaring

- isolinje, med belysningsstyrkan
- rummets yta i statistiken (utan kantzonen)
- delområde med egen statistik
- armatur

Rev	Avser	Datum	Sign

PROJEKT

Fritidshus Trebodar, Resö, Tanum

FASTIGHET

Resö 2:66, Tanums kommun · BYGG.2025.2278

INNEHÅLL

Ljusplan
Källaren, golvet

SKALA	FORMAT	DATUM
1:75	A3	2026-11-05

UPPRÄTTAD	GRANSKAD	UNDERLAG
Viktor Ogeman	–	Modellen, rendering

STATUS	REVISION
UTREDNING	**A**

RITNINGSNUMMER

U-04.4