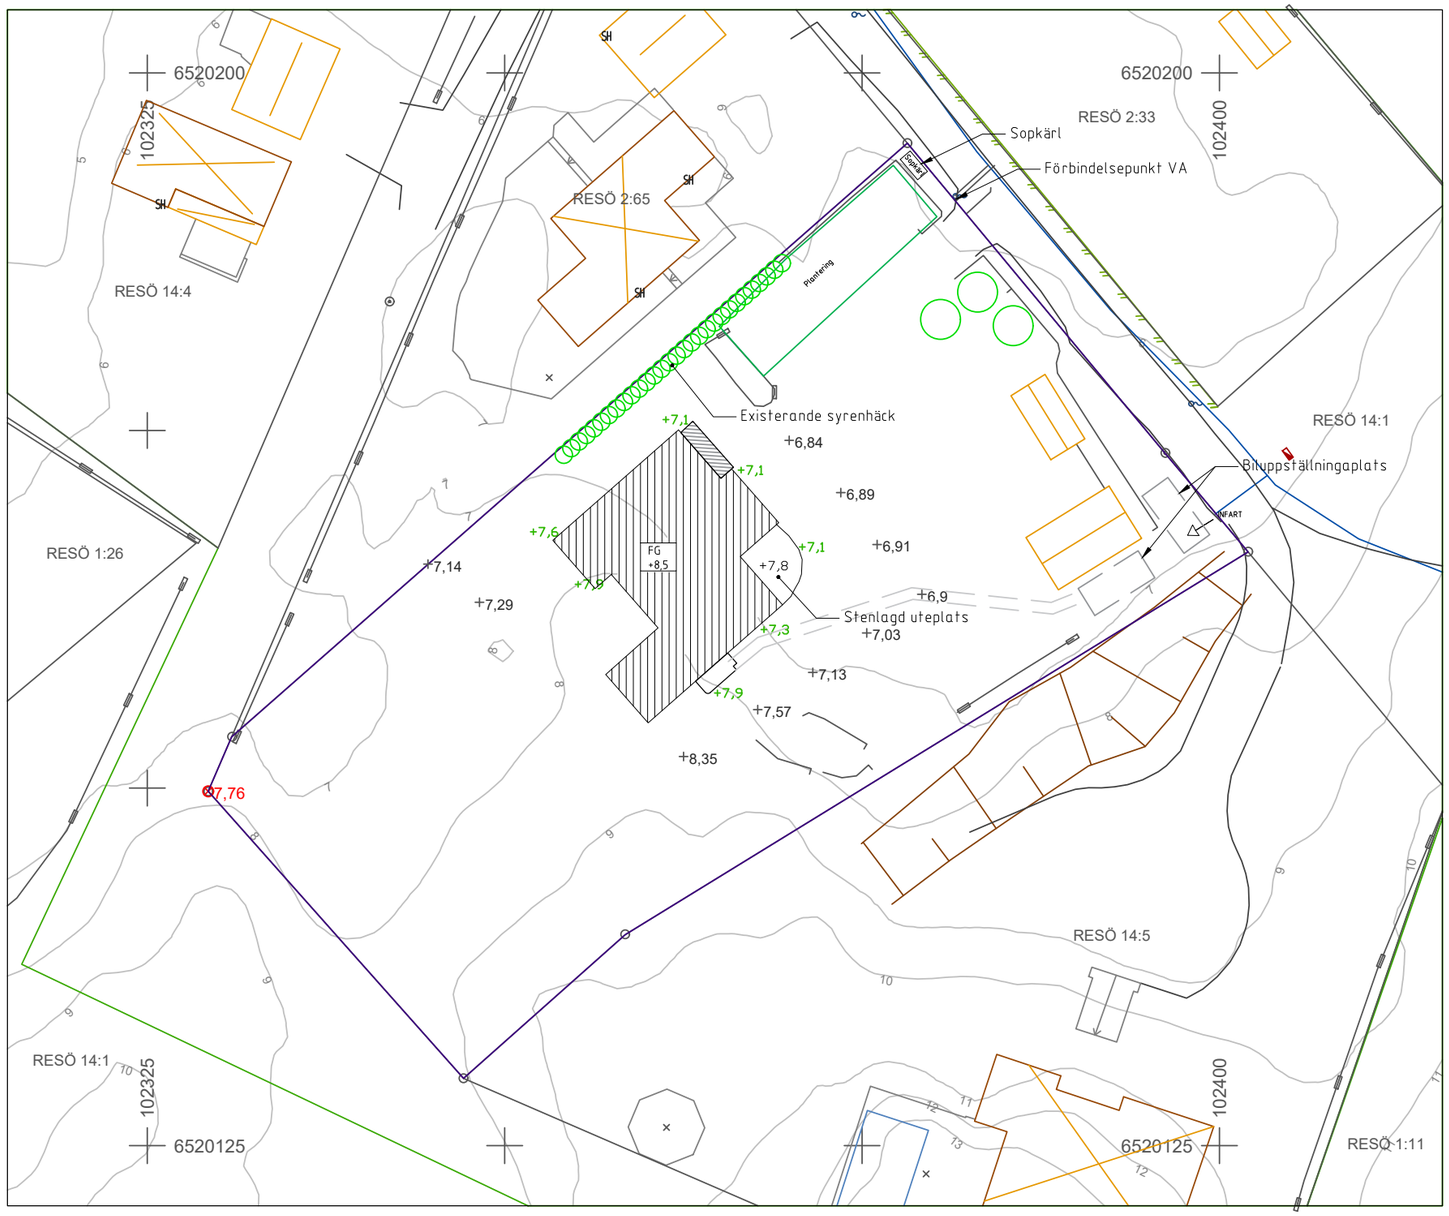


FÖRKLARINGAR
Alla mått anges i meter

Koordinatsystem Sweref 99 12 00
Höjdsystem RH2000

FG	Färdigt golv
+X.XX	Inmätt punkt nygyggnadskarta
+X.X	Ny markhöjd lokalt vid huset

Dagvatten kopplas på befintlig anslutning till kommunalt system.

Ny marknivå lutar 1:10 lokalt bort från huset.

NORR

0m 10m 20m 30m 40m 50m

BYGGLOV

Ogeman
Skogsåsen 16a
1412 Sofiemyr
Norge
Tel: +47 91 91 13 06

Tanum, Resö 2:66

Mariavägen 11b, Resö

Bygglov Fritidshus Trebodar

Markplan

DATUM	SKALA	RITNINGSNUMMER	REV
2025-12-01	1:400	203	00

Dokument tillhör beslut D32 Ordförande Hans Schub ,2026-02-18, BYGG.2025.2278