

Dokument tillhör beslut D32 Ordförande Hans Schub ,2026-02-18, BYGG.2025.2278

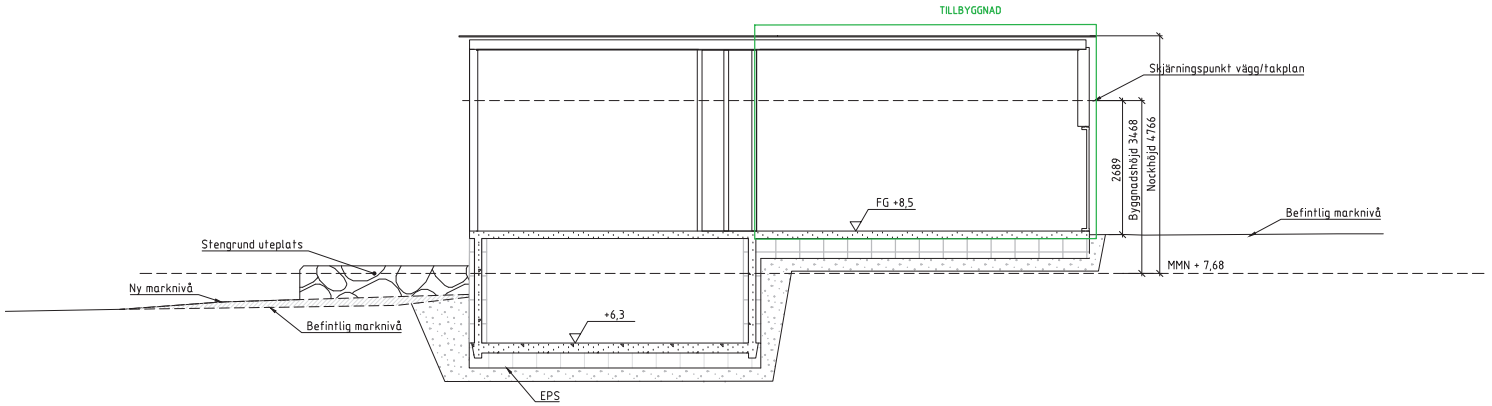

C-C

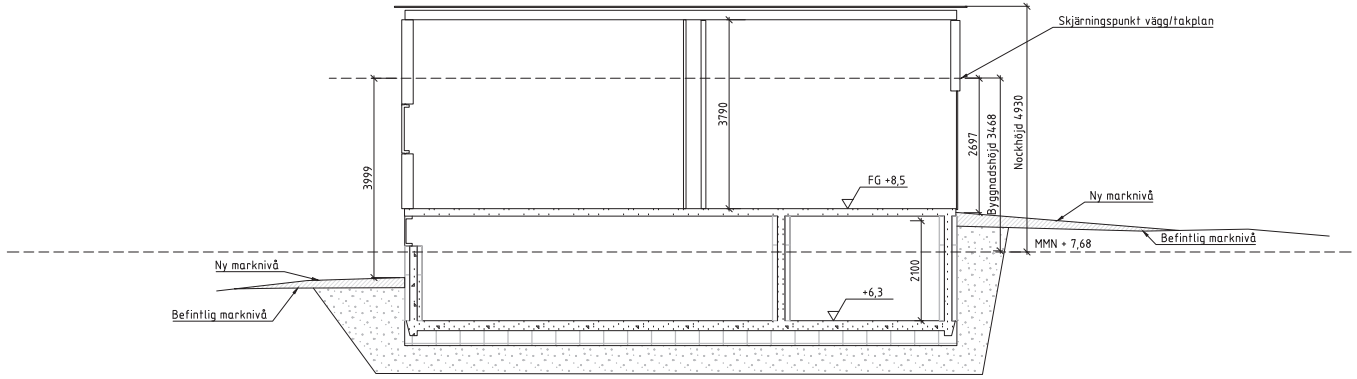

D-D

FÖRKLARING

	Markuppfyllnad
	Betong
	Makadam
	EPS
TG	Tomtgräns

BYGGLOV

Ogeman
Skogsåsen 16a
1412 Sofiemyr
Norge
Tel: +47 91 91 13 06

Tanum, Resö 2:66

Mariavägen 11b, Resö

Bygglov Fritidshus Trebodar

Sektion C och D

DATUM	SKALA	RITNINGSNUMMER	REV
2025-12-18	1:100	207	01

Ankom: 2025-12-18 Ärende: BYGG.2025.2278 Handling: 1487305