
Plan 1, golvet, belysningsstyrka

Skala 1:75

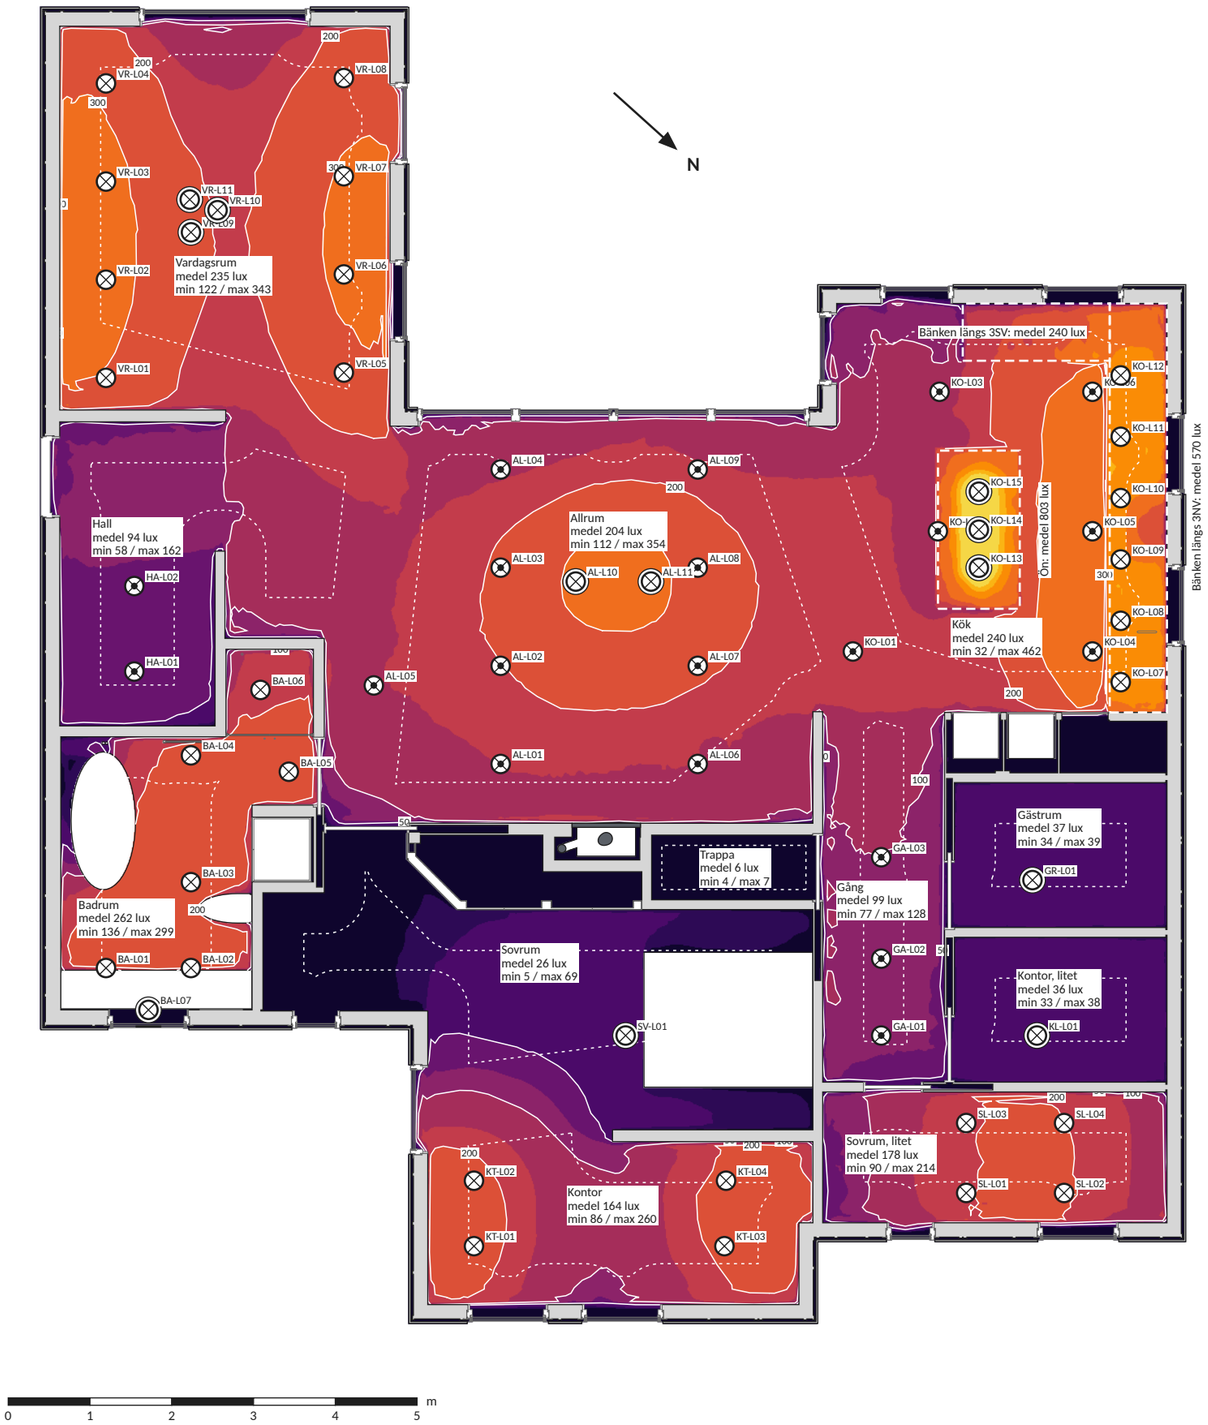

Belysningsstyrka, lux

5 000
2 000
1 000
750
500
300
200
150
100
75
50
20
10
0

Rum och delområden, lux

Rum	Medel	Min	Max	Jämnhet U_o
Allrum	204	112	354	0,55
Badrum	262	136	299	0,52
Bänken längs 3NV (0,91 m)	570	170	779	0,30
Bänken längs 3SV (0,91 m)	240	107	522	0,45
Gästrum	37	34	39	0,91
Gång	99	77	128	0,78
Hall	94	58	162	0,62
Kontor	164	86	260	0,52
Kontor, litet	36	33	38	0,89
Kök	240	32	462	0,13
Sovrum	26	5	69	0,20
Sovrum, litet	178	90	214	0,51
Trappa	6	4	7	0,74
Vardagsrum	235	122	343	0,52
Ön (0,91 m)	803	180	2 034	0,22

Anvisningar

1. Belysningsstyrkan på en vågrät yta 0,04 m över golvet, i rutor om 50 mm, ur renderingen i Blender (Cycles): armaturernas uppmätta ljusfördelning (tillverkarnas fotometrifiler), dagsljuset och reflexerna i rummen. Delområdena Bänken längs 3NV, Bänken längs 3SV och Ön mäts på en vågrät yta 0,91 m över golvet.
2. Tända: AL-T1 Allrum, tubspotar sydost; AL-T2 Allrum, tubspotar nordväst; AL-T3 Allrum, PH 5 över bordet; KO-T1 Kök, tubspotar mot taket; KO-T2 Kök, spotar mot bänken; KO-T3 Kök, Stav över ön; GA-T1 Gång, tubspotar; HA-T1 Hall, tubspotar; VR-T1 Vardagsrum, spotar sydost; VR-T2 Vardagsrum, spotar nordväst; VR-T3 Vardagsrum, VL45; BA-T1 Badrum, spotar; BA-T2 Badrum, lampan över tvättstället; SV-T1 Sovrum, glob; KT-T1 Kontor, spotar mot väggarna; SL-T1 Sovrum litet, spotar mot gaveln; SL-T2 Sovrum litet, spotar mot L1; KL-T1 Kontor litet, glob; GR-T1 Gästrum, glob; taklamporna kallare (16 LED-paneler 600 × 600 mm, 2 500 lm och 3 000 K).
3. Inget dagsljus (2026-12-21 kl. 22:00).
4. Statistiken per rum utan en kantzon på 0,5 m längs väggarna (SS-EN 12464-1), i små rum mindre, och utan inredningen på mätytan (skåp, säng och bänkskivor, vita på planen); jämnheten U_o = minsta / medel. Rummen är de slutna ytorna mellan väggarna; en öppen planlösning delas mellan rummens namn.
5. Ritningen ritas med ./mod ljusplan (verktyg/modellering); mätytorna står i modellens el/matytor.py.

Teckenförklaring

- isolinje, med belysningsstyrkan
- rummets yta i statistiken (utan kantzonen)
- delområde med egen statistik
- armatur

Rev	Avser	Datum	Sign

PROJEKT

Fritidshus Trebodar, Resö, Tanum

FASTIGHET

Resö 2:66, Tanums kommun · BYGG.2025.2278

INNEHÅLL

Ljusplan
Plan 1, golvet


SKALA	FORMAT	DATUM
1:75	A3	2026-11-05
UPPRÄTTAD	GRANSKAD	UNDERLAG
Viktor Ogeman	–	Modellen, rendering
STATUS		REVISION
UTREDNING		**A**

RITNINGSNUMMER

U-04.1

Plan 1, bordshöjd 0,75 m, belysningsstyrka

Skala 1:75

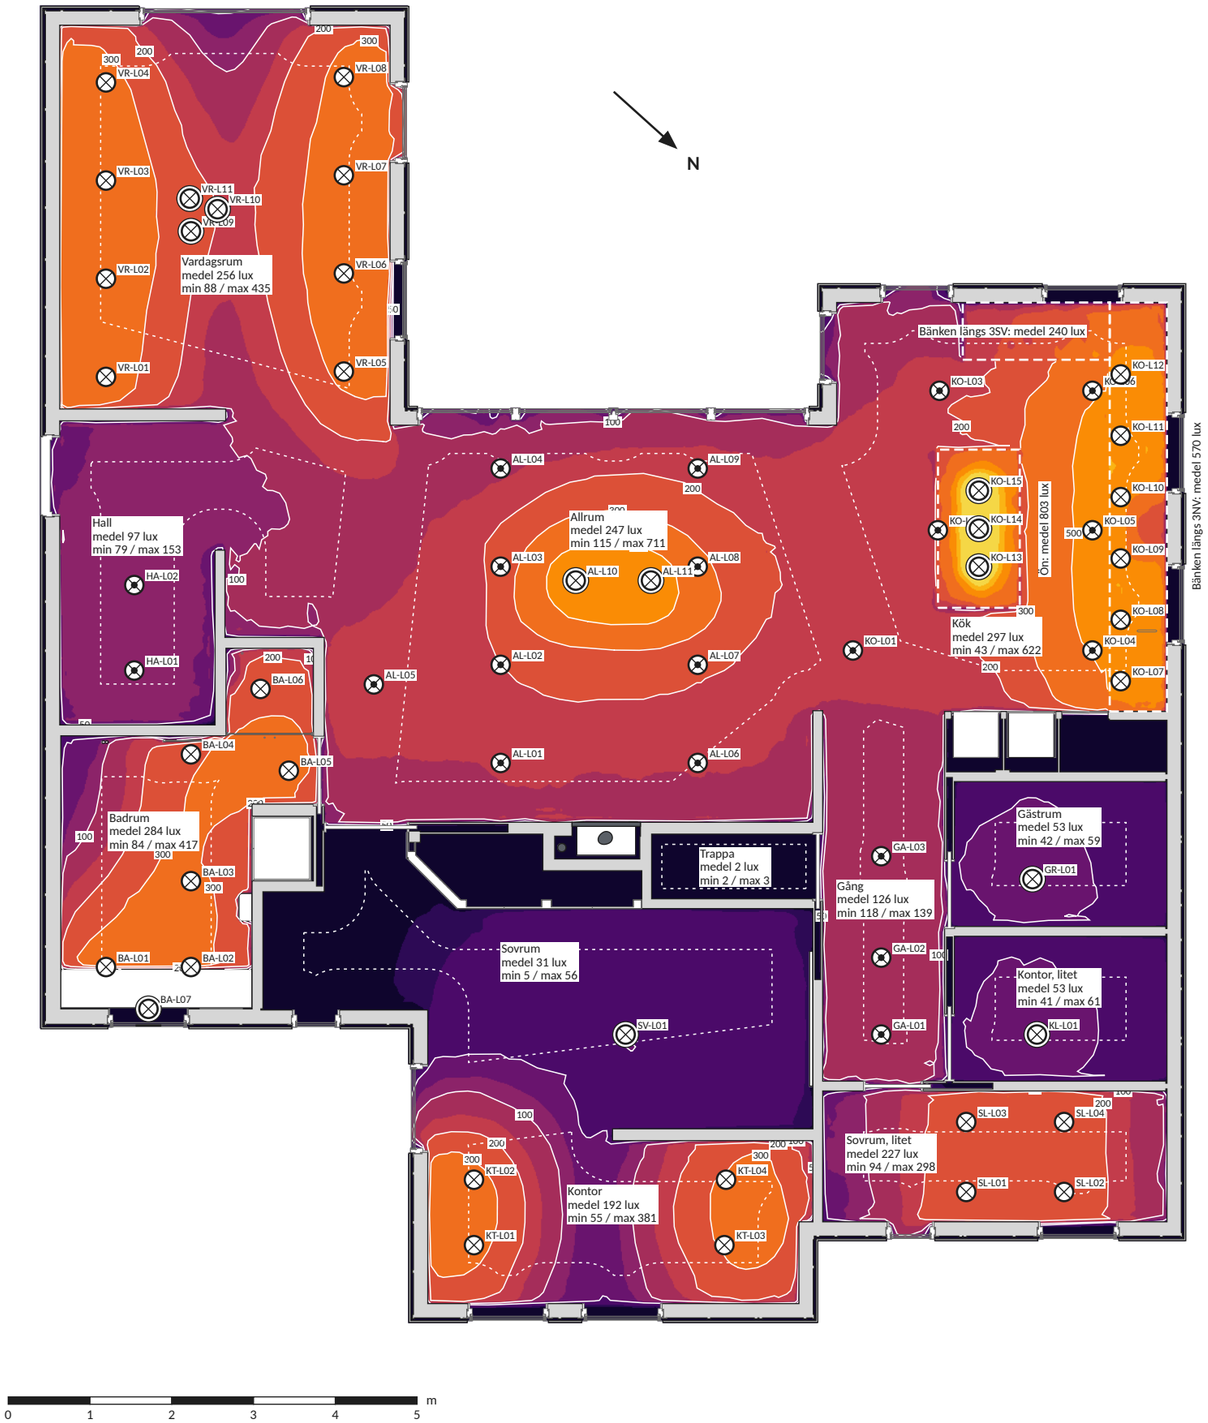

Belysningsstyrka, lux

5 000
2 000
1 000
750
500
300
200
150
100
75
50
20
10
0

Rum och delområden, lux

Rum	Medel	Min	Max	Jämnhet U_0
Allrum	247	115	711	0,47
Badrum	284	84	417	0,30
Bänken längs 3NV (0,91 m)	570	170	779	0,30
Bänken längs 3SV (0,91 m)	240	107	522	0,45
Gästrum	53	42	59	0,79
Gång	126	118	139	0,94
Hall	97	79	153	0,81
Kontor	192	55	381	0,29
Kontor, litet	53	41	61	0,77
Kök	297	43	622	0,14
Sovrum	31	5	56	0,17
Sovrum, litet	227	94	298	0,42
Trappa	2	2	3	0,79
Vardagsrum	256	88	435	0,34
Ön (0,91 m)	803	180	2 034	0,22

Anvisningar

1. Belysningsstyrkan på en vågrät yta 0,75 m över golvet, i rutor om 50 mm, ur renderingen i Blender (Cycles): armaturernas uppmätta ljusfördelning (tillverkarnas fotometrifiler), dagsljuset och reflexerna i rummen. Delområdena Bänken längs 3NV, Bänken längs 3SV och Ön mäts på en vågrät yta 0,91 m över golvet.
2. Tända: AL-T1 Allrum, tubspotar sydost; AL-T2 Allrum, tubspotar nordväst; AL-T3 Allrum, PH 5 över bordet; KO-T1 Kök, tubspotar mot taket; KO-T2 Kök, spotar mot bänken; KO-T3 Kök, Stav över ön; GA-T1 Gång, tubspotar; HA-T1 Hall, tubspotar; VR-T1 Vardagsrum, spotar sydost; VR-T2 Vardagsrum, spotar nordväst; VR-T3 Vardagsrum, VL45; BA-T1 Badrum, spotar; BA-T2 Badrum, lampan över tvättstället; SV-T1 Sovrum, glob; KT-T1 Kontor, spotar mot väggarna; SL-T1 Sovrum litet, spotar mot gaveln; SL-T2 Sovrum litet, spotar mot L1; KL-T1 Kontor litet, glob; GR-T1 Gästrum, glob; taklamporna kallare (16 LED-paneler 600 × 600 mm, 2 500 lm och 3 000 K).
3. Inget dagsljus (2026-12-21 kl. 22:00).
4. Statistiken per rum utan en kantzon på 0,5 m längs väggarna (SS-EN 12464-1), i små rum mindre, och utan inredningen på mätytan (skåp, säng och bänkskivor, vita på planen); jämnheten U_0 = minsta / medel. Rummen är de slutna ytorna mellan väggarna; en öppen planlösning delas mellan rummens namn.
5. Ritningen ritas med ./mod ljusplan (verktyg/modellering); mätytorna står i modellens el/matytor.py.

Teckenförklaring

- isolinje, med belysningsstyrkan
- rummets yta i statistiken (utan kantzonen)
- delområde med egen statistik
- armatur

Rev	Avser	Datum	Sign

PROJEKT

Fritidshus Trebodar, Resö, Tanum

FASTIGHET

Resö 2:66, Tanums kommun · BYGG.2025.2278

INNEHÅLL

Ljusplan
Plan 1, bordshöjd 0,75 m


SKALA	FORMAT	DATUM
1:75	A3	2026-11-05
UPPRÄTTAD	GRANSKAD	UNDERLAG
Viktor Ogeman	–	Modellen, rendering
STATUS		REVISION
UTREDNING		**A**

RITNINGSNUMMER

U-04.2

Köket, bänkskivorna 0,91 m, belysningsstyrka

Skala 1:50

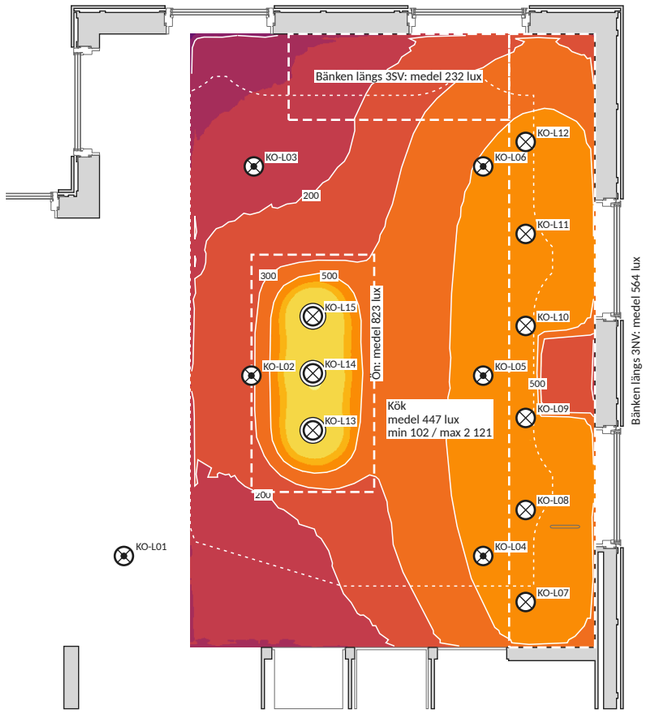

Belysningsstyrka, lux

5 000
2 000
1 000
750
500
300
200
150
100
75
50
20
10
0

Rum och delområden, lux

Rum	Medel	Min	Max	Jämnhet U_0
Bänken längs 3NV	564	140	751	0,25
Bänken längs 3SV	232	101	482	0,43
Kök	447	102	2 121	0,23
Ön	823	200	2 121	0,24

Anvisningar

1. Belysningsstyrkan på en vågrät yta 0,91 m över golvet, i rutor om 25 mm, ur renderingen i Blender (Cycles): armaturernas uppmätta ljusfördelning (tillverkarnas fotometrifiler), dagsljuset och reflexerna i rummen.
2. Tända: AL-T1 Allrum, tubspotar sydost; AL-T2 Allrum, tubspotar nordväst; AL-T3 Allrum, PH 5 över bordet; KO-T1 Kök, tubspotar mot taket; KO-T2 Kök, spotar mot bänken; KO-T3 Kök, Stav över ön; GA-T1 Gång, tubspotar; HA-T1 Hall, tubspotar; VR-T1 Vardagsrum, spotar sydost; VR-T2 Vardagsrum, spotar nordväst; VR-T3 Vardagsrum, VL45; BA-T1 Badrum, spotar; BA-T2 Badrum, lampan över tvättstället; SV-T1 Sovrum, glob; KT-T1 Kontor, spotar mot väggarna; SL-T1 Sovrum litet, spotar mot gaveln; SL-T2 Sovrum litet, spotar mot L1; KL-T1 Kontor litet, glob; GR-T1 Gästrum, glob; taklamporna kallare (16 LED-paneler 600 × 600 mm, 2 500 lm och 3 000 K).
3. Inget dagsljus (2026-12-21 kl. 22:00).
4. Statistiken per rum utan en kantzon på 0,5 m längs väggarna (SS-EN 12464-1), i små rum mindre, och utan inredningen på mätytan (skåp, säng och bänkskivor, vita på planen); jämnheten U_0 = minsta / medel. Rummen är de slutna ytorna mellan väggarna; en öppen planlösning delas mellan rummens namn.
5. Ritningen ritas med ./mod ljusplan (verktyg/modellering); mätytorna står i modellens el/matytor.py.

Teckenförklaring

- isolinje, med belysningsstyrkan
- rummets yta i statistiken (utan kantzonen)
- delområde med egen statistik
- armatur

Rev	Avser	Datum	Sign

PROJEKT

Fritidshus Trebodar, Resö, Tanum

FASTIGHET

Resö 2:66, Tanums kommun · BYGG.2025.2278

INNEHÅLL

Ljusplan
Köket, bänkskivorna 0,91 m

SKALA	FORMAT	DATUM
1:50	A3	2026-11-05

UPPRÄTTAD	GRANSKAD	UNDERLAG
Viktor Ogeman	–	Modellen, rendering


STATUS	REVISION
UTREDNING	**A**

RITNINGSNUMMER

U-04.3

Källaren, golvet, belysningsstyrka

Skala 1:75

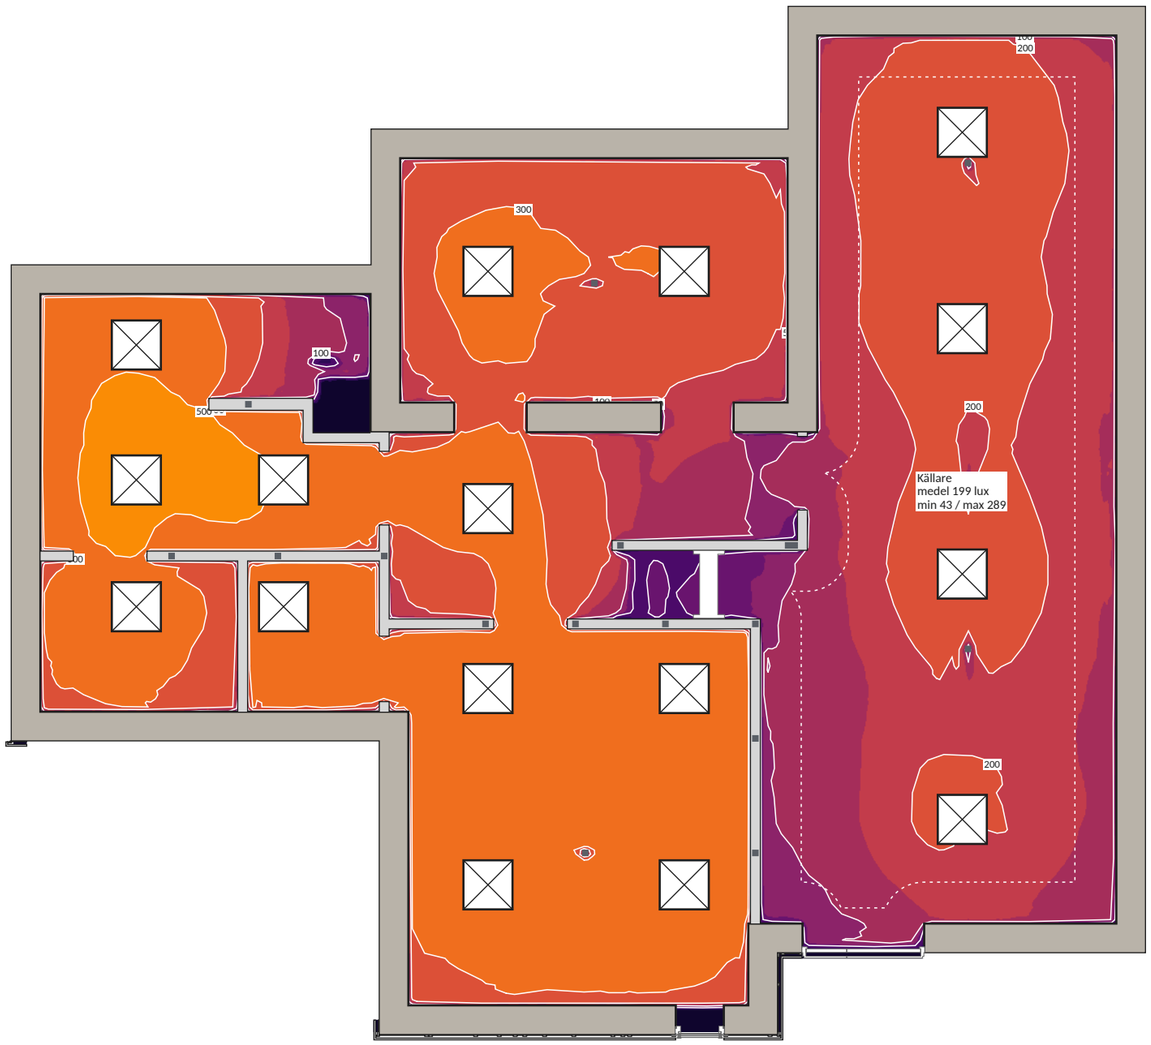

0 1 2 3 4 5 m

Belysningsstyrka, lux

5 000
2 000
1 000
750
500
300
200
150
100
75
50
20
10
0

Rum och delområden, lux

Rum	Medel	Min	Max	Jämnhet U_0
Källare	199	43	289	0,22

Anvisningar

1. Belysningsstyrkan på golvet, i rutor om 50 mm, ur renderingen i Blender (Cycles): armaturernas uppmätta ljusfördelning (tillverkarnas fotometrifiler), dagsljuset och reflexerna i rummen.
2. Tända: AL-T1 Allrum, tubspotar sydost; AL-T2 Allrum, tubspotar nordväst; AL-T3 Allrum, PH 5 över bordet; KO-T1 Kök, tubspotar mot taket; KO-T2 Kök, spotar mot bänken; KO-T3 Kök, Stav över ön; GA-T1 Gång, tubspotar; HA-T1 Hall, tubspotar; VR-T1 Vardagsrum, spotar sydost; VR-T2 Vardagsrum, spotar nordväst; VR-T3 Vardagsrum, VL45; BA-T1 Badrum, spotar; BA-T2 Badrum, lampan över tvättstället; SV-T1 Sovrum, glob; KT-T1 Kontor, spotar mot väggarna; SL-T1 Sovrum litet, spotar mot gaveln; SL-T2 Sovrum litet, spotar mot L1; KL-T1 Kontor litet, glob; GR-T1 Gästrum, glob; taklamporna kallare (16 LED-paneler 600 × 600 mm, 2 500 lm och 3 000 K).
3. Inget dagsljus (2026-12-21 kl. 22:00).
4. Statistiken per rum utan en kantzon på 0,5 m längs väggarna (SS-EN 12464-1), i små rum mindre, och utan inredningen på mätytan (skåp, säng och bänkskivor, vita på planen); jämnheten U_0 = minsta / medel. Rummen är de slutna ytorna mellan väggarna; en öppen planlösning delas mellan rummens namn.
5. Ritningen ritas med ./mod ljusplan (verktyg/modellering); mätytorna står i modellens el/matytor.py.

Teckenförklaring

- isolinje, med belysningsstyrkan
- rummets yta i statistiken (utan kantzonen)
- delområde med egen statistik
- armatur
- taklampa (LED-panel)

Rev	Avser	Datum	Sign

PROJEKT

Fritidshus Trebodar, Resö, Tanum

FASTIGHET

Resö 2:66, Tanums kommun · BYGG.2025.2278

INNEHÅLL

Ljusplan
Källaren, golvet

SKALA	FORMAT	DATUM
1:75	A3	2026-11-05
UPPRÄTTAD	GRANSKAD	UNDERLAG
Viktor Ogeman	–	Modellen, rendering
STATUS		REVISION
UTREDNING		**A**

RITNINGSNUMMER

U-04.4