


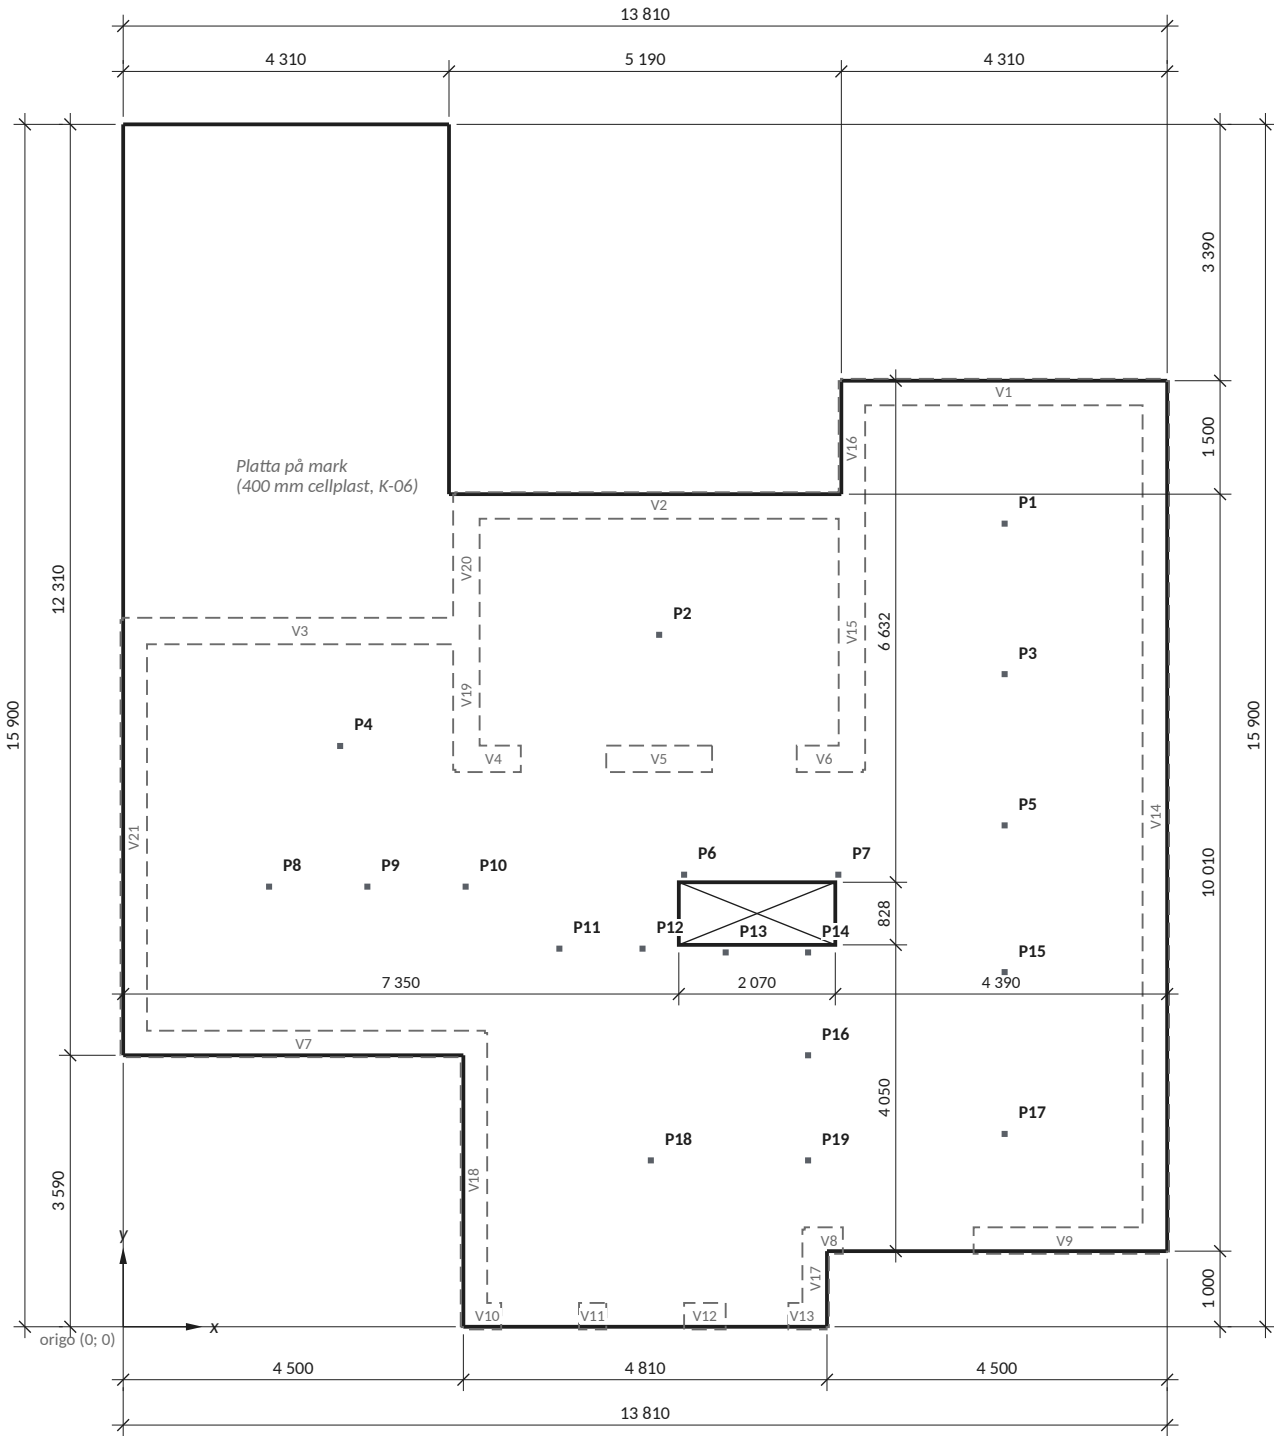

PLAN - ÖVERSIKT OCH YTTERMÅTT

Skala 1:100



Anvisningar

- Betong C25/30, exponeringsklass XC1, livslängd 50 år. Armering B500B.
- Täckskikt: underkant 20 mm, överkant 25 mm, kanter och hålskanter 25 mm.
- Skarvlängd: Ø8 500, Ø10 650, Ø12 750 mm. Skarvar förskjuts minst 1,3 x skarvlängden.
- x-järnen ligger ytterst i båda näten. Tilläggsjärn läggs i nätets lager.
- Koordinater i mm enligt K-05; origo i skärningen mellan plattkanterna x = 0 och y = 0. Mått, se R-03.1.
- Plattans kontur och trapphålets läge enligt denna ritning. Rörens lägen, se tabell på R-03.2.
- Lecaväggarna under plattan streckade (K-06).

Teckenförklaring

- plattans kant
- Lecavägg under plattan
- stålrör VKR 80x80x4 (K-05)

Ritningsförteckning R-03

Ritning	Innehåll	Skala
R-03.1	Översikt och yttermått	1:100
R-03.2	Armering i underkant	1:50
R-03.3	Armering i överkant	1:50
R-03.4	Sektioner, detaljer och stålförteckning	1:5, 1:10, 1:20

Rev	Avser	Datum	Sign
A	Första utgåvan	2026-10-08	VO

PROJEKT

Fritidshus Trebodar, Resö, Tanum

FASTIGHET

Resö 2:66, Tanums kommun · BYGG.2025.2278

INNEHÅLL

Mellanbjälklag Översikt och yttermått

SKALA	FORMAT	DATUM
1:100	A3	2026-10-08
UPPRÄTTAD	GRANSKAD	UNDERLAG
Viktor Ogeman	-	K-05 rev A, K-06
STATUS	REVISION	
FÖR GRANSKNING	A	

RITNINGNUMMER

R-03.1