


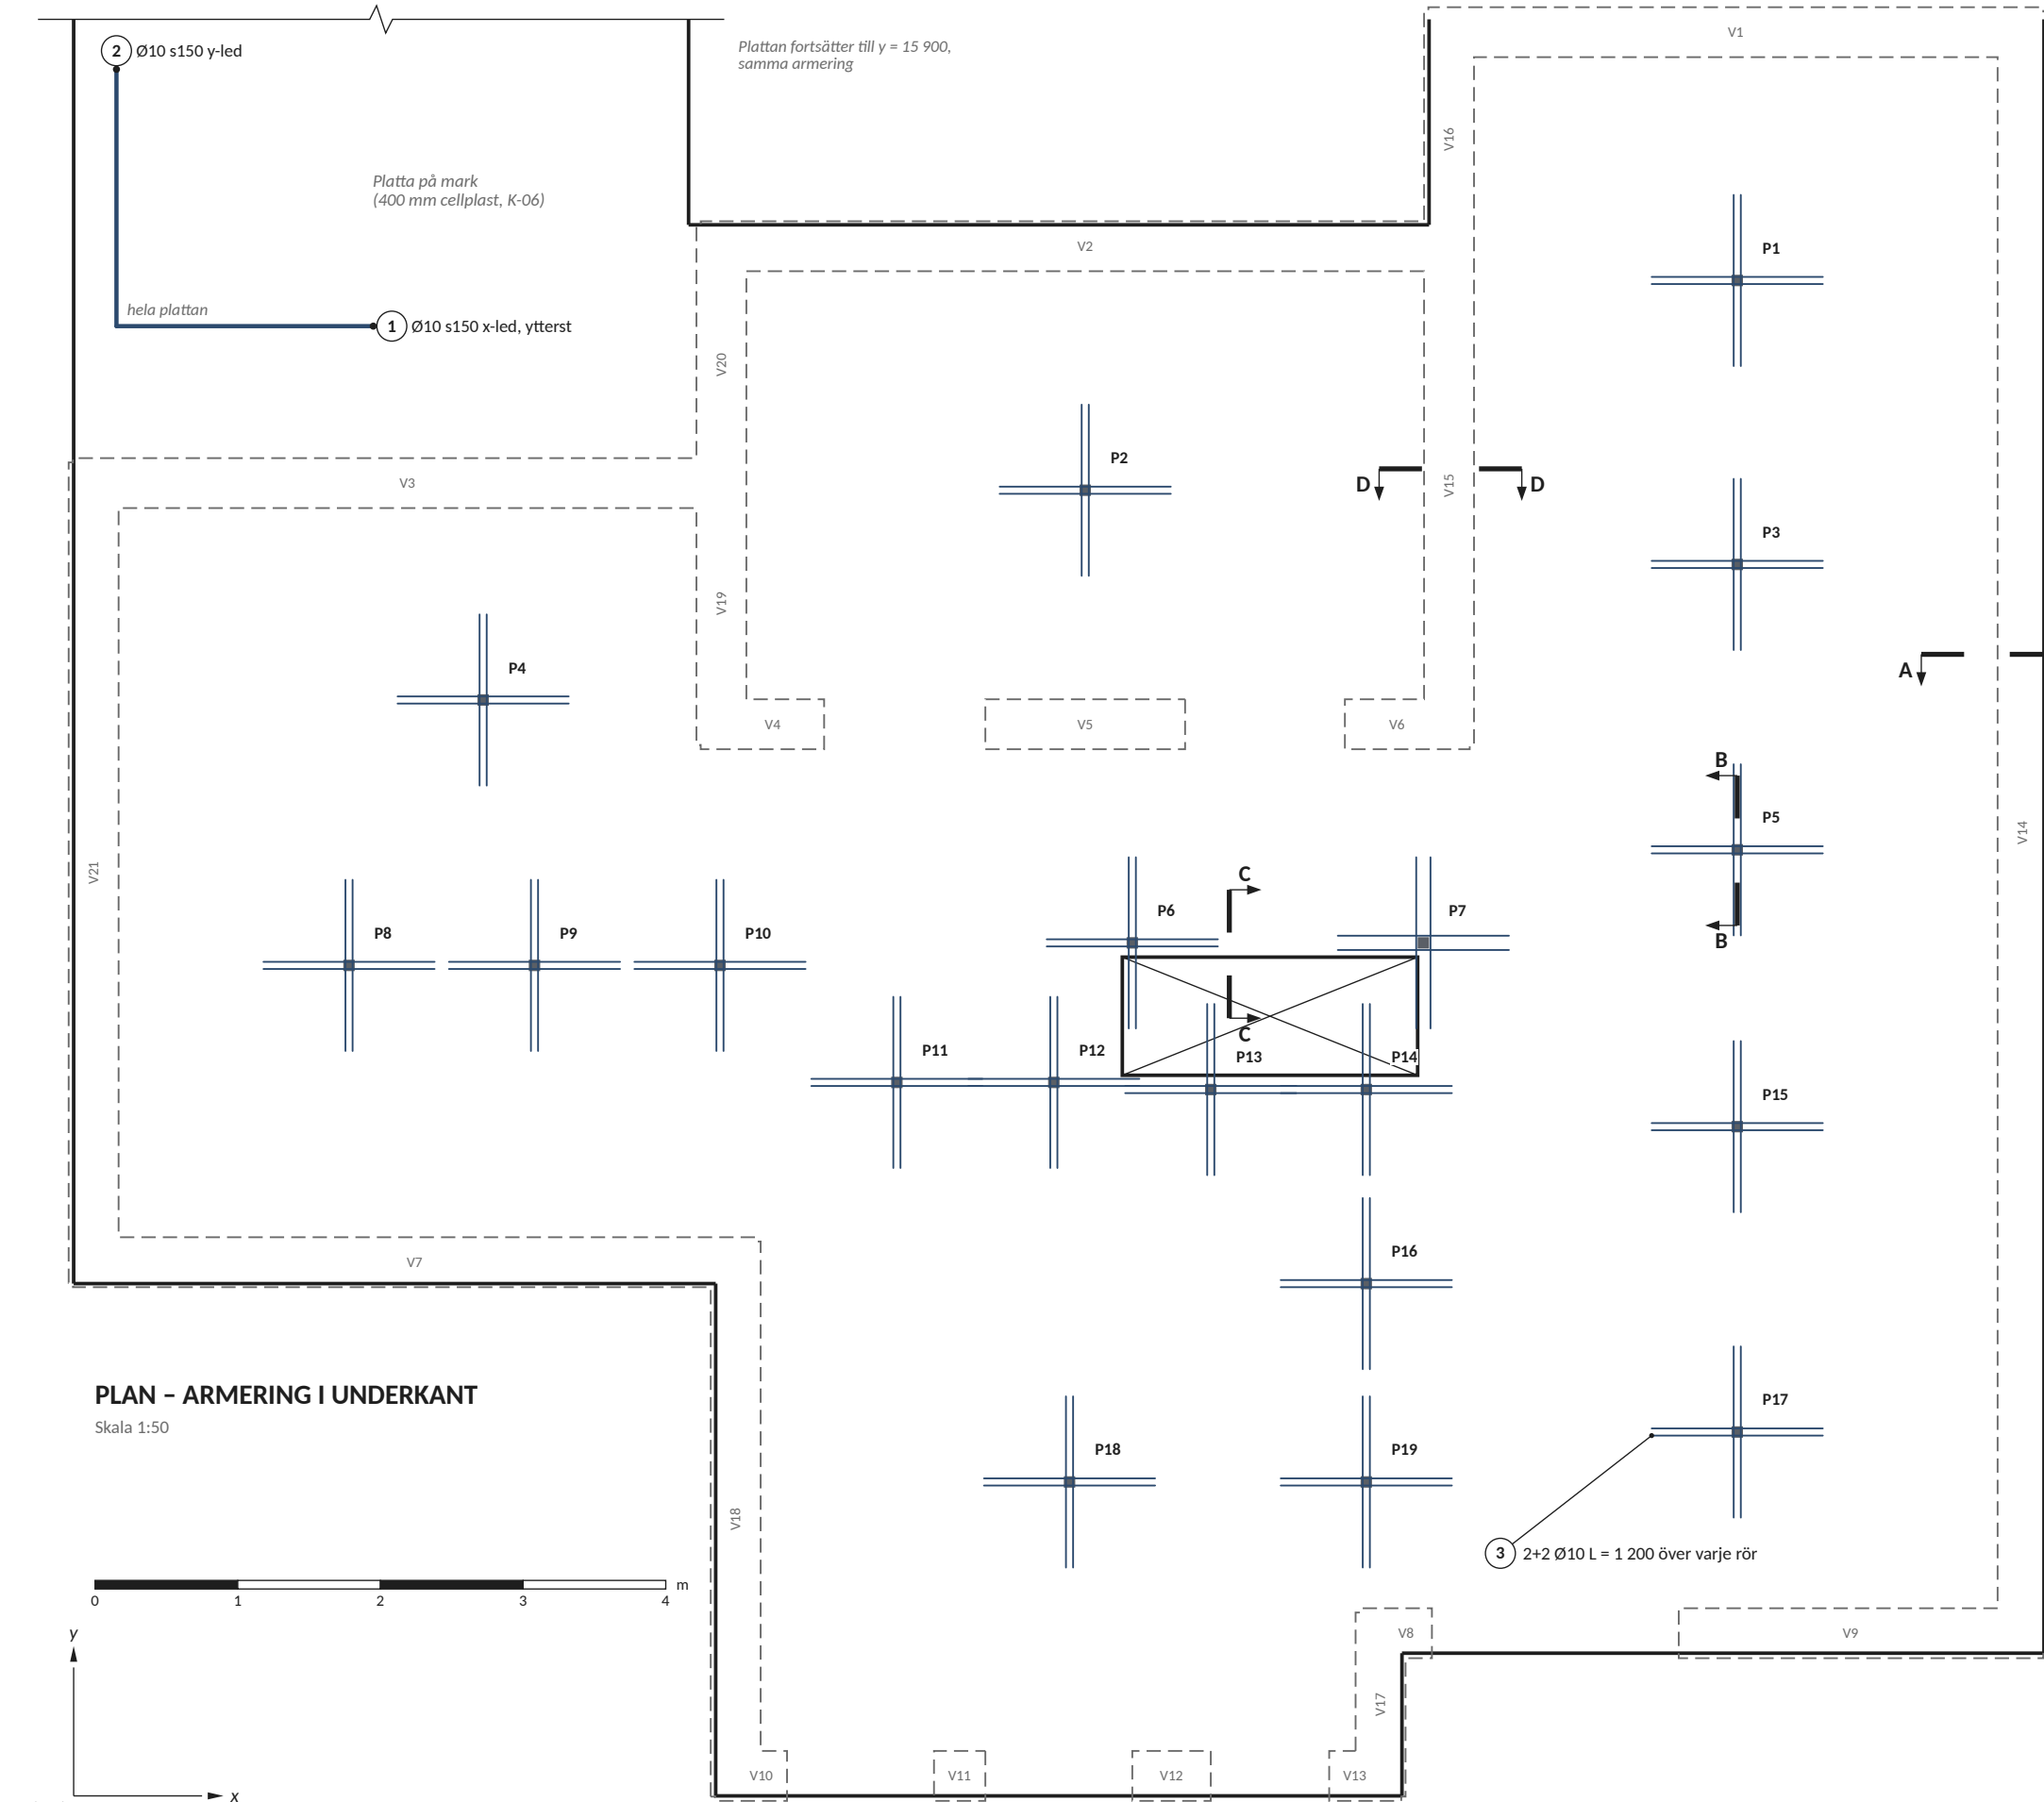

Anvisningar

- Betong C25/30, exponeringsklass XC1, livslängd 50 år. Armering B500B.
- Täckskikt: underkant 20 mm, överkant 25 mm, kanter och hållkanter 25 mm.
- Skarvlängd: Ø8 500, Ø10 650, Ø12 750 mm. Skarvar förskjuts minst 1,3 x skarvlängden.
- x-järnen ligger ytterst i båda näten. Tilläggsjärn läggs i nätets lager.
- Koordinater i mm enligt K-05; origo i skärningen mellan plattkanterna x = 0 och y = 0. Mått, se R-03.1.
- Underkantsnätet läggs på distanser 20 mm, högst 0,8 m isär.
- Minst två underkantsjärn i vardera riktningen ska passera över varje rör (SS-EN 1992-1-1 9.4.1(3)): pos 3, bundna till nätet.
- Överkant, se R-03.3. Sektioner A–D, se R-03.4.

Teckenförklaring

- armering i underkant
- positionsnummer (stålförteckning R-03.4)
- Lecavägg under plattan
- stålrör VKR 80×80×4 (K-05)

Rör och toppplåtar

Rör	x	y	Topplåt
P1	11 660	10 620	80×80×8
P2	7 090	9 150	80×80×8
P3	11 660	8 630	80×80×8
P4	2 870	7 680	80×80×8
P5	11 660	6 630	80×80×8
P6	7 420	5 978	80×80×8
P7	9 460	5 978	160×160×25 S355
P8	1 930	5 820	80×80×8
P9	3 230	5 820	80×80×8
P10	4 530	5 820	80×80×8
P11	5 770	5 000	80×80×8
P12	6 870	5 000	80×80×8
P13	7 970	4 950	80×80×8
P14	9 060	4 950	80×80×8
P15	11 660	4 690	80×80×8
P16	9 060	3 590	80×80×8
P17	11 660	2 550	80×80×8
P18	6 980	2 200	80×80×8
P19	9 060	2 200	80×80×8

Rev	Avser	Datum	Sign
A	Första utgåvan	2026-10-08	VO

PROJEKT

Fritidshus Trebodar, Resö, Tanum

FASTIGHET

Resö 2:66, Tanums kommun · BYGG.2025.2278

INNEHÅLL

Mellanbjälklag
Armering i underkant

KALA	FORMAT	DATUM
1:50	A3	2026-10-08
UPPRÄTTAD	GRANSKAD	UNDERLAG
Viktor Ogeman	–	K-05 rev A, K-06
STATUS		REVISION
FÖR GRANSKNING		A
RITNINGNUMMER		

R-03.2