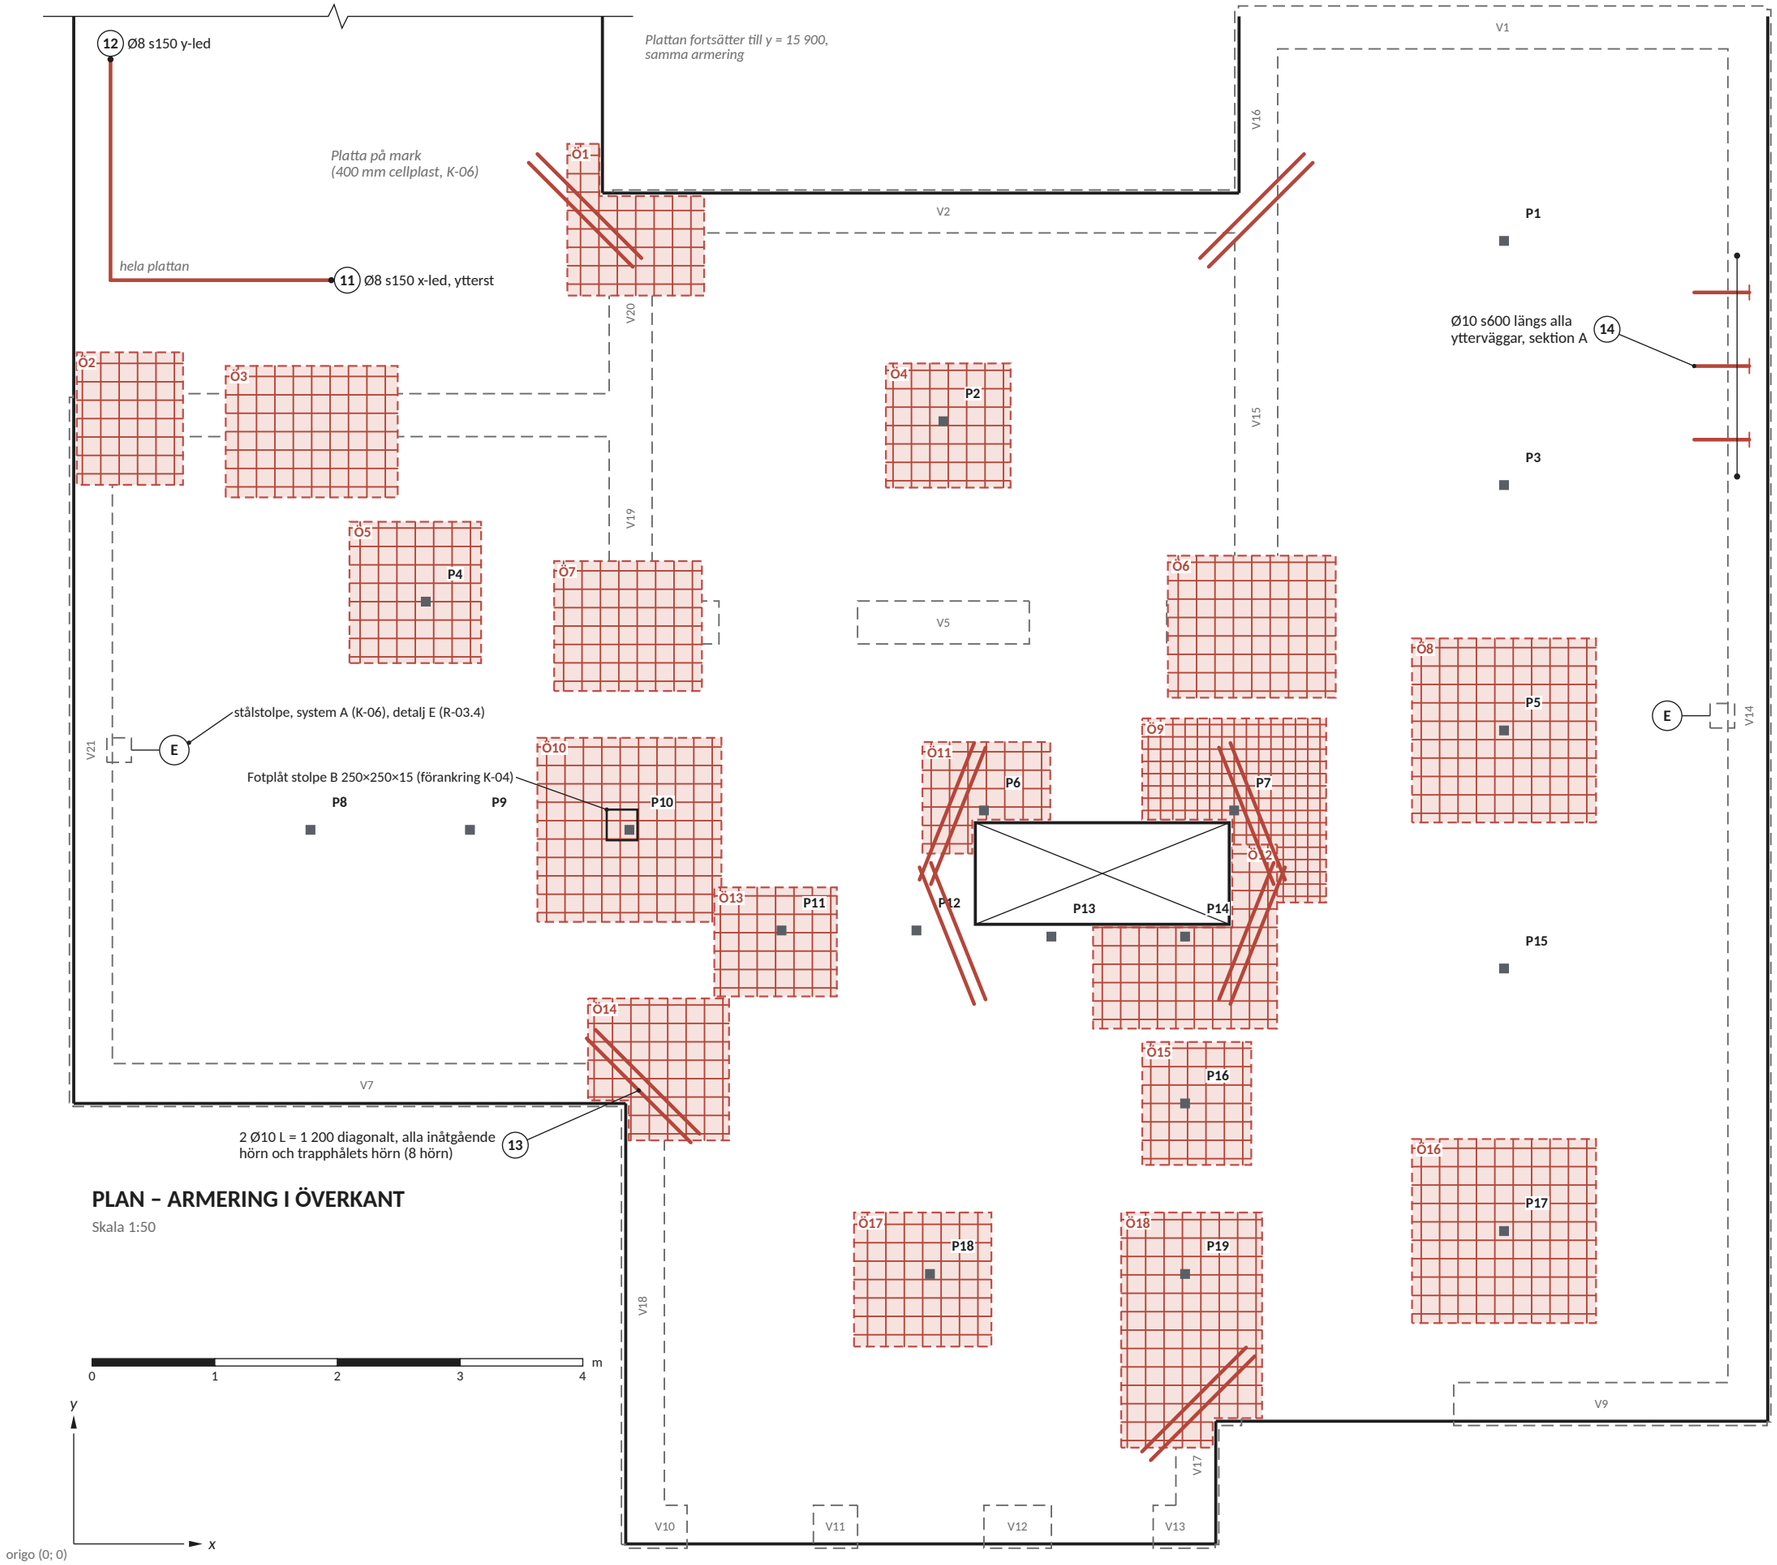


PLAN – ARMERING I ÖVERKANT

Skala 1:50

Anvisningar

1. Allmänt, se R-03.2. Mått R-03.1, sektioner R-03.4.
2. Överkantsnätet läggs på armeringsstolar, högst 0,8 m isär.
3. Tilläggsjärnen i zonerna Ö1–Ö18 läggs i båda riktningarna i nätets lager och binds till nätet (s150: mitt emellan nätets järn). Där zonen når plattans kant förs järnen ut till kanten.
4. Stålstolparnas plåtar (E) gäller system A i K-06. Gjuts in i underkant, se R-03.4.
5. Förankringsjärnen pos 14 sätts i U-blocket innan bjälklaget gjuts.

Teckenförklaring

- armering i överkant
- zon med tilläggsjärn i överkant
- fördelning av järn med samma position
- Lecavägg eller plåt under plattan
- stålrör VKR 80×80×4 (K-05)

Tilläggsjärn i överkant (antal × längd)

Zon	Järn	x-led	y-led	x (m)	y (m)
Ö1	Ø12 s150	8 st, 300–1 150	7 st, 850–1 250	4,02–5,14	10,17–11,41
Ö2	Ø8 s150	7 × 900	6 × 1 100	0,00–0,89	8,63–9,71
Ö3	Ø8 s150	7 × 1 450	9 × 1 100	1,24–2,64	8,53–9,60
Ö4	Ø8 s150	7 × 1 050	7 × 1 050	6,62–7,64	8,61–9,62
Ö5	Ø8 s150	8 × 1 100	7 × 1 200	2,25–3,32	7,18–8,33
Ö6	Ø12 s150	8 × 1 400	9 × 1 200	8,92–10,29	6,90–8,05
Ö7	Ø8 s150	7 × 1 250	8 × 1 100	3,92–5,12	6,95–8,01
Ö8	Ø8 s150	10 × 1 500	10 × 1 500	10,91–12,41	5,88–7,38
Ö9	Ø12 s100	15 st, 800–1 500	15 st, 850–1 500	8,71–10,21	5,23–6,73
Ö10	Ø12 s150	10 × 1 500	10 × 1 500	3,78–5,28	5,07–6,57
Ö11	Ø8 s150	6 st, 450–1 050	7 st, 650–950	6,92–7,96	5,63–6,54
Ö12	Ø10 s150	11 st, 400–1 500	10 st, 850–1 500	8,31–9,81	4,20–5,70
Ö13	Ø8 s150	6 × 1 000	7 × 900	5,22–6,22	4,46–5,35
Ö14	Ø8 s150	8 st, 850–1 150	8 st, 850–1 200	4,19–5,34	3,29–4,45
Ö15	Ø8 s150	7 × 900	6 × 1 050	8,71–9,60	3,09–4,09
Ö16	Ø10 s150	10 × 1 500	10 × 1 500	10,91–12,41	1,80–3,30
Ö17	Ø8 s150	7 × 1 150	7 × 1 100	6,36–7,48	1,61–2,70
Ö18	Ø8 s150	13 st, 750–1 150	8 st, 1 700–1 950	8,54–9,69	0,78–2,70

Rev	Avser	Datum	Sign
A	Första utgåvan	2026-10-08	VO

PROJEKT

Fritidshus Trebodar, Resö, Tanum

FASTIGHET

Resö 2:66, Tanums kommun · BYGG.2025.2278

INNEHÅLL

Mellanbjälklag
Armering i överkant

SKALA	FORMAT	DATUM
1:50	A3	2026-10-08
UPPRÄTTAD	GRANSKAD	UNDERLAG
Viktor Ogeman	–	K-05 rev A, K-06
STATUS		REVISION
FÖR GRANSKNING		**A**

RITNINGSNUMMER

R-03.3