

NOCKBALK 1

NB1 · L = 11 570 · plåtar NB1-1-O/U · 172 skruv

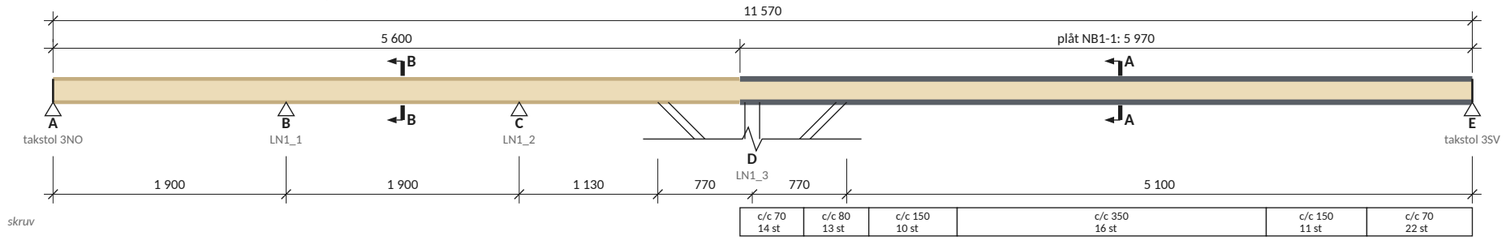


NOCKBALK 3

NB3 · L = 11 070 · plåtar NB3-1-O/U · 114 skruv

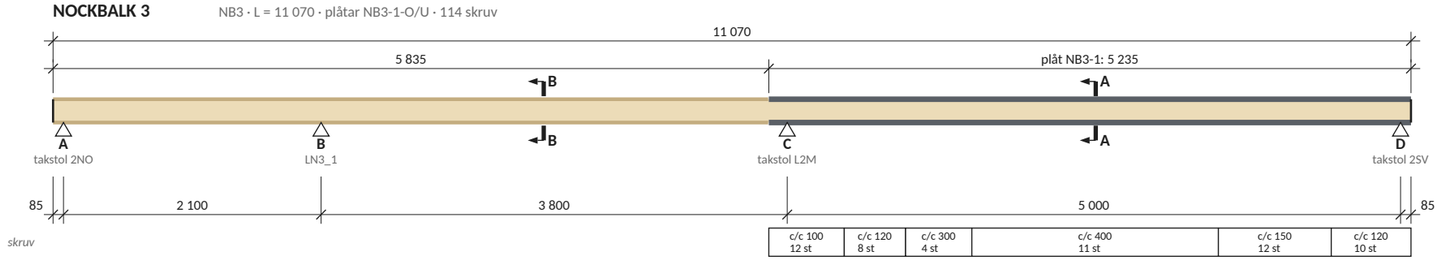


NOCKBALK 5

NB5 · L = 12 370 · plåtar NB5-1-O/U och NB5-2-O/U · 208 skruv

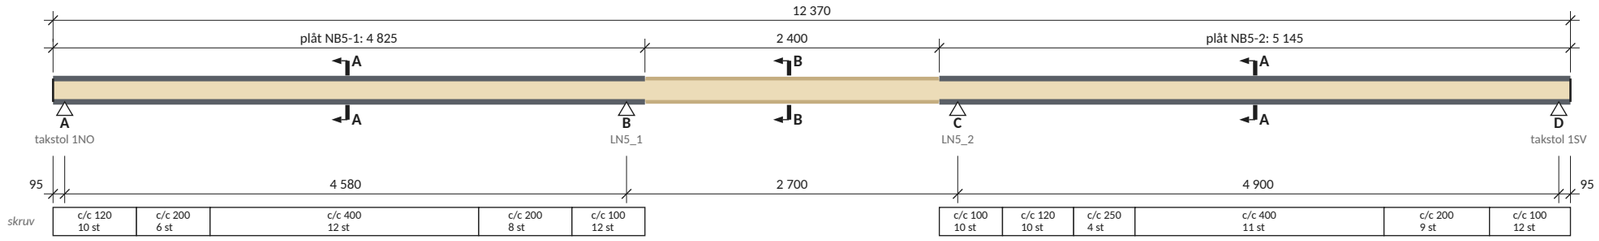


DALBALK 2

DB2 · L = 10 070 · plåtar DB2-1-O/U · 96 skruv

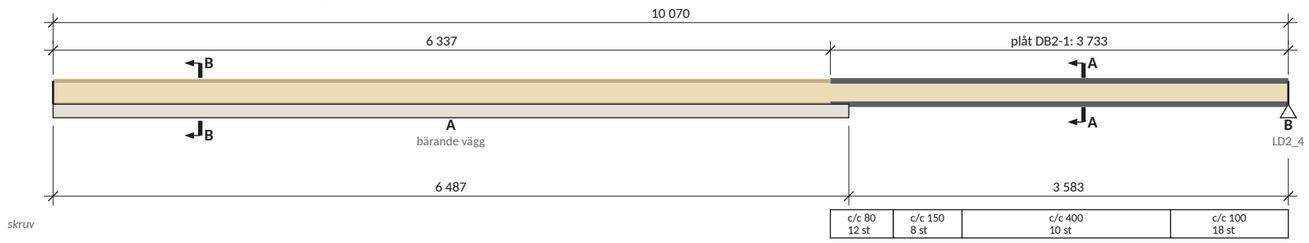

DALBALK 4


DB4 · L = 7 480 · plåtar DB4-1-O/U · 196 skruv

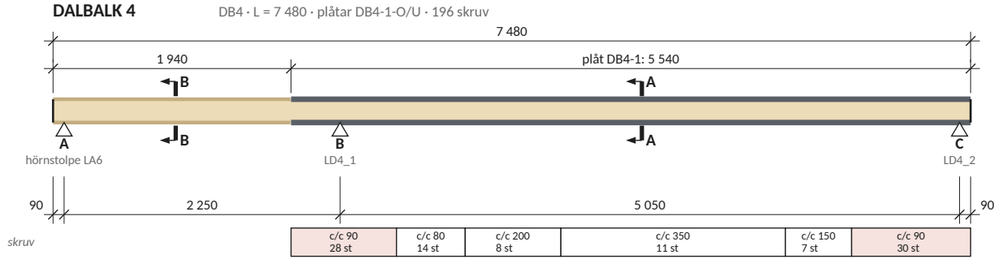

ELEVATIONER Nock- och dalbalkar

Skala 1:50



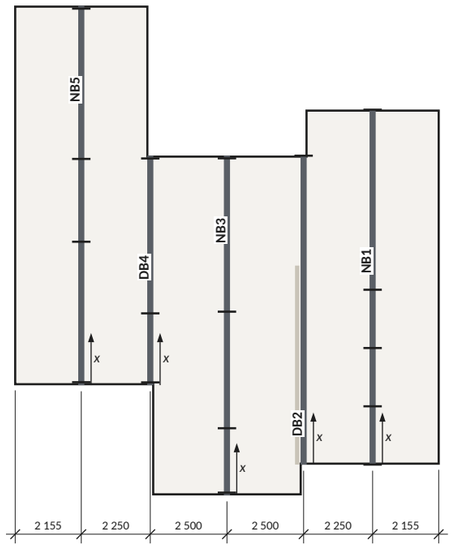

PLAN Balkarnas lägen

Skala 1:200

K-05:s koordinater, mm. Strecken på balkarna är stöden, x = 0 vid balkens nedre ände.

Anvisningar

1. Limträ GL30c 200×170 i hel längd. Plattstål 200×10 S355J2+N i över- och underkant där plåt anges, limmat och skruvat. I övrigt distansreglar 200×10. Balkens höjd 190 mm. Sektioner och detaljer: R-01.2.
2. x räknas från balkens vänstra ände, som ligger mot lägre y (planen). Plåtarna och skruvzonerna är inte symmetriska: balken monteras med x = 0 åt det hållet.
3. Stöden A, B, … som i K-01, stolparna och takstolarna som i K-03 och K-05. Stöden förankras för dragkraften R min i tabellen (K-03).
4. Skruvzonerna: c/c i varje rad och antal skruv per plåt (lika i över- och underplåt). Två rader om inget annat anges. Hålen laserskärs enligt hålbilderna (R-01.2), en skruv i varje hål.
5. Huvudstolpen LN1_3 med strävor till nockbalk 1, 770 mm från stolpen åt båda hållen: K-03.

Teckenförklaring

- limträ GL30c 200×170
- plattstål 200×10, över- och underplåt
- distansregel 200×10
- stöd (stolpe eller takstol)
- bärande vägg
- skruvzon, två rader
- skruvzon, tre rader

Stöd och förankring

Balk	Stöd	x (mm)	Bärs av	R max	R min	l min
NB1	A	0	takstol 3NO	7,3	−3,0	7
	B	1 900	LN1_1	19,8	−6,5	12
	C	3 800	LN1_2	9,9	−16,9	6
	D	5 700	LN1_3	49,0	−12,3	13
	E	11 570	takstol 3SV	21,5	−6,3	20
NB3	A	85	takstol 2NO	8,0	−3,4	5
	B	2 185	LN3_1	23,9	−7,2	15
	C	5 985	takstol L2M	36,6	−9,4	22
	D	10 985	takstol 2SV	18,9	−6,2	12
NB5	A	95	takstol 1NO	17,5	−6,1	11
	B	4 675	LN5_1	30,9	−7,1	19
	C	7 375	LN5_2	32,6	−7,4	20
	D	12 275	takstol 1SV	18,6	−6,4	12
DB2	A	0–6 487	bärande vägg	41,0[1]	−18,6[1]	–
	B	10 070	LD2_4	21,2	−4,5	19
DB4	A	90	hörnstolpe LA6	14,0	−3,8	9
	B	2 340	LD4_1	54,2	−9,0	37
	C	7 390	LD4_2	31,0	−6,0	19

Dimensionerande stödreaktioner (kN) enligt K-01. R min är dragkraft vid vindlyft (negativ). I min: minsta upplagslängd (mm) för tryck vinkelrätt fiberrna.
[1] Väggen: R_max inom 0,5 m från väggänden, hela väggen högst 99 kN. R_min: dragkraften vid vindlyft sammanlagt.

Ritningsförteckning R-01

Ritning	Innehåll	Skala
R-01.1	Elevationer och lägen	1:50, 1:200
R-01.2	Sektioner, detaljer och förteckningar	1:2,5, 1:5

Rev	Avser	Datum	Sign
A	Första utgåvan	2026-10-13	VO

PROJEKT

Fritidshus Trebodar, Resö, Tanum

FASTIGHET

Resö 2:66, Tanums kommun · BYGG.2025.2278


INNEHÅLL

Nock- och dalbalkar
Elevationer och lägen

SKALA	FORMAT	DATUM
1:50, 1:200	A3	2026-10-13
UPPRÄTTAD	GRANSKAD	UNDERLAG
Viktor Ogeman	–	K-01 rev C, K-03
STATUS		REVISION
FÖR GRANSKNING		**A**


RITNINGSNUMMER

R-01.1

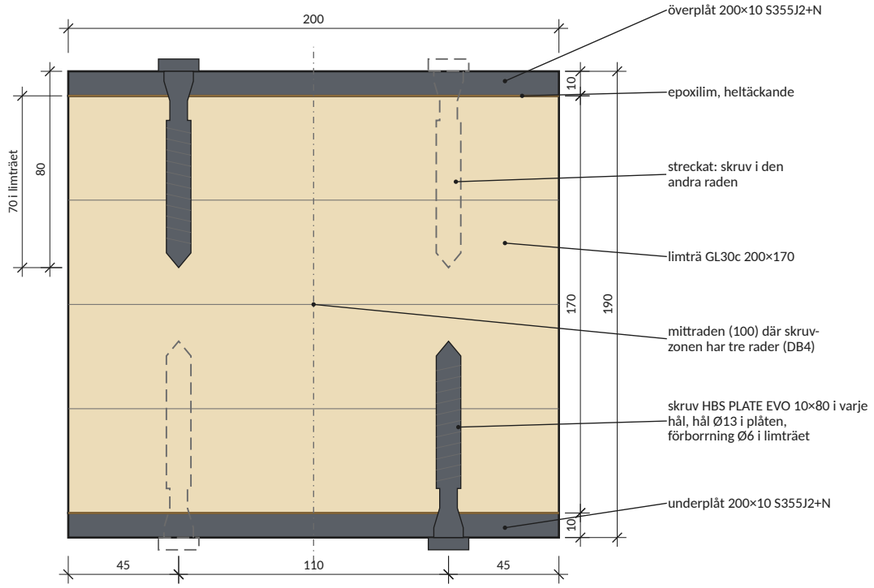


SEKTION A–A Med plåt

Skala 1:2.5

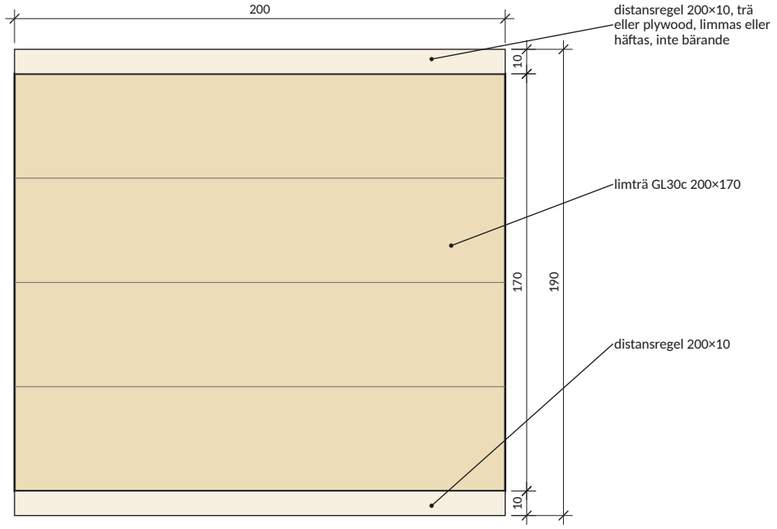

SEKTION B–B Utan plåt


Skala 1:2.5

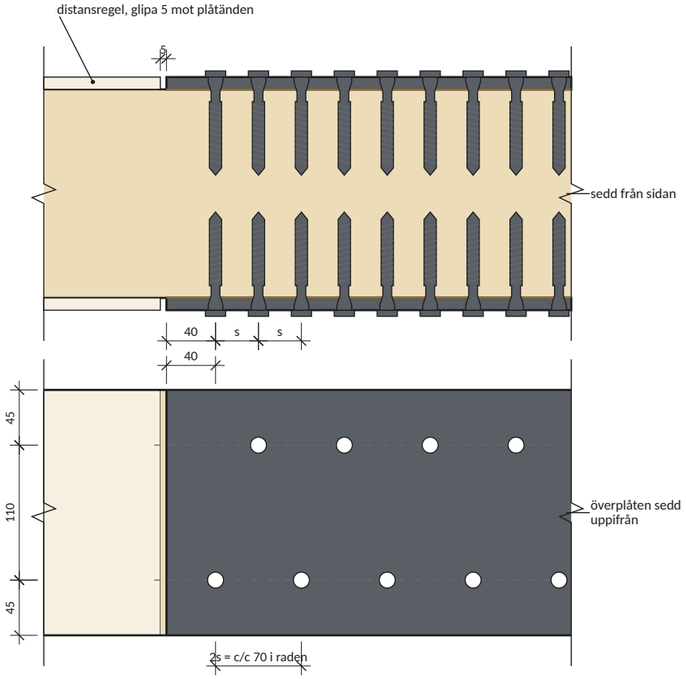

DETALJ C Plåtände inne på balken

Skala 1:5

Exempel: NB1-1 vid x = 5 600, två rader, s = 35.

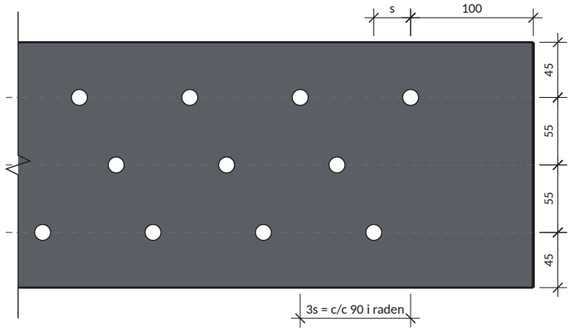

DETALJ D Tre rader vid balkänden

Skala 1:5

Exempel: DB4-1 vid balkänden x = 7 480, s = 30. Första skruv 100 från balkänden.

Plåtar, S355J2+N 200×10 (modeller/balkplattor)

Plåt	Läge	x i balken	L (mm)	Hål	Vikt (kg)
NB1-1-O	över	5 600–11 570	5 970	86	92,8
NB1-1-U	under	5 600–11 570	5 970	86	92,8
DB2-1-O	över	6 337–10 070	3 733	48	58,1
DB2-1-U	under	6 337–10 070	3 733	48	58,1
NB3-1-O	över	5 835–11 070	5 235	57	81,6
NB3-1-U	under	5 835–11 070	5 235	57	81,6
DB4-1-O	över	1 940–7 480	5 540	98	86,0
DB4-1-U	under	1 940–7 480	5 540	98	86,0
NB5-1-O	över	0–4 825	4 825	48	75,3
NB5-1-U	under	0–4 825	4 825	48	75,3
NB5-2-O	över	7 225–12 370	5 145	56	80,2
NB5-2-U	under	7 225–12 370	5 145	56	80,2
Summa	12 plåtar		60 896	786	948

Vikt efter håltagning.

Anvisningar

1. Limträ GL30c enligt SS-EN 14080, 200×170 i hel längd. Fuktkvot högst 12 % vid limning. Klimatklass 1.
2. Plåtar: plattstål 200×10 S355J2+N enligt SS-EN 10025-2, laserskurna enligt DXF- och STEP-filerna i modeller/balkplattor/, en fil per plåt. Bitarna skarvas inte.
3. Hål Ø13 genomgående, cylindriska, utan försänkning. Varje plåt märks med sitt namn, en pil mot balkens vänstra ände och framsidans kant (y = 0). Över- och underplåt har speglade hålbilder och kan inte bytas.
4. Ytor utanför limfogen: zinkrik grundfärg. Limytorna på stålet blästras eller slipas och avfettas. Träytan ska vara ren och torr.
5. Lim: tvåkomponents strukturepoxi för limning av stål (t.ex. Sikadur-30), heltäckande fog mot båda plåtarna i hela plåtlängden. Härdning enligt limtillverkarens anvisning.
6. Skruv: Rothoblaas HBS PLATE EVO 10×80 (HBSPLEVO1080, ETA-11/0030), C4 EVO. En skruv i varje hål, vinkelrätt mot plåten. Förborra Ø6 genom plåthålen, lika djupt som skruven.
7. Skruvarna dras medan limmet är färskt, i ett drag tills huvudet ligger an mot plåten, med högst 35 Nm (momentbegränsare eller momentnyckel), inte med slagskruvdragare.
8. Distansreglar 200×10 där plåt saknas: trä eller plywood, valfri kvalitet. Limmas med vanligt trälim eller häftas/spikas; inga krav på limprocessen. Glipa 5 mm mot plåtänden.
9. Annan skruv, annat lim eller ändrade hål kräver ny kontroll enligt K-01.
10. Takbalkarnas upplag på balkarnas sidor (upplagsregel 45×45) och förankring: K-03.

Teckenförklaring

- limträ GL30c
- stål S355J2+N
- distansregel
- epoxilim
- skruv i den andra raden
- skruvrad

Balkar

Balk	L	Plåt, x	Distansregel, x	Skruv
NB1	11 570	5 600–11 570	0–5 595	172
DB2	10 070	6 337–10 070	0–6 332	96
NB3	11 070	5 835–11 070	0–5 830	114
DB4	7 480	1 940–7 480	0–1 935	196
NB5	12 370	0–4 825, 7 225–12 370	4 830–7 220	208
Summa	52 560			786

Rev	Avser	Datum	Sign
A	Första utgåvan	2026-10-13	VO

PROJEKT

Fritidshus Trebodar, Resö, Tanum

FASTIGHET

Resö 2:66, Tanums kommun · BYGG.2025.2278

INNEHÅLL

Nock- och dalbalkar
Sektioner, detaljer och förteckningar

SKALA	FORMAT	DATUM
1:2,5, 1:5	A3	2026-10-13
UPPRÄTTAD	GRANSKAD	UNDERLAG
Viktor Ogeman	–	K-01 rev C, K-03
STATUS		REVISION
FÖR GRANSKNING		**A**

RITNINGSNUMMER

R-01.2