
Plan 1, golvet, belysningsstyrka

Skala 1:75

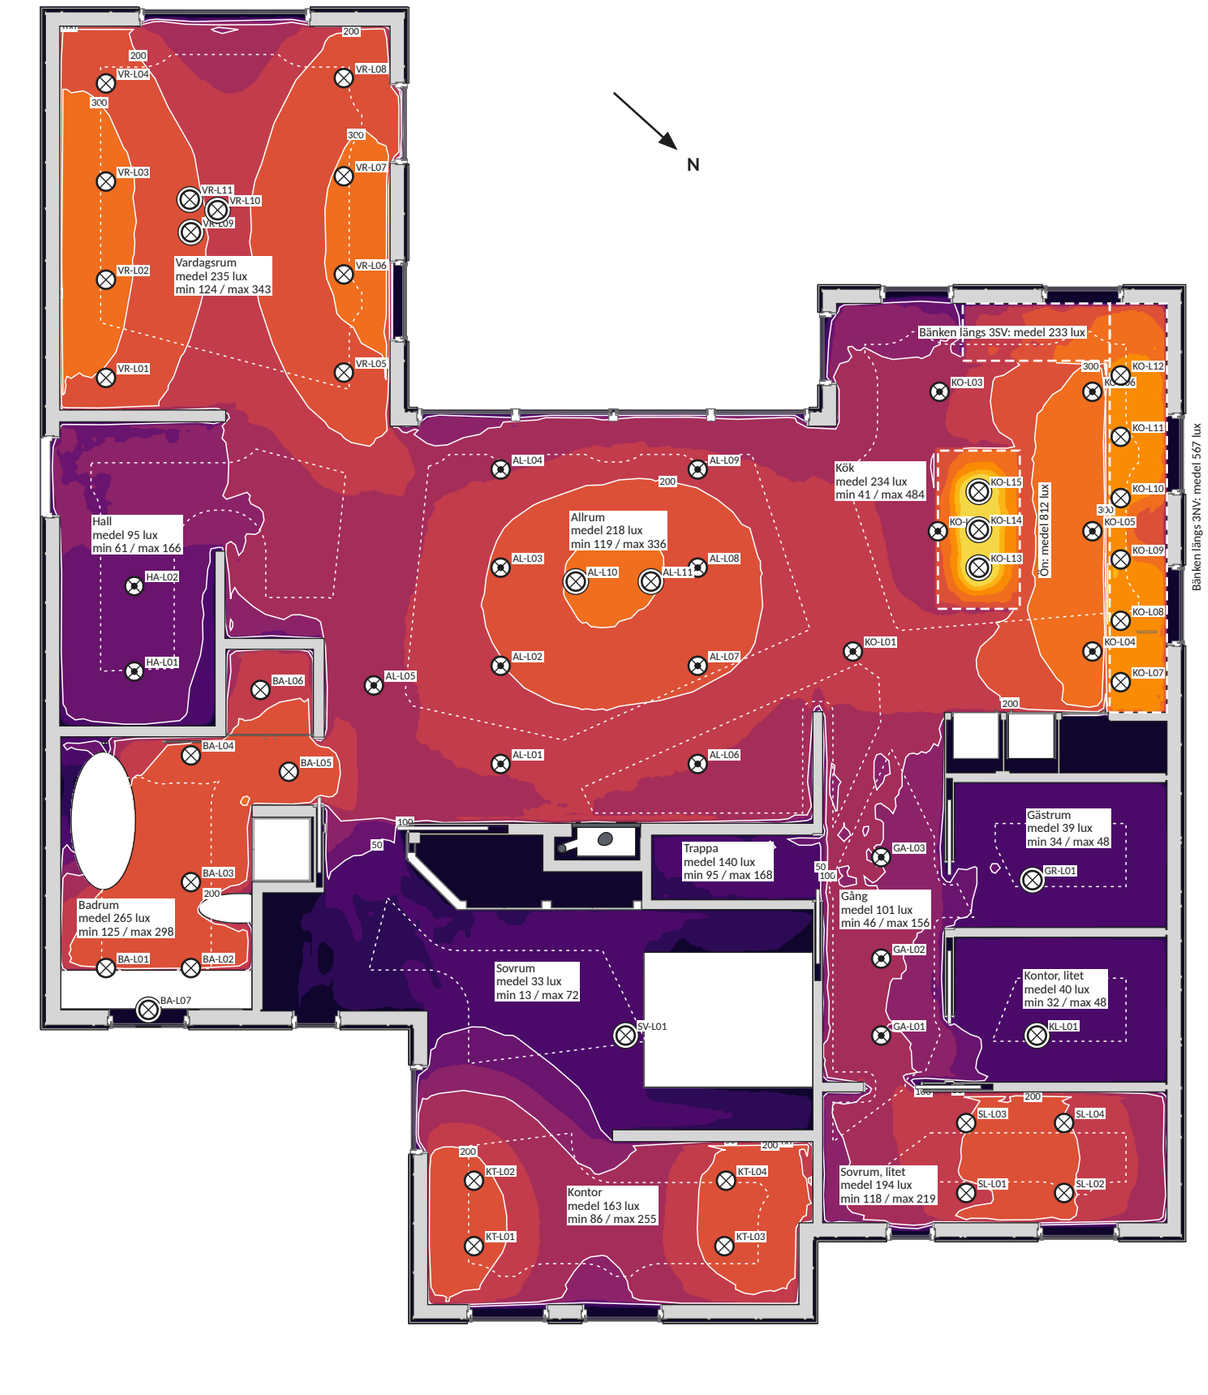

Belysningsstyrka, lux

5 000
2 000
1 000
750
500
300
200
150
100
75
50
20
10
0

Rum och delområden, lux

Rum	Medel	Min	Max	Jämnhet U_0
Allrum	218	119	336	0,54
Badrum	265	125	298	0,47
Bänken längs 3NV (0,91 m)	567	171	778	0,30
Bänken längs 3SV (0,91 m)	233	109	486	0,47
Gästrum	39	34	48	0,88
Gång	101	46	156	0,45
Hall	95	61	166	0,64
Kontor	163	86	255	0,53
Kontor, litet	40	32	48	0,81
Kök	234	41	484	0,17
Sovrum	33	13	72	0,38
Sovrum, litet	194	118	219	0,61
Trappa	140	95	168	0,68
Vardagsrum	235	124	343	0,53
Ön (0,91 m)	812	169	2 086	0,21

Anvisningar

1. Belysningsstyrkan på en vågrät yta 0,04 m över golvet, i rutor om 50 mm, ur renderingen i Blender (Cycles): armaturernas uppmätta ljusfördelning (tillverkarnas fotometrifiler), dagsljuset och reflexerna i rummen. Delområdena Bänken längs 3NV, Bänken längs 3SV och Ön mäts på en vågrät yta 0,91 m över golvet.
2. Tända: AL-T1 Allrum, tubspotar sydost; AL-T2 Allrum, tubspotar nordväst; AL-T3 Allrum, PH 5 över bordet; KO-T1 Kök, tubspotar mot taket; KO-T2 Kök, spotar mot bänken; KO-T3 Kök, Stav över ön; GA-T1 Gång, tubspotar; HA-T1 Hall, tubspotar; VR-T1 Vardagsrum, spotar sydost; VR-T2 Vardagsrum, spotar nordväst; VR-T3 Vardagsrum, VL45; BA-T1 Badrum, spotar; BA-T2 Badrum, lampan över tvättstället; SV-T1 Sovrum, glob; KT-T1 Kontor, spotar mot väggarna; SL-T1 Sovrum litet, spotar mot gaveln; SL-T2 Sovrum litet, spotar mot L1; KL-T1 Kontor litet, glob; GR-T1 Gästrum, glob; KA-T6 Källaren, det stora rummet; KA-T7 Källaren, det lilla rummet väster om KL2; KA-T8 Källaren, det lilla rummet öster om KL2; KA-T1 Källaren, trapphallen; KA-T2 Källaren, tvättstugan; KA-T3 Källaren, rummen norr om V4–V6, västra delen; KA-T4 Källaren, rummen norr om V4–V6, östra delen; KA-T5 Källaren, rummet söder om trapphallen.
3. Inget dagsljus (2026-12-21 kl. 22:00).
4. Statistiken per rum utan en kantzon på 0,5 m längs väggarna (SS-EN 12464-1), i små rum mindre, och utan inredningen på mätytan (skåp, säng, bänkskivor, källartrappan och pelarna, vita på planen); jämnheten U_0 = minsta / medel. Rummen är de slutna ytorna mellan väggarna; en öppen planlösning delas mellan rummens namn.
5. Ritningen ritas med ./mod ljusplan (verktyg/modellering); mätytorna står i modellens el/matytor.py.

Teckenförklaring

- isolinje, med belysningsstyrkan
- rummets yta i statistiken (utan kantzonen)
- delområde med egen statistik
- armatur

Rev	Avser	Datum	Sign

PROJEKT

Fritidshus Trebodar, Resö, Tanum

FASTIGHET

Resö 2:66, Tanums kommun · BYGG.2025.2278

INNEHÅLL

Ljusplan
Plan 1, golvet


SKALA	FORMAT	DATUM
1:75	A3	2026-11-05
UPPRÄTTAD	GRANSKAD	UNDERLAG
Viktor Ogeman	–	Modellen, rendering
STATUS		REVISION
UTREDNING		**A**

RITNINGSNUMMER

U-04.1

Plan 1, bordshöjd 0,75 m, belysningsstyrka

Skala 1:75

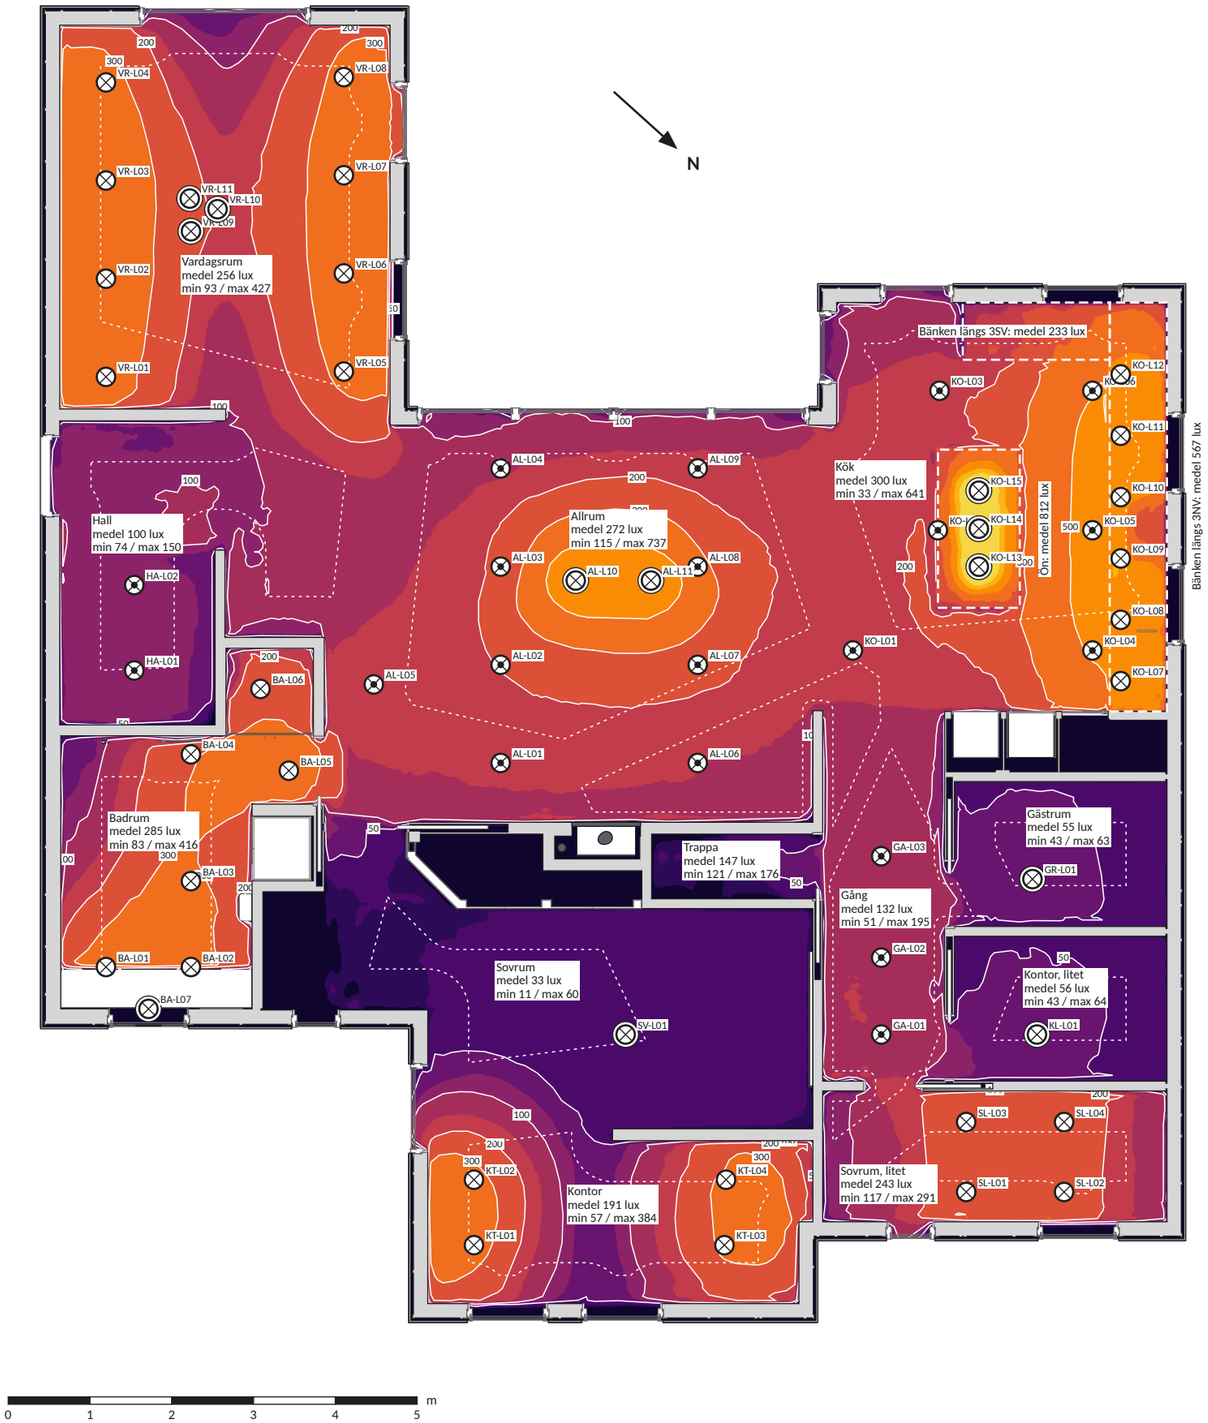

Belysningsstyrka, lux

5 000
2 000
1 000
750
500
300
200
150
100
75
50
20
10
0

Rum och delområden, lux

Rum	Medel	Min	Max	Jämnhet U_0
Allrum	272	115	737	0,42
Badrum	285	83	416	0,29
Bänken längs 3NV (0,91 m)	567	171	778	0,30
Bänken längs 3SV (0,91 m)	233	109	486	0,47
Gästrum	55	43	63	0,77
Gång	132	51	195	0,39
Hall	100	74	150	0,74
Kontor	191	57	384	0,30
Kontor, litet	56	43	64	0,77
Kök	300	33	641	0,11
Sovrum	33	11	60	0,32
Sovrum, litet	243	117	291	0,48
Trappa	147	121	176	0,82
Vardagsrum	256	93	427	0,36
Ön (0,91 m)	812	169	2 086	0,21

Anvisningar

1. Belysningsstyrkan på en vågrät yta 0,75 m över golvet, i rutor om 50 mm, ur renderingen i Blender (Cycles): armaturernas uppmätta ljusfördelning (tillverkarnas fotometrifiler), dagsljuset och reflexerna i rummen. Delområdena Bänken längs 3NV, Bänken längs 3SV och Ön mäts på en vågrät yta 0,91 m över golvet.
2. Tända: AL-T1 Allrum, tubspotar sydost; AL-T2 Allrum, tubspotar nordväst; AL-T3 Allrum, PH 5 över bordet; KO-T1 Kök, tubspotar mot taket; KO-T2 Kök, spotar mot bänken; KO-T3 Kök, Stav över ön; GA-T1 Gång, tubspotar; HA-T1 Hall, tubspotar; VR-T1 Vardagsrum, spotar sydost; VR-T2 Vardagsrum, spotar nordväst; VR-T3 Vardagsrum, VL45; BA-T1 Badrum, spotar; BA-T2 Badrum, lampan över tvättstället; SV-T1 Sovrum, glob; KT-T1 Kontor, spotar mot väggarna; SL-T1 Sovrum litet, spotar mot gaveln; SL-T2 Sovrum litet, spotar mot L1; KL-T1 Kontor litet, glob; GR-T1 Gästrum, glob; KA-T6 Källaren, det stora rummet; KA-T7 Källaren, det lilla rummet väster om KL2; KA-T8 Källaren, det lilla rummet öster om KL2; KA-T1 Källaren, trapphallen; KA-T2 Källaren, tvättstugan; KA-T3 Källaren, rummen norr om V4–V6, västra delen; KA-T4 Källaren, rummen norr om V4–V6, östra delen; KA-T5 Källaren, rummet söder om trapphallen.
3. Inget dagsljus (2026-12-21 kl. 22:00).
4. Statistiken per rum utan en kantzon på 0,5 m längs väggarna (SS-EN 12464-1), i små rum mindre, och utan inredningen på mätytan (skåp, säng, bänkskivor, källartrappan och pelarna, vita på planen); jämnheten U_0 = minsta / medel. Rummen är de slutna ytorna mellan väggarna; en öppen planlösning delas mellan rummens namn.
5. Ritningen ritas med ./mod ljusplan (verktyg/modellering); mätytorna står i modellens el/matytor.py.

Teckenförklaring

- isolinje, med belysningsstyrkan
- rummets yta i statistiken (utan kantzonen)
- delområde med egen statistik
- armatur

Rev	Avser	Datum	Sign

PROJEKT

Fritidshus Trebodar, Resö, Tanum

FASTIGHET

Resö 2:66, Tanums kommun · BYGG.2025.2278

INNEHÅLL

Ljusplan
Plan 1, bordshöjd 0,75 m


SKALA	FORMAT	DATUM
1:75	A3	2026-11-05
UPPRÄTTAD	GRANSKAD	UNDERLAG
Viktor Ogeman	–	Modellen, rendering
STATUS		REVISION
UTREDNING		**A**

RITNINGSNUMMER

U-04.2

Köket, bänkskivorna 0,91 m, belysningsstyrka

Skala 1:50

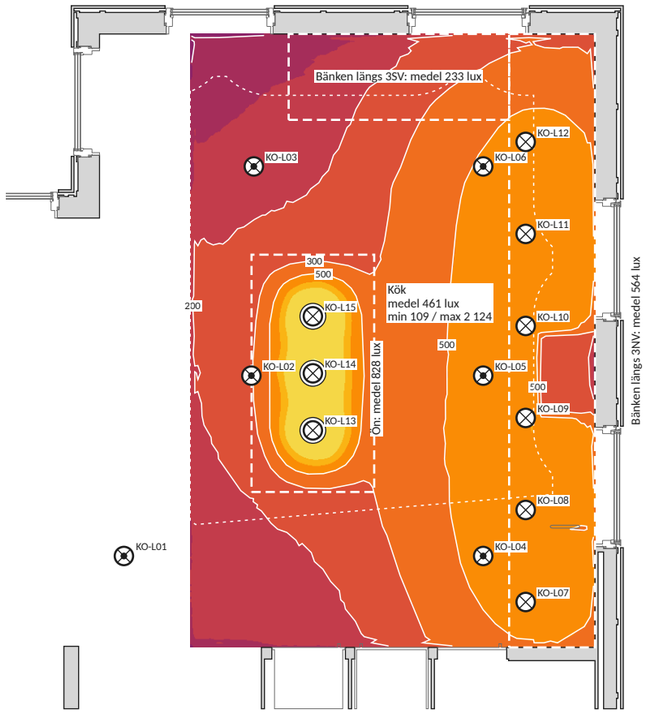

Belysningsstyrka, lux

5 000
2 000
1 000
750
500
300
200
150
100
75
50
20
10
0

Rum och delområden, lux

Rum	Medel	Min	Max	Jämnhet U_o
Bänken längs 3NV	564	133	753	0,24
Bänken längs 3SV	233	111	498	0,48
Kök	461	109	2 124	0,24
Ön	828	206	2 124	0,25

Anvisningar

1. Belysningsstyrkan på en vågrät yta 0,91 m över golvet, i rutor om 25 mm, ur renderingen i Blender (Cycles): armaturernas uppmätta ljusfördelning (tillverkarnas fotometrifiler), dagsljuset och reflexerna i rummen.
2. Tända: AL-T1 Allrum, tubspotar sydost; AL-T2 Allrum, tubspotar nordväst; AL-T3 Allrum, PH 5 över bordet; KO-T1 Kök, tubspotar mot taket; KO-T2 Kök, spotar mot bänken; KO-T3 Kök, Stav över ön; GA-T1 Gång, tubspotar; HA-T1 Hall, tubspotar; VR-T1 Vardagsrum, spotar sydost; VR-T2 Vardagsrum, spotar nordväst; VR-T3 Vardagsrum, VL45; BA-T1 Badrum, spotar; BA-T2 Badrum, lampan över tvättstället; SV-T1 Sovrum, glob; KT-T1 Kontor, spotar mot väggarna; SL-T1 Sovrum litet, spotar mot gaveln; SL-T2 Sovrum litet, spotar mot L1; KL-T1 Kontor litet, glob; GR-T1 Gästrum, glob; KA-T6 Källaren, det stora rummet; KA-T7 Källaren, det lilla rummet väster om KL2; KA-T8 Källaren, det lilla rummet öster om KL2; KA-T1 Källaren, trapphallen; KA-T2 Källaren, tvättstugan; KA-T3 Källaren, rummen norr om V4–V6, västra delen; KA-T4 Källaren, rummen norr om V4–V6, östra delen; KA-T5 Källaren, rummet söder om trapphallen.
3. Inget dagsljus (2026-12-21 kl. 22:00).
4. Statistiken per rum utan en kantzon på 0,5 m längs väggarna (SS-EN 12464-1), i små rum mindre, och utan inredningen på mätytan (skåp, säng, bänkskivor, källartrappan och pelarna, vita på planen); jämnheten U_o = minsta / medel. Rummen är de slutna ytorna mellan väggarna; en öppen planlösning delas mellan rummens namn.
5. Ritningen ritas med ./mod ljusplan (verktyg/modellering); mätytorna står i modellens el/matytor.py.

Teckenförklaring

- isolinje, med belysningsstyrkan
- rummets yta i statistiken (utan kantzonen)
- delområde med egen statistik
- armatur

Rev	Avser	Datum	Sign

PROJEKT

Fritidshus Trebodar, Resö, Tanum

FASTIGHET

Resö 2:66, Tanums kommun · BYGG.2025.2278

INNEHÅLL

Ljusplan
Köket, bänkskivorna 0,91 m

SKALA	FORMAT	DATUM
1:50	A3	2026-11-05

UPPRÄTTAD	GRANSKAD	UNDERLAG
Viktor Ogeman	–	Modellen, rendering


STATUS	REVISION
UTREDNING	**A**

RITNINGSNUMMER

U-04.3

Källaren, golvet, belysningsstyrka

Skala 1:75

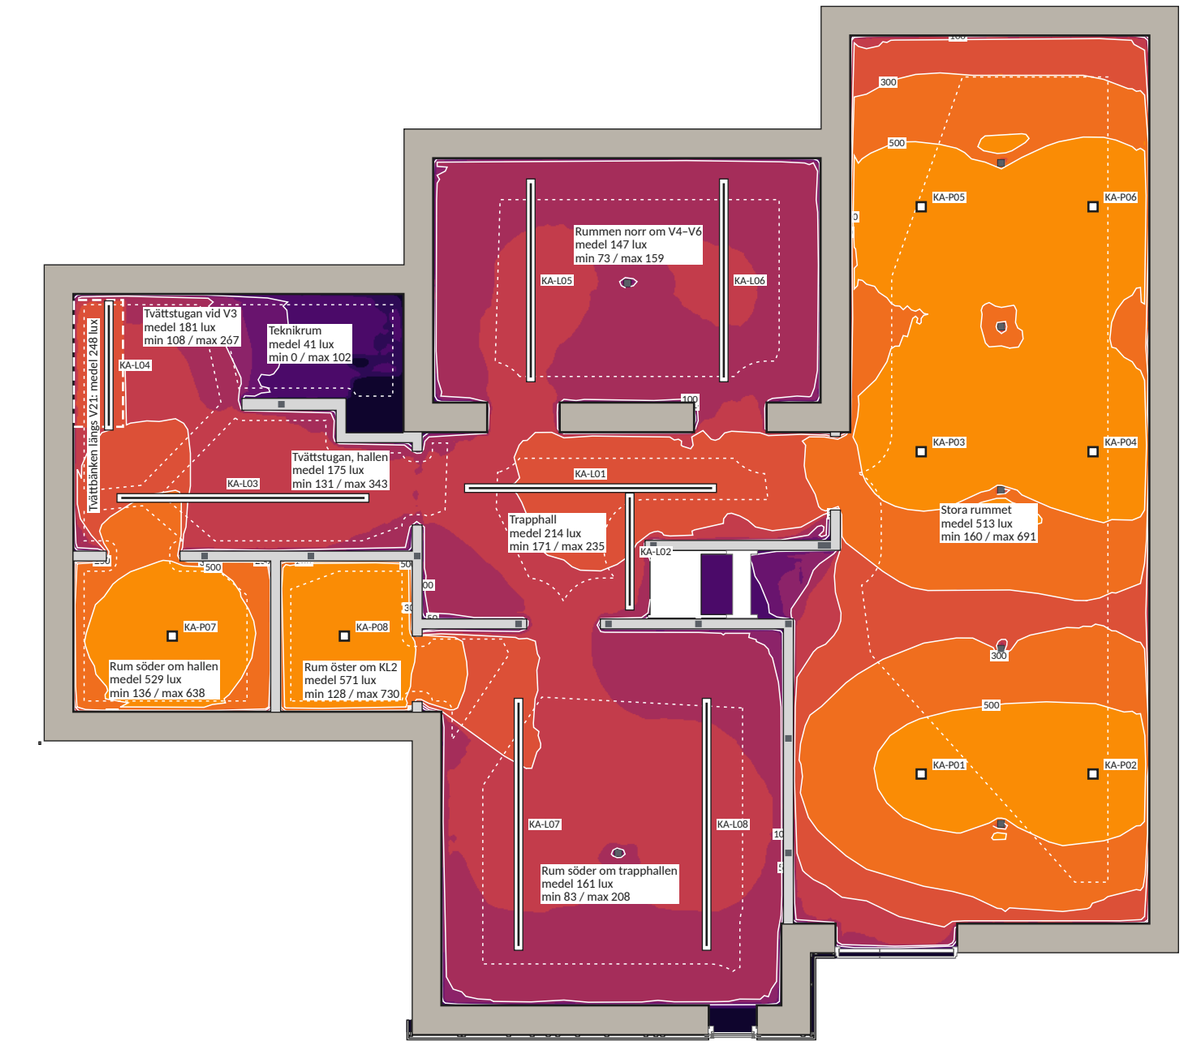

Belysningsstyrka, lux

5 000
2 000
1 000
750
500
300
200
150
100
75
50
20
10
0

Rum och delområden, lux

Rum	Medel	Min	Max	Jämnhet U_0
Rum söder om hallen	529	136	638	0,26
Rum söder om trapphallen	161	83	208	0,52
Rum öster om KL2	571	128	730	0,22
Rummen norr om V4–V6	147	73	159	0,50
Stora rummet	513	160	691	0,31
Teknikrum	41	0	102	0,00
Trapphall	214	171	235	0,80
Tvättbänken längs V21 (0,90 m)	248	150	294	0,61
Tvättstugan vid V3	181	108	267	0,60
Tvättstugan, hallen	175	131	343	0,75

Anvisningar

1. Belysningsstyrkan på golvet, i rutor om 50 mm, ur renderingen i Blender (Cycles): armaturernas uppmätta ljusfördelning (tillverkarnas fotometrifiler), dagsljuset och reflexerna i rummen. Ljuslinjerna lyser som lambertska ytor (den opala diffusorn) med det antagna ljusflödet per meter lysande längd. Delområdet Tvättbänken längs V21 mäts på en vågrät yta 0,90 m över golvet.
2. Tända: AL-T1 Allrum, tubspotar sydost; AL-T2 Allrum, tubspotar nordväst; AL-T3 Allrum, PH 5 över bordet; KO-T1 Kök, tubspotar mot taket; KO-T2 Kök, spotar mot bänken; KO-T3 Kök, Stav över ön; GA-T1 Gång, tubspotar; HA-T1 Hall, tubspotar; VR-T1 Vardagsrum, spotar sydost; VR-T2 Vardagsrum, spotar nordväst; VR-T3 Vardagsrum, VL45; BA-T1 Badrum, spotar; BA-T2 Badrum, lampan över tvättstället; SV-T1 Sovrum, glob; KT-T1 Kontor, spotar mot väggarna; SL-T1 Sovrum litet, spotar mot gaveln; SL-T2 Sovrum litet, spotar mot L1; KL-T1 Kontor litet, glob; GR-T1 Gästrum, glob; KA-T6 Källaren, det stora rummet; KA-T7 Källaren, det lilla rummet väster om KL2; KA-T8 Källaren, det lilla rummet öster om KL2; KA-T1 Källaren, trapphallen; KA-T2 Källaren, tvättstugan; KA-T3 Källaren, rummen norr om V4–V6, västra delen; KA-T4 Källaren, rummen norr om V4–V6, östra delen; KA-T5 Källaren, rummet söder om trapphallen.
3. Inget dagsljus (2026-12-21 kl. 22:00).
4. Statistiken per rum utan en kantzon på 0,5 m längs väggarna (SS-EN 12464-1), i små rum mindre, och utan inredningen på mätytan (skåp, säng, bänkskivor, källartrappan och pelarna, vita på planen); jämnheten U_0 = minsta / medel. Rummen är de slutna ytorna mellan väggarna; en öppen planlösning delas mellan rummens namn.
5. Ritningen ritas med ./mod ljusplan (verktyg/modellering); mätytorna står i modellens el/matytor.py.

Teckenförklaring

- isolinje, med belysningsstyrkan
- rummets yta i statistiken (utan kantzonen)
- delområde med egen statistik
- armatur
- ljuslinje, i sin längd

Rev	Avser	Datum	Sign

PROJEKT

Fritidshus Trebodar, Resö, Tanum

FASTIGHET

Resö 2:66, Tanums kommun · BYGG.2025.2278

INNEHÅLL

Ljusplan
Källaren, golvet

SKALA	FORMAT	DATUM
1:75	A3	2026-11-05

UPPRÄTTAD	GRANSKAD	UNDERLAG
Viktor Ogeman	–	Modellen, rendering

STATUS	REVISION
UTREDNING	**A**

RITNINGSNUMMER

U-04.4