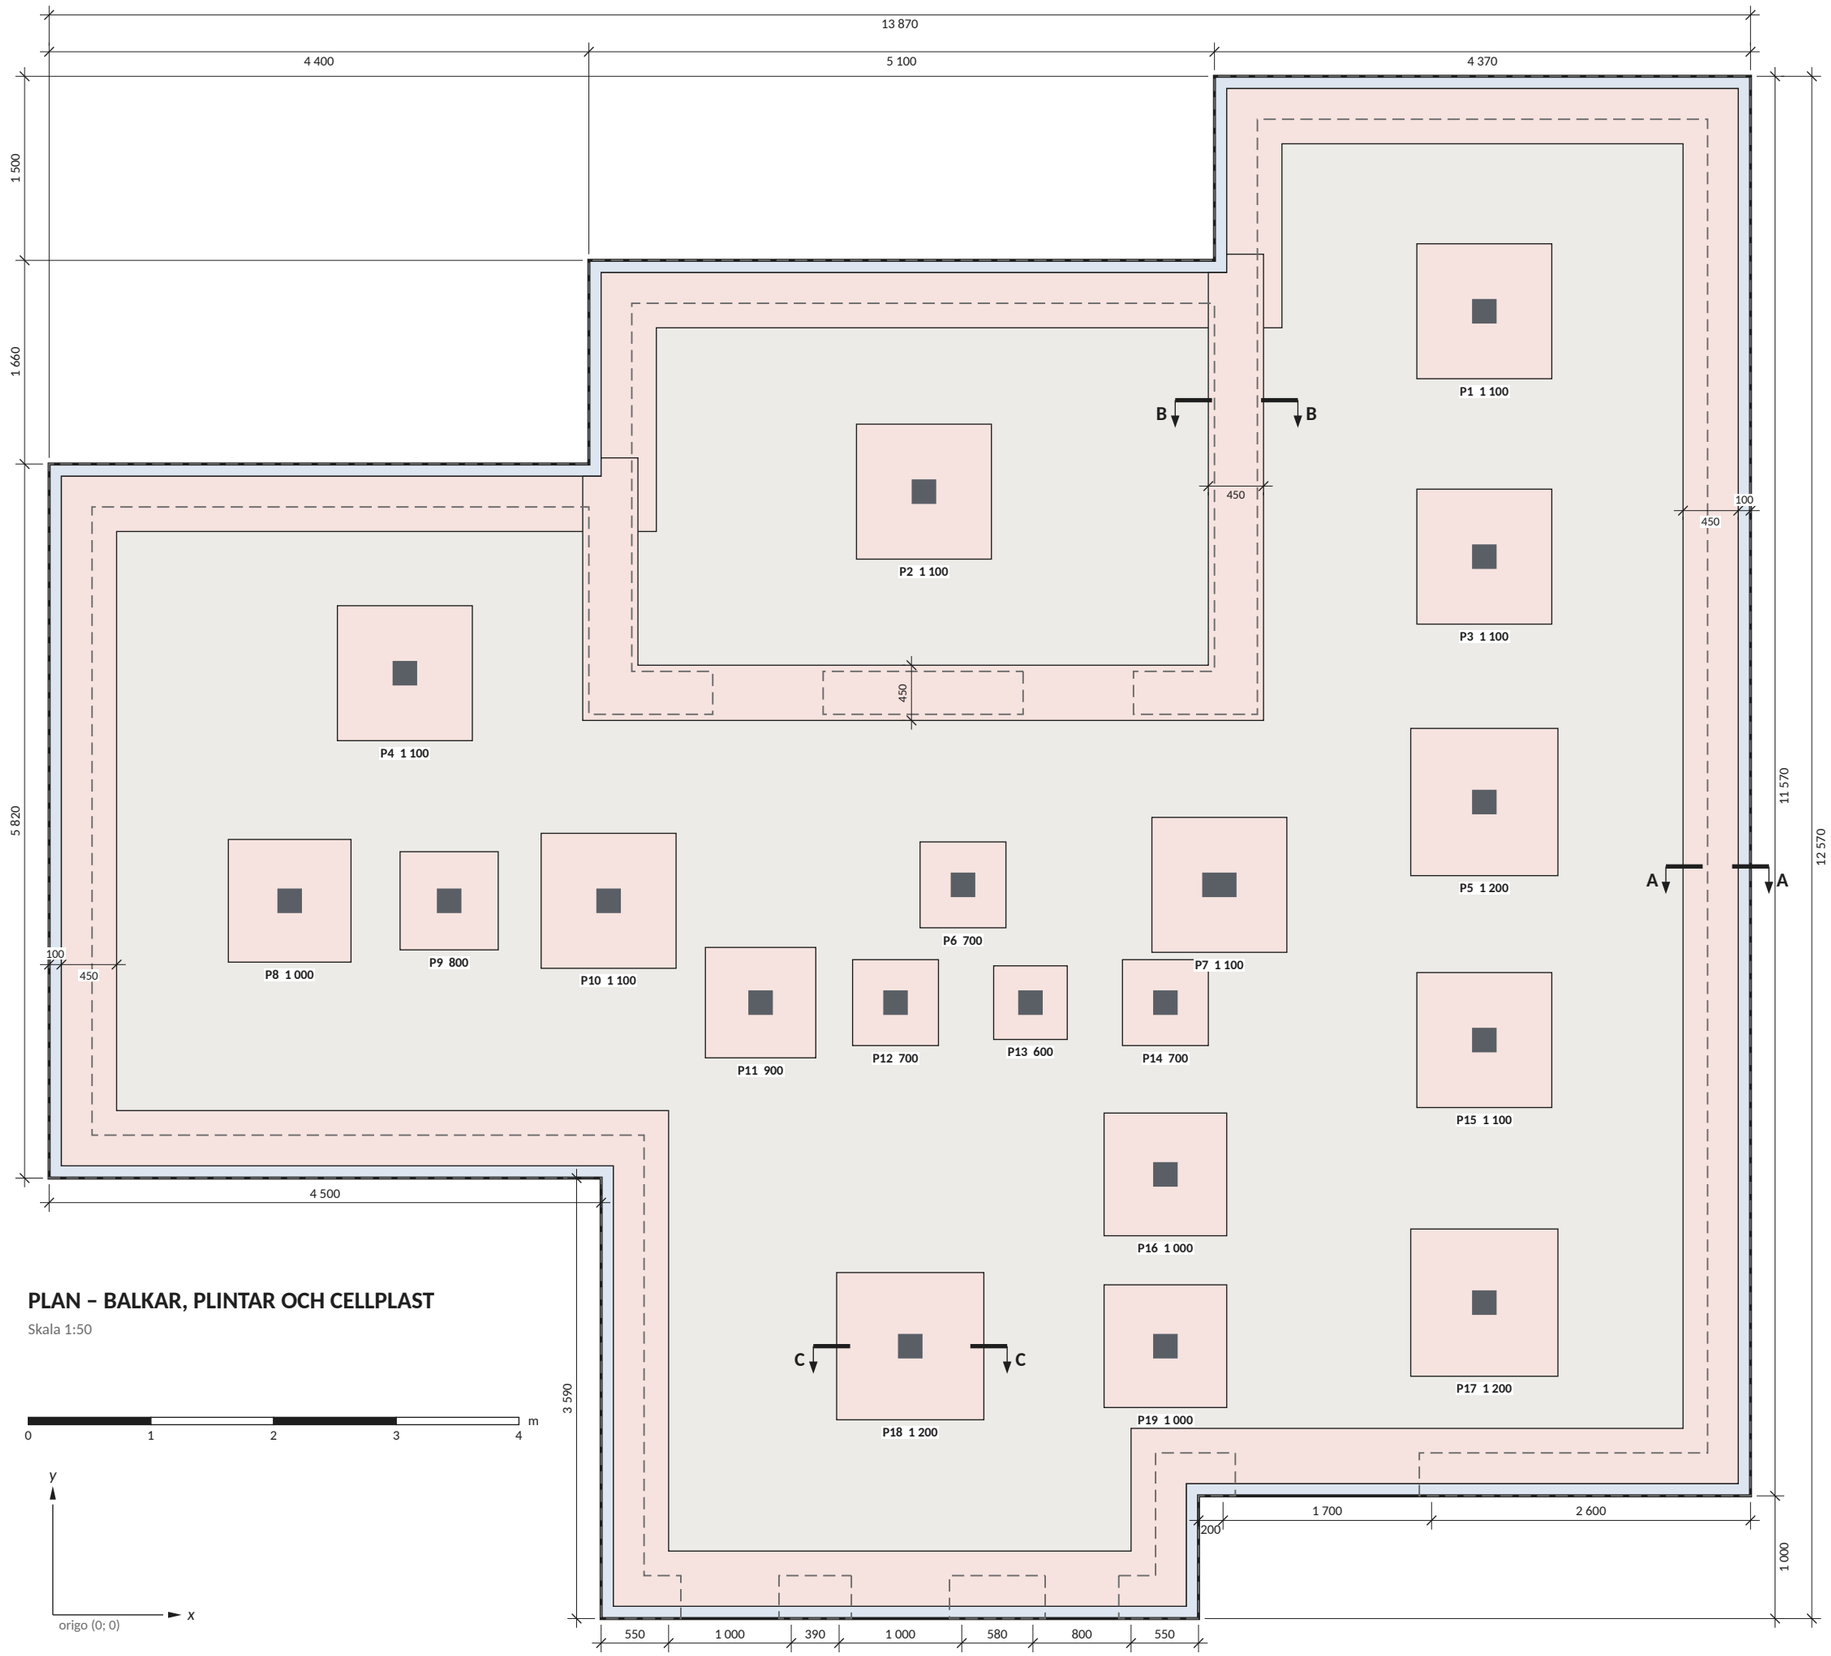


PLAN – BALKAR, PLINTAR OCH CELLPLAST

Skala 1:50

Anvisningar

1. Bottenplatta L300 (K-06): 100 mm betong C25/30 på 200 mm cellplast S100 i två skikt med åldringsbeständig plastfolie emellan. Kantbalkar 450 × 200 i L-element L300 med fot av S300 längs hela kanten; balkar under innerväggarna 450 × 200 och plintar under rören, lika höga, på 100 mm S300. Bara två kvaliteter: S100 under plattan och S300 under balkar och plintar. Samma uppbyggnad i hela källaren.
2. L-elementens ytterkant ligger i väggarnas ytterliv (R-04.1), som planens mått går till. Betongen börjar innanför L-elementets yttre ben, 100 mm, i kärnans yttre yta: väggens yttre cellplast står på benet och kärnan på kantbalken (detalj D, sektion A). Koordinater i mm enligt K-05, höjder från bottenplattans överkant.
3. Plintarna är kvadratiska och centrerade under rörets mitt (P7: mitt mellan de två rören). Sida och mitt enligt tabellen; mått från väggarna till rörens mitt på R-04.1.
4. Underlag: makadam på sprängt berg, avjämnat och packat. Dränledningen läggs runt huset innan cellplasten läggs (K-06).
5. Armering R-05.2, sektioner och förteckningar R-05.3. Fotplåtar och rör R-04.5.

Teckenförklaring

- kantbalk, balk och plint, 200 hög, på 100 S300
- platta 100 på 200 S100
- L-elementets yttre ben, 100, i väggarnas ytterliv
- väggarna (R-04)
- fotplåt (R-04.5)

Plintar (sida och mitt)

Plint	Sida	x	y	Anm
P1	1 100	11 670	10 625	
P2	1 100	7 102	9 155	
P3	1 100	11 670	8 625	
P4	1 100	2 870	7 675	
P5	1 200	11 670	6 625	
P6	700	7 420	5 950	
P7	1 100	9 510	5 950	två rör, fotplåt 280 × 200 eller 2 st 140 × 200 (R-04.5)
P8	1 000	1 931	5 820	
P9	800	3 231	5 820	
P10	1 100	4 531	5 820	
P11	900	5 770	4 990	
P12	700	6 870	4 990	
P13	600	7 970	4 990	
P14	700	9 070	4 990	
P15	1 100	11 670	4 685	
P16	1 000	9 070	3 590	
P17	1 200	11 670	2 545	
P18	1 200	6 990	2 190	
P19	1 000	9 070	2 190	

Ritningsförteckning R-05

Ritning	Innehåll	Skala
R-05.1	Plan, balkar, plintar och cellplast	1:50
R-05.2	Armering	1:50
R-05.3	Sektioner, detaljer och förteckningar	1:10, 1:20, 1:50

Rev	Avser	Datum	Sign
A	Första utgåvan	2026-10-16	VO

PROJEKT

Fritidshus Trebodar, Resö, Tanum

FASTIGHET

Resö 2:66, Tanums kommun · BYGG.2025.2278


INNEHÅLL

Bottenplatta
Plan, balkar, plintar och cellplast

SKALA	FORMAT	DATUM
1:50	A3	2026-10-16
UPPRÄTTAD	GRANSKAD	UNDERLAG
Viktor Ogeman	–	K-06 rev A, K-05 rev A
STATUS		REVISION
KONSTRUKTION		**A**

RITNINGSNUMMER

R-05.1

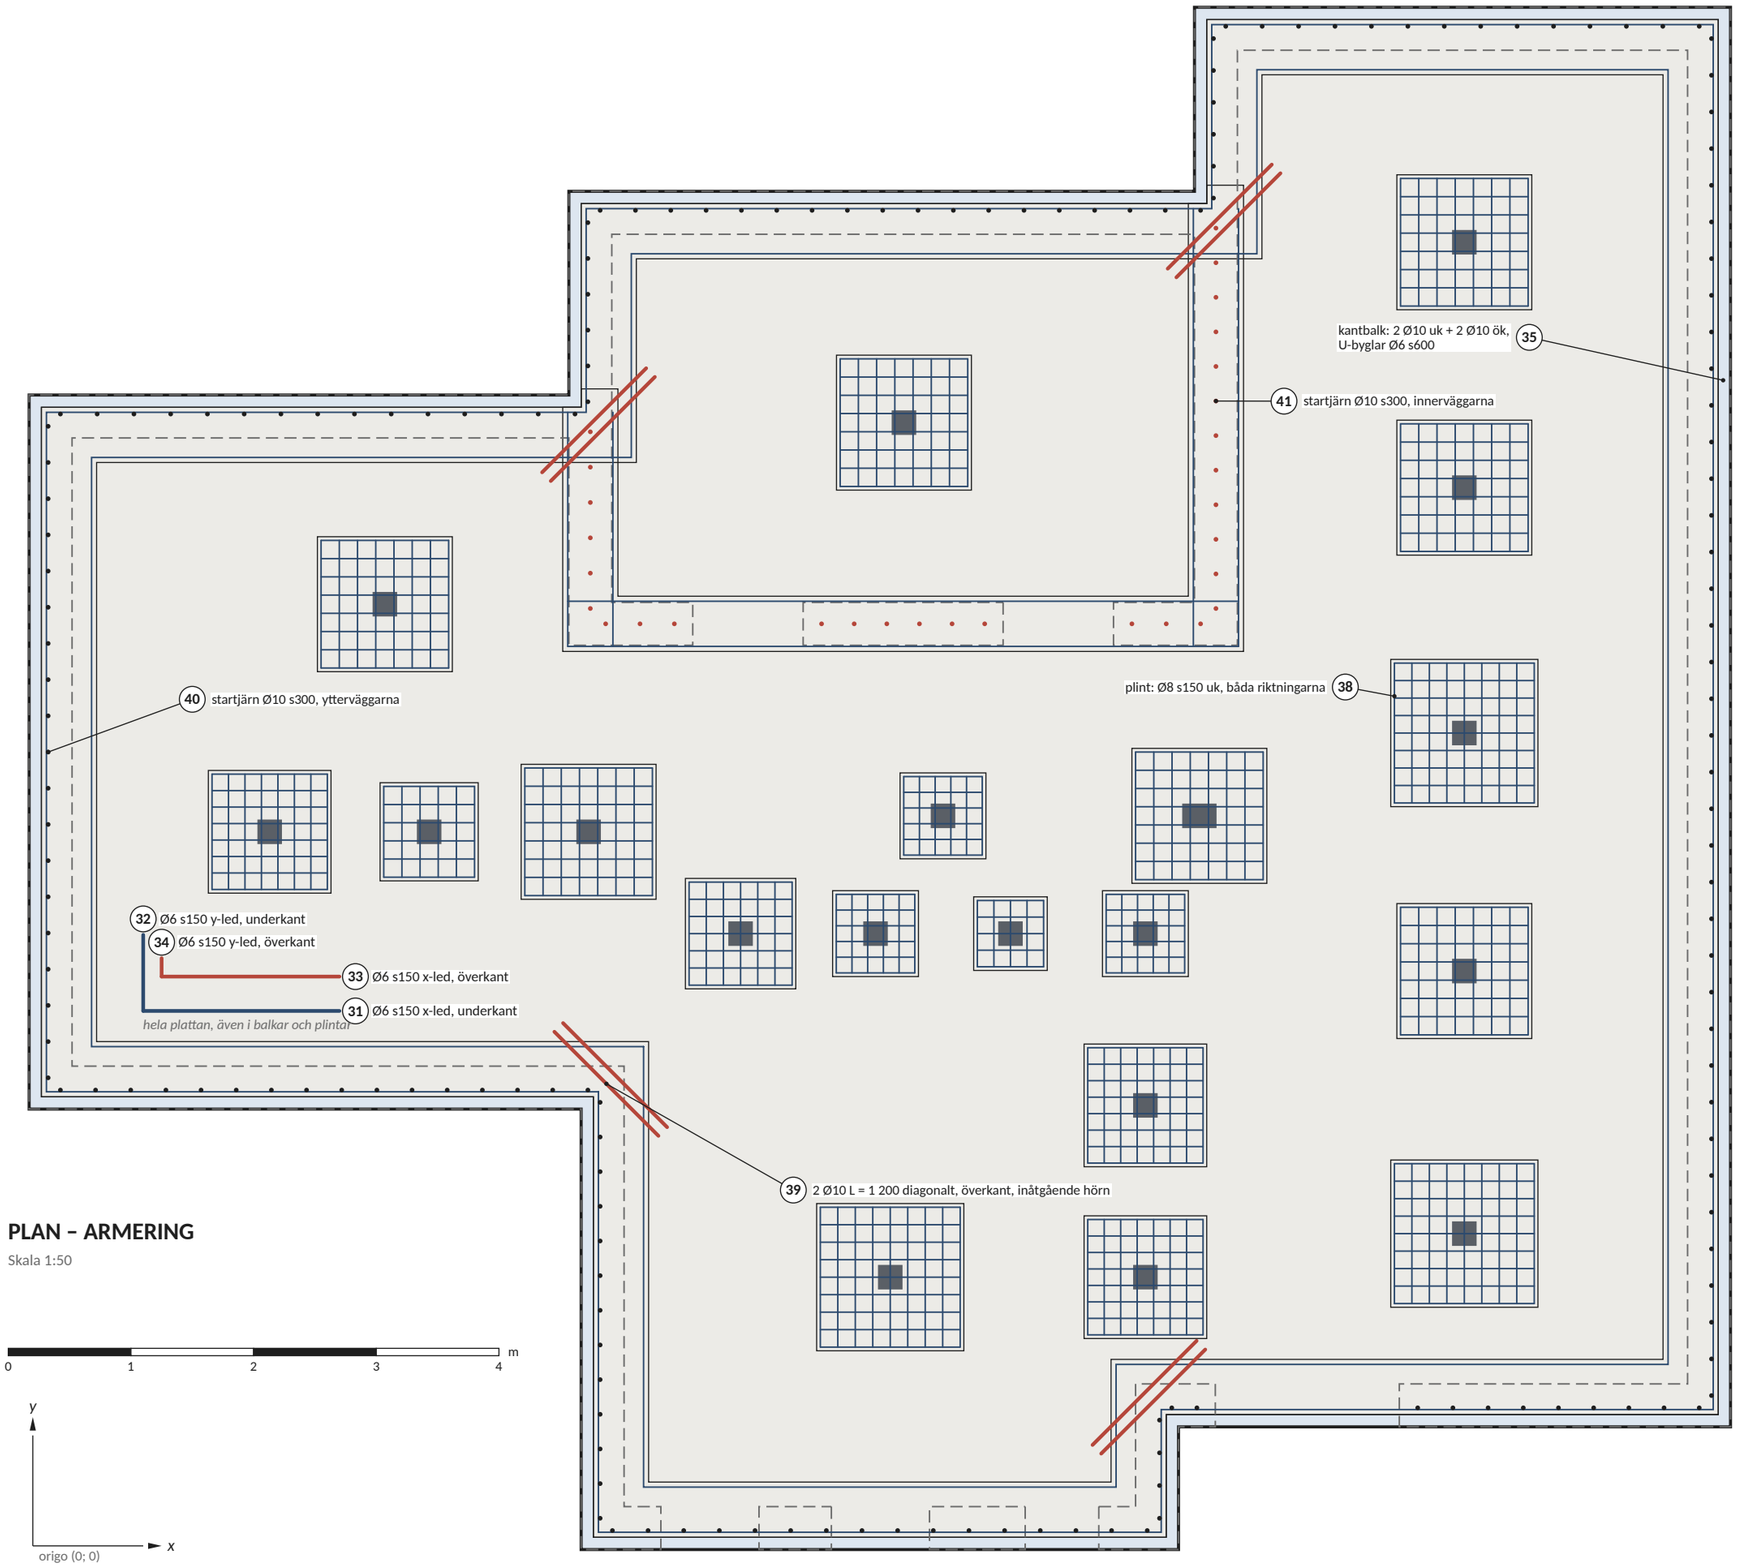

PLAN – ARMERING

Skala 1:50

Anvisningar

1. Betong C25/30, armering B500B. Täckande skikt: 30 mm mot cellplasten (distanser) och 25 mm i överkant.
2. Nät Ø6 s150 i under- och överkant i hela plattan (31–34), också genom balkarna och plintarna. Golvvärmeslangarna fästs i underkantsnätet. Skarvlängd Ø6 400.
3. Kantbalkar och balkar under innerväggarna: 2 Ø10 i underkant (35) på byglarna och 2 Ø10 i överkant (36) under överkantsnätet, U-byglar Ø6 s600 (37). Skarvlängd Ø10 650; i hörnen bockas järnen eller skarvas med vinkeljärn. Innerbalkarnas järn förs in i kantbalken och i den korsande balken.
4. Plintar: Ø8 s150 i underkant, båda riktningarna (38). Fotplåten gjuts in kant i kant med plintens överkant (R-04.5); näten läggs fritt från svetsbultarna.
5. Inåtgående hörn: 2 Ø10, L = 1 200, i överkant diagonalt, 150 och 250 mm från hörnet (39).
6. Startjärn Ø10 s300, 1 200 upp och 500 i balken: den lodräta delen och foten, 330, på byglarna. Ytterväggarna på utsidan (40, svarta), med foten vinkelrätt in i kantbalken (Sundolitt), också under bröstningarna vid F1–F3; innerväggarna i kärnans mitt (41, röda), med foten längs balken. Väggarnas armering: R-04.
7. Ytan under väggarna ruggas före väggarnas gjutning (K-06).

Teckenförklaring

- armering i underkant / balkjärn
- armering i överkant (diagonaljärn)
- startjärn, ytterväggarna
- startjärn, innerväggarna
- (31) positionsnummer (stålförteckning R-05.3)

Rev	Avser	Datum	Sign
A	Första utgåvan	2026-10-16	VO

PROJEKT

Fritidshus Trebodar, Resö, Tanum

FASTIGHET

Resö 2:66, Tanums kommun · BYGG.2025.2278


INNEHÅLL

Bottenplatta
Armering

SKALA	FORMAT	DATUM
1:50	A3	2026-10-16
UPPRÄTTAD	GRANSKAD	UNDERLAG
Viktor Ogeman	–	K-06 rev A, K-05 rev A
STATUS		REVISION
KONSTRUKTION		**A**


RITNINGSNUMMER

R-05.2

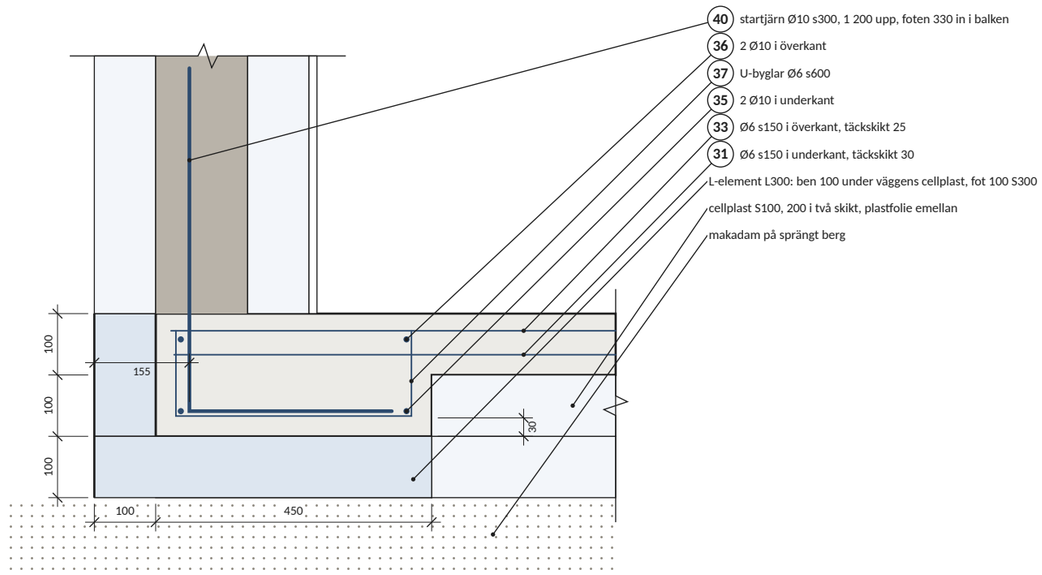


SEKTION A–A Kantbalk i L-element (V14)

Skala 1:10

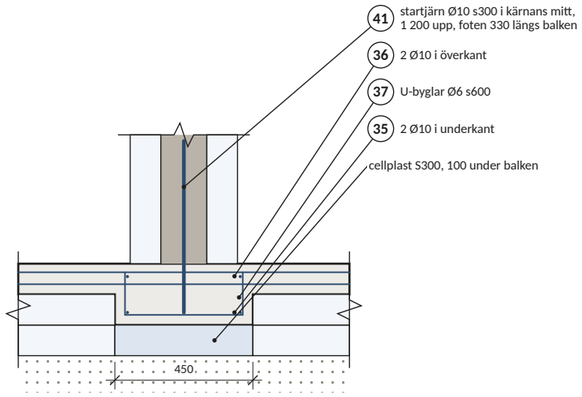


SEKTION B–B Balk under innervägg (V15)

Skala 1:20

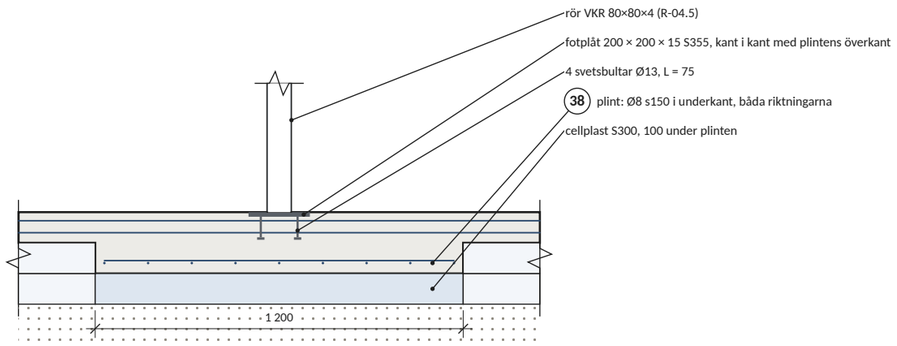

SEKTION C–C Plint under rör (P18, 1 200)

Skala 1:20

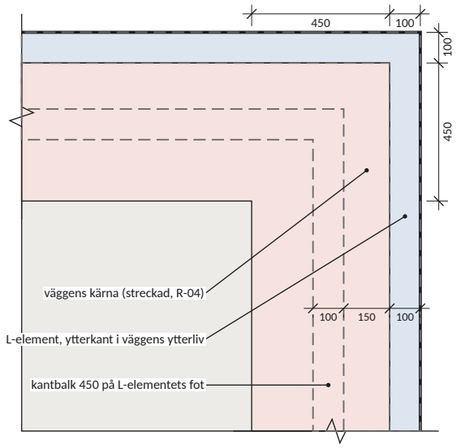

DETALJ D Yttre hörn i plan (V1/V14)

Skala 1:20

Samma vid alla hörn: L-elementets ytterkant i väggens ytterliv.

Anvisningar

1. Utförande (K-06): spräng och avjämna berget och lägg makadam. Lägg dränledningen. Lägg L-elementen (fot S300) med ytterkanten i väggarnas ytterliv, S300 under innerbalkarna och plintarna och S100 under plattan i två skikt med plastfolie emellan. Skär ur cellplasten för balkar och plintar.
2. Armera, lägg golvvärmeslangarna och fixera fotplåtarna i läge och höjd. Gjut bottenplattan med balkar och plintar i en gjutning; fotplåtarna gjuts in kant i kant med plintarnas överkant. Rugga ytan under väggarna.
3. Kontrollera före gjutning: armeringens läge och täckskikt (distanser), plintarnas läge och storlek, fotplåtarnas läge och höjd (±5 mm), startjärnen.
4. Plattan behöver inga fogar; golvbeläggning och tätskikt ska tåla krympsprickor (K-06).
5. Plan R-05.1, armering R-05.2.

Teckenförklaring

- betong C25/30
- cellplast S100
- L-element (fot S300), S300 under balkar och plintar
- väggens betongkärna (R-04)
- armering

Cellplast

	Utförande	Mängd	Anm
S100	2 × 100 mm, plastfolie emellan	81,0 m²	under plattan
S300	100 mm	23,3 m²	under innerbalkarna och plintarna
L-element	L300, 550 × 300, ben 100, fot S300	52,9 m	längs hela kanten, ytterkant i väggarnas ytterliv

Stålförteckning, B500B

Pos	Ø	Form	s	Antal	L (mm)	Total (m)	Vikt (kg)	Anm
31	Ø6	rak	s150	82	var.	848	188	UK x-led, hela plattan
32	Ø6	rak	s150	91	var.	840	186	UK y-led, hela plattan
33	Ø6	rak	s150	82	var.	848	188	ÖK x-led, hela plattan
34	Ø6	rak	s150	91	var.	840	186	ÖK y-led, hela plattan
35	Ø10	rak	–	2 per balk	var.	129	80	balkar, underkant
36	Ø10	rak	–	2 per balk	var.	129	80	balkar, överkant
37	Ø6	U 145+390+145	s600	102	700	71	16	byglar i balkarna
38	Ø8	rak	s150	286	var.	272	108	plintar, underkant
39	Ø10	rak	–	8	1 200	10	6	inåtgående hörn, ÖK
40	Ø10	L 1 360+330	s300	176	1 690	297	184	ytterväggarna, utsidan
41	Ø10	L 1 360+330	s300	30	1 690	51	31	innerväggarna, mitt
						Summa	1 253	Ø6: 765 + Ø8: 108 + Ø10: 380

Rev	Avser	Datum	Sign
A	Första utgåvan	2026-10-16	VO

PROJEKT

Fritidshus Trebodar, Resö, Tanum

FASTIGHET

Resö 2:66, Tanums kommun · BYGG.2025.2278

INNEHÅLL

Bottenplatta
Sektioner, detaljer och förteckningar

SKALA	FORMAT	DATUM
1:10, 1:20, 1:50	A3	2026-10-16
UPPRÄTTAD: Viktor Ogeman	GRANSKAD: –	UNDERLAG: K-06 rev A, K-05 rev A
STATUS: **KONSTRUKTION**		REVISION: **A**

RITNINGSNUMMER

R-05.3