

Plan, utsättningspunkter

Skala 1:100

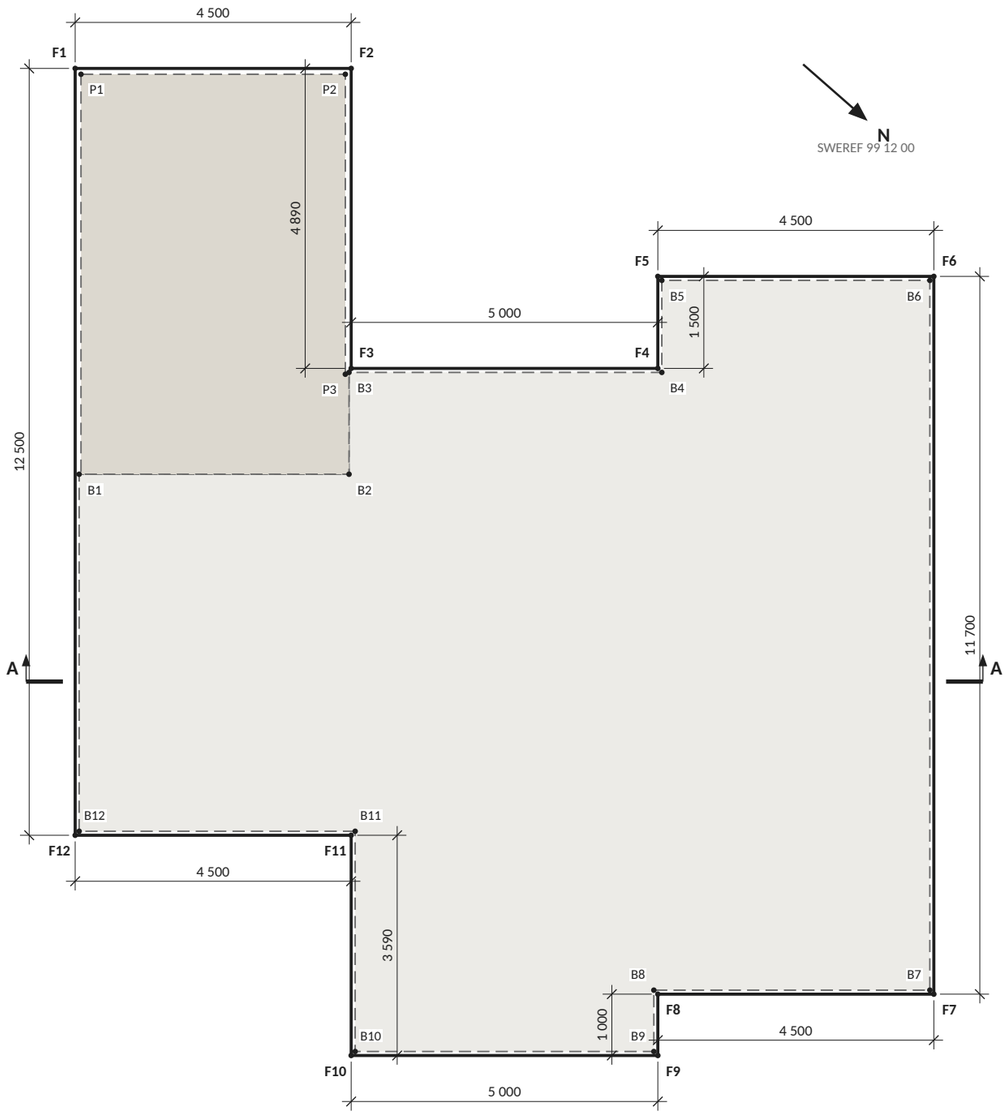

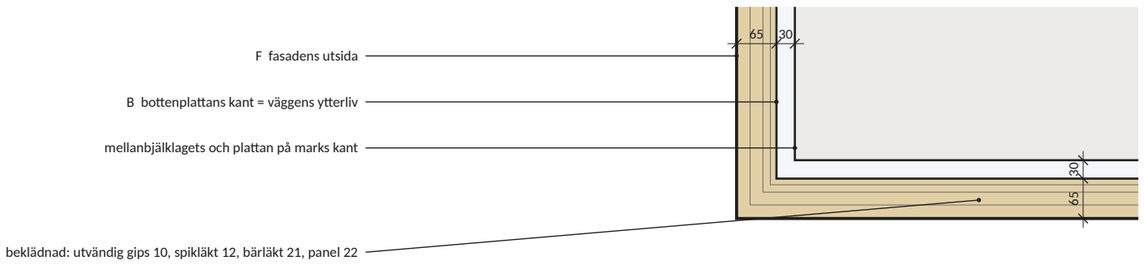

Utsättningspunkter, SWEREF 99 12 00

x, y i mm (K-05), N, E i m.

Fasadens utsida (F)

Punkt	x	y	N	E
F1	−95	15 995	6 520 154,563	102 360,041
F2	4 405	15 995	6 520 157,947	102 357,075
F3	4 405	11 105	6 520 161,170	102 360,752
F4	9 405	11 105	6 520 164,930	102 357,457
F5	9 405	12 605	6 520 163,941	102 356,329
F6	13 905	12 605	6 520 167,326	102 353,362
F7	13 905	905	6 520 175,037	102 362,161
F8	9 405	905	6 520 171,653	102 365,127
F9	9 405	−95	6 520 172,312	102 365,879
F10	4 405	−95	6 520 168,552	102 369,175
F11	4 405	3 495	6 520 166,186	102 366,475
F12	−95	3 495	6 520 162,802	102 369,441

Bottenplattans kant (B)

Punkt	x	y	N	E
B1	−30	9 380	6 520 158,972	102 364,973
B2	4 370	9 380	6 520 162,281	102 362,073
B3	4 370	11 040	6 520 161,187	102 360,824
B4	9 470	11 040	6 520 165,022	102 357,463
B5	9 470	12 540	6 520 164,033	102 356,335
B6	13 840	12 540	6 520 167,320	102 353,454
B7	13 840	970	6 520 174,946	102 362,155
B8	9 340	970	6 520 171,562	102 365,121
B9	9 340	−30	6 520 172,221	102 365,873
B10	4 470	−30	6 520 168,558	102 369,083
B11	4 470	3 560	6 520 166,192	102 366,383
B12	−30	3 560	6 520 162,808	102 369,350

Plattan på marks kant (P)

Punkt	x	y	N	E
P1	0	15 900	6 520 154,697	102 360,050
P2	4 310	15 900	6 520 157,938	102 357,209
P3	4 310	11 010	6 520 161,161	102 360,886

Detalj 1, hörnet F12/B12

Skala 1:10

lika runt huset

Anvisningar

1. Koordinater i SWEREF 99 12 00 (Tanums kommun), höjder i RH2000 (AR-02.2). Mått i mm. x, y är husets koordinater i K-05, med origo i mellanbjälklagets kanter.
2. Utstakning och lägeskontroll görs av certifierad mättekniker (krav i bygglovet BYGG.2025.2278).
3. Läget är passat mot bygglovets situationsplan (ritning 200): husets kontur är vriden och flyttad så att den täcker husets yta i planen. Läget är därför inte noggrannare än situationsplanen, cirka ±0,1 m. Måtten mellan punkterna är exakta. Kontrollera läget mot den reviderade situationsplanen före utstakningen.
4. E = E0 + (x cos θ − y sin θ)/1 000, N = N0 + (x sin θ + y cos θ)/1 000, med θ = 131,2336°, E0 = 102 372,007, N0 = 6 520 165,177.
5. Fasadens utsida (F) ligger 95 mm utanför mellanbjälklagets kant runt hela huset, även på gavlarna: regeln 30 och beklädnaden 65 (detalj 1). Fasadstenen på källarväggarna har sin framsida i samma liv (AR-01). Måtten över regelstommen är 130 mm mindre än fasadens.
6. Bottenplattans kant (B) ligger i källarväggarnas ytterliv, 65 mm innanför fasaden. B1–B3 är plattans kant mot plattan på mark, under källarväggarna V3 och V20.
7. Plattan på mark (P, tillbyggnaden) har sin kant i mellanbjälklagets kant, 95 mm innanför fasaden. Den ansluter till källarväggarna mot B1–B3.

Teckenförklaring

- fasadens utsida (F)
- bottenplattan (B), källaren
- plattan på mark (P)
- • utsättningspunkt

Rev	Avser	Datum	Sign
A	Första utgåvan	2026-10-31	VO

PROJEKT

Fritidshus Trebodar, Resö, Tanum

FASTIGHET

Resö 2:66, Tanums kommun · BYGG.2025.2278

INNEHÅLL

Utsättning
Plan och koordinater


SKALA	FORMAT	DATUM
1:100, 1:10	A3	2026-10-31
UPPRÄTTAD	GRANSKAD	UNDERLAG
Viktor Ogeman	–	Bygglov, K-05, R-05
STATUS		REVISION
KONSTRUKTION		**A**

RITNINGSNUMMER

AR-02.1

Sektion A–A, y = 6 000 (princip)

Skala 1:50

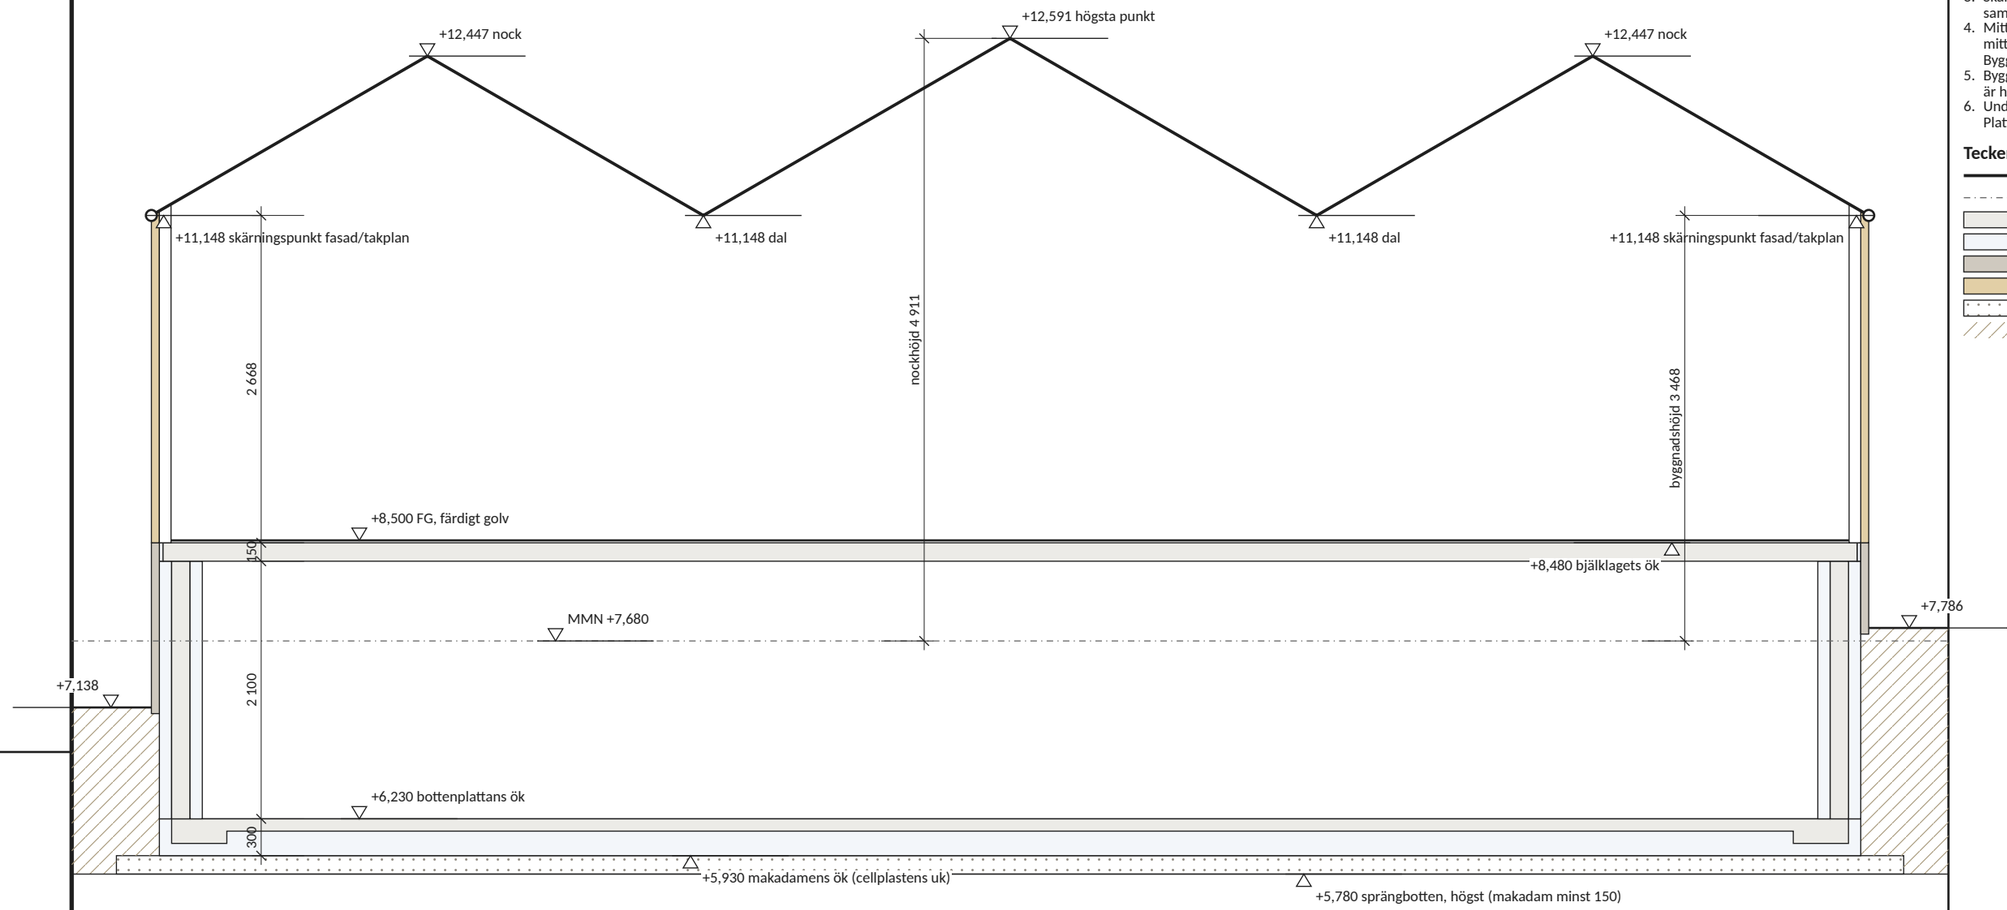

Anvisningar

1. Höjder i RH2000 (m), mått i mm. Sektionen är en principskiss: takets uppbyggnad, takfoten och stommen visas inte. Snittets läge: AR-02.1.
2. FG +8,500 är färdigt golv på plan 1. Mellanbjälklagets överkant ligger 20 mm lägre (golvet).
3. Skärningspunkten mellan fasadens utsida och takplanets ovansida ligger på samma höjd runt hela huset och i dalarna. Taklutning 30°.
4. Mittenbyggnaden är 5 000 mm bred och sidobyggnaderna 4 500 mm, så mittenbyggnadens nock blir 144 mm högre än sidobyggnadernas. Bygglovets nockhöjd (4 766) är sidobyggnadernas.
5. Byggnadshöjden mäts från MMN vid den nordvästra fasaden, där marken är högst (+7,786).
6. Under plattan: minst 150 mm makadam på sprängt och avjämnat berg. Plattans cellplast ligger direkt på makadamen.

Teckenförklaring

- takplanets ovansida
- MMN
- betong
- cellplast
- fasadsten (AR-01)
- beklädnad, plan 1
- makadam
- mark

Höjder, RH2000

Nivå	RH2000 (m)	Underlag
Högsta punkt, mittenbyggnadens nock	+12,591	skärningspunkten + 2 500 · tan 30°; 4 911 över MMN
Sidobyggnadernas nock	+12,447	skärningspunkten + 2 250 · tan 30°; bygglovets nockhöjd 4 766 över MMN (+12,446)
Skärningspunkt fasad/takplan, takfot och dalar	+11,148	MMN + byggnadshöjd 3 468 (bygglov), nordvästra fasaden
FG, färdigt golv plan 1	+8,500	bygglov
Mellanbjälklagets överkant	+8,480	FG – golv 20
Ny mark, nordvästra fasaden	+7,786	bygglov (sektion E)
MMN, medelmarknivå	+7,680	bygglov
Ny mark, sydöstra fasaden	+7,138	bygglov (sektion E)
Bottenplattans överkant, golv i källaren	+6,230	bjälklagets uk – 2 100 (K-06); bygglovet anger +6,3
Makadamens överkant, cellplastens underkant	+5,930	– platta 100 – cellplast 200 (R-04)
Sprängbotten, högst	+5,780	makadam minst 150 (U-01)

Rev	Avser	Datum	Sign
A	Första utgåvan	2026-10-31	VO

PROJEKT

Fritidshus Trebodar, Resö, Tanum

FASTIGHET

Resö 2:66, Tanums kommun · BYGG.2025.2278

INNEHÅLL

Utsättning
Sektion och höjder

SKALA	FORMAT	DATUM
1:50	A3	2026-10-31
UPPRÄTTAD	GRANSKAD	UNDERLAG
Viktor Ogeman	–	Bygglov, K-05, R-05
STATUS		REVISION
KONSTRUKTION		**A**

RITNINGSNUMMER

AR-02.2