
Plan, utsättningspunkter

Skala 1:100

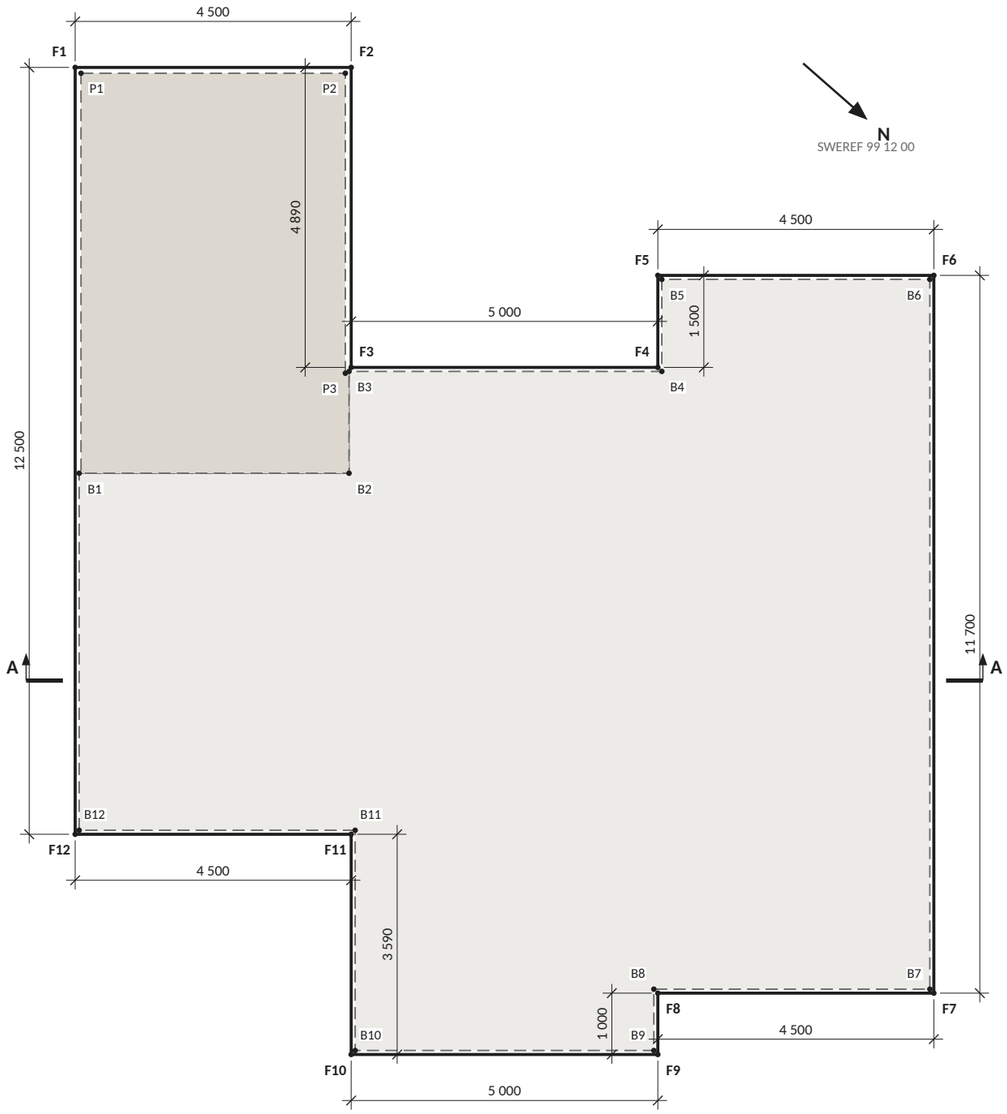

Utsättningspunkter, SWEREF 99 12 00

x, y i mm (K-05), N, E och höjder i m. Höjder i RH2000 och relativt fixpunkten FIX (+7,760).

Fasadens utsida (F)

Punkt	x	y	N	E
F1	−95	15 995	6 520 154,563	102 360,041
F2	4 405	15 995	6 520 157,947	102 357,075
F3	4 405	11 105	6 520 161,170	102 360,752
F4	9 405	11 105	6 520 164,930	102 357,457
F5	9 405	12 605	6 520 163,941	102 356,329
F6	13 905	12 605	6 520 167,326	102 353,362
F7	13 905	905	6 520 175,037	102 362,161
F8	9 405	905	6 520 171,653	102 365,127
F9	9 405	−95	6 520 172,312	102 365,879
F10	4 405	−95	6 520 168,552	102 369,175
F11	4 405	3 495	6 520 166,186	102 366,475
F12	−95	3 495	6 520 162,802	102 369,441

Bottenplattans kant (B), ök +6,250 (FIX −1,510)

Punkt	x	y	N	E
B1	−30	9 380	6 520 158,972	102 364,973
B2	4 370	9 380	6 520 162,281	102 362,073
B3	4 370	11 040	6 520 161,187	102 360,824
B4	9 470	11 040	6 520 165,022	102 357,463
B5	9 470	12 540	6 520 164,033	102 356,335
B6	13 840	12 540	6 520 167,320	102 353,454
B7	13 840	970	6 520 174,946	102 362,155
B8	9 340	970	6 520 171,562	102 365,121
B9	9 340	−30	6 520 172,221	102 365,873
B10	4 470	−30	6 520 168,558	102 369,083
B11	4 470	3 560	6 520 166,192	102 366,383
B12	−30	3 560	6 520 162,808	102 369,350

Plattan på marks kant (P), ök +8,500 (FIX +0,740)


Punkt	x	y	N	E
P1	0	15 900	6 520 154,697	102 360,050
P2	4 310	15 900	6 520 157,938	102 357,209
P3	4 310	11 010	6 520 161,161	102 360,886

Fixpunkt FIX, +7,760

Punkt	x	y	N	E
FIX	16 589,4	42 302,2	6 520 149,770	102 329,260

Översikt, fixpunkt

Skala 1:500

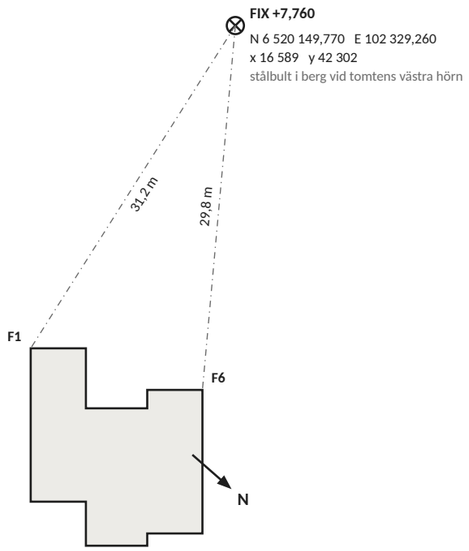

Anvisningar

1. Koordinater i SWEREF 99 12 00 (Tanums kommun), höjder i RH2000 (AR-02.2). Mått i mm. x, y är husets koordinater i K-05, med origo i mellanbjälklagets kanter.
2. Utstakning och lägeskontroll görs av certifierad mättekniker (krav i bygglovet BYGG.2025.2278).
3. Höjdreferens: fixpunkten FIX, stålbult i berg vid tomtens västra hörn, +7,760 enligt situationsplanen (nybyggnadskartan). Alla höjder anges i RH2000 och relativt bulten, och mäts från bulten med avvägningsinstrument eller laser. Mätteknikern kontrollerar bultens höjd vid utstakningen. Bultens läge är mätt ur situationsplanen (±0,1 m), avstånden i översikten är ungefärliga.
4. Läget är passat mot bygglovets situationsplan (ritning 200): husets kontur är vriden och flyttad så att den täcker husets yta i planen. Läget är därför inte noggrannare än situationsplanen, cirka ±0,1 m. Måtten mellan punkterna är exakta. Kontrollera läget mot den reviderade situationsplanen före utstakningen.
5. E = E0 + (x cos θ − y sin θ)/1 000, N = N0 + (x sin θ + y cos θ)/1 000, med θ = 131,2336°, E0 = 102 372,007, N0 = 6 520 165,177.
6. Fasadens utsida (F) ligger 95 mm utanför mellanbjälklagets kant runt hela huset, även på gavlarna: regeln 30 och beklädnaden 65 (utvändig gips 10, spikläkt 12, bärläkt 21, panel 22). Fasadstenen på källarväggarna har sin framsida i samma liv (AR-01). Måtten över regelstommen är 130 mm mindre än fasadens.
7. Bottenplattans kant (B) ligger i källarväggarnas ytterliv, 65 mm innanför fasaden. B1–B3 är plattans kant mot plattan på mark, under källarväggarna V3 och V20.
8. Plattan på mark (P, tillbyggnaden) har sin kant i mellanbjälklagets kant, 95 mm innanför fasaden. Den ansluter till källarväggarna mot B1–B3.

Teckenförklaring

- fasadens utsida (F)
- bottenplattan (B), källaren
- plattan på mark (P)
- • utsättningspunkt

Rev	Avser	Datum	Sign
A	Första utgåvan	2026-10-31	VO

PROJEKT

Fritidshus Trebodar, Resö, Tanum

FASTIGHET

Resö 2:66, Tanums kommun · BYGG.2025.2278

INNEHÅLL

Utsättning
Plan och koordinater


SKALA	FORMAT	DATUM
1:100, 1:500	A3	2026-10-31
UPPRÄTTAD	GRANSKAD	UNDERLAG
Viktor Ogeman	–	Bygglov, K-05, R-05
STATUS		REVISION
KONSTRUKTION		**A**

RITNINGSNUMMER

AR-02.1

Sektion A–A, y = 6 000 (princip)

Skala 1:50

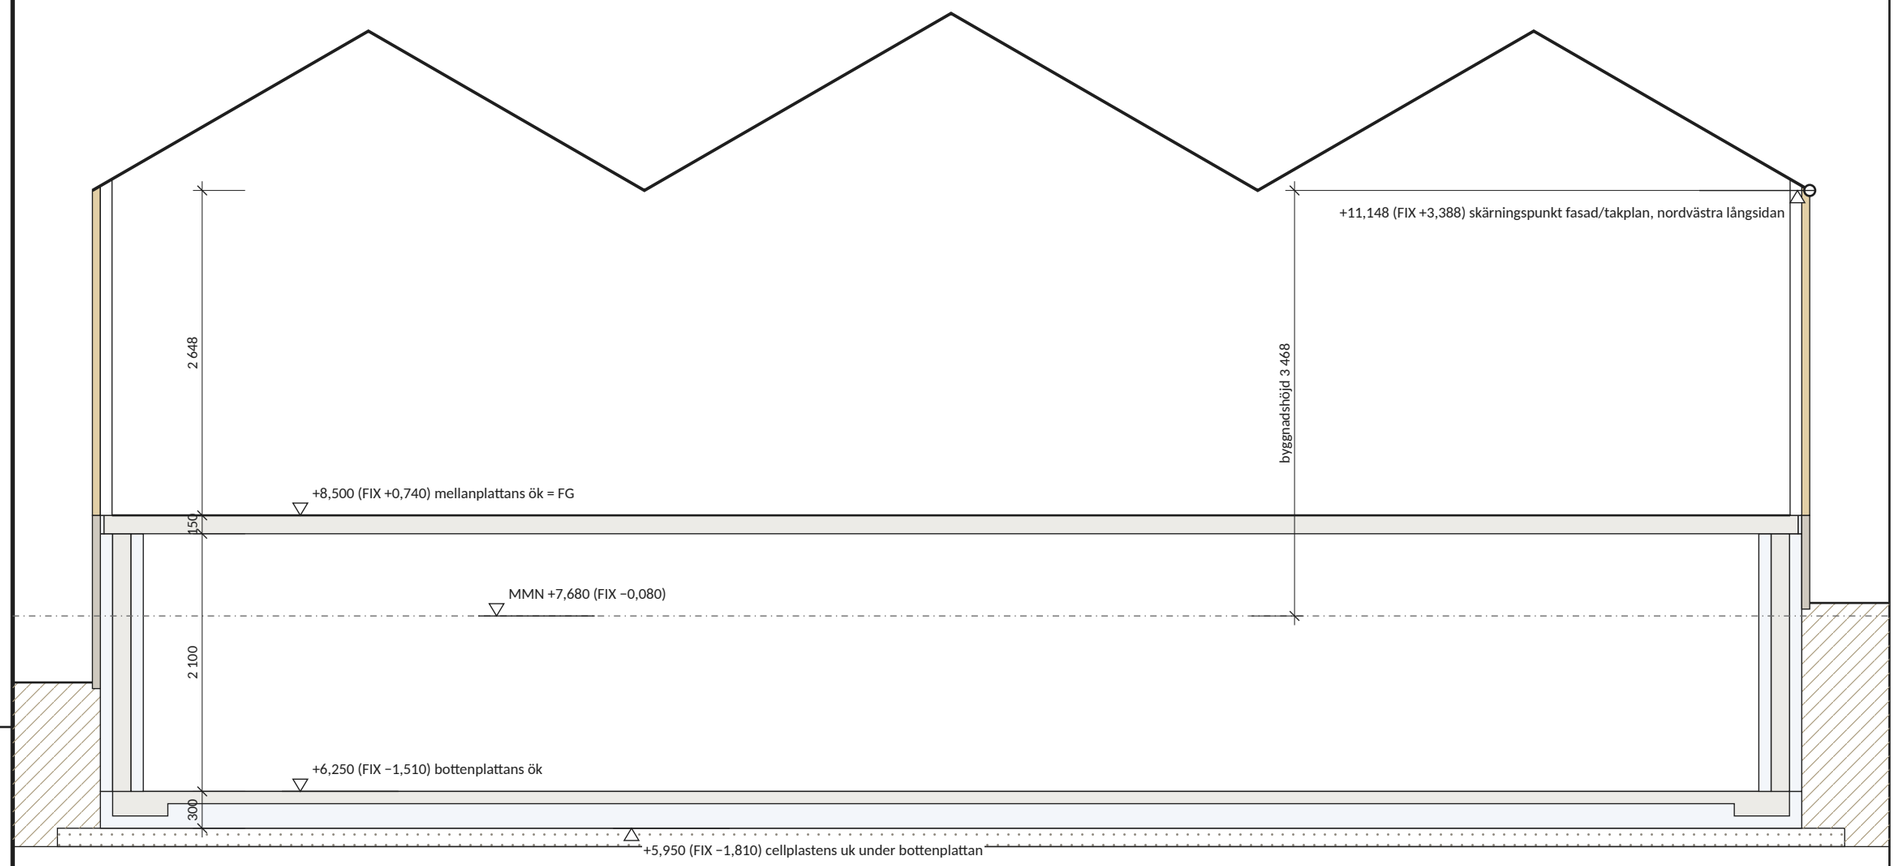

Höjder, RH2000

Nivå	RH2000 (m)	Relativt FIX (m)	Underlag
Skärningspunkt fasad/takplan, nordvästra långsidan	+11,148	+3,388	MMN + byggnadshöjd 3 468 (bygglov)
Mellanplattans överkant = FG, färdigt golv plan 1	+8,500	+0,740	bygglov; betonggolv
Fixpunkt FIX, stålbult i berg vid tomtens västra hörn	+7,760	±0	situationsplanen (nybyggnadskartan)
MMN, medelmarknivå	+7,680	−0,080	bygglov
Bottenplattans överkant	+6,250	−1,510	mellanplattans ök − 150 − 2 100 (K-05, K-06)
Cellplastens underkant under bottenplattan	+5,950	−1,810	− platta 100 − cellplast 200 (R-04)

Anvisningar

1. Höjder i RH2000 och relativt fixpunkten FIX (+7,760, stålbult i berg, se AR-02.1), i m. Mått i mm. Sektionen är en principskiss: takets uppbyggnad, takfoten och stommen visas inte. Snittets läge: AR-02.1.
2. FG +8,500 är mellanplattans överkant: betonggolv utan golvbeläggning.
3. Byggnadshöjden (bygglovet) mäts från MMN till skärningspunkten mellan fasadens utsida och takplanets ovansida på den nordvästra långsidan. Taklutning 30°.
4. Bottenplattans cellplast läggs på avjämnad makadam (R-04).

Teckenförklaring

- takplanets ovansida
- MMN
- betong
- cellplast
- fasadsten (AR-01)
- beklädnad, plan 1
- makadam
- mark

Rev	Avser	Datum	Sign
A	Första utgåvan	2026-10-31	VO

PROJEKT

Fritidshus Trebodar, Resö, Tanum

FASTIGHET

Resö 2:66, Tanums kommun · BYGG.2025.2278

INNEHÅLL

Utsättning
Sektion och höjder

SKALA	FORMAT	DATUM
1:50	A3	2026-10-31
UPPRÄTTAD	GRANSKAD	UNDERLAG
Viktor Ogeman	–	Bygglov, K-05, R-05
STATUS		REVISION
KONSTRUKTION		**A**

RITNINGSNUMMER

AR-02.2