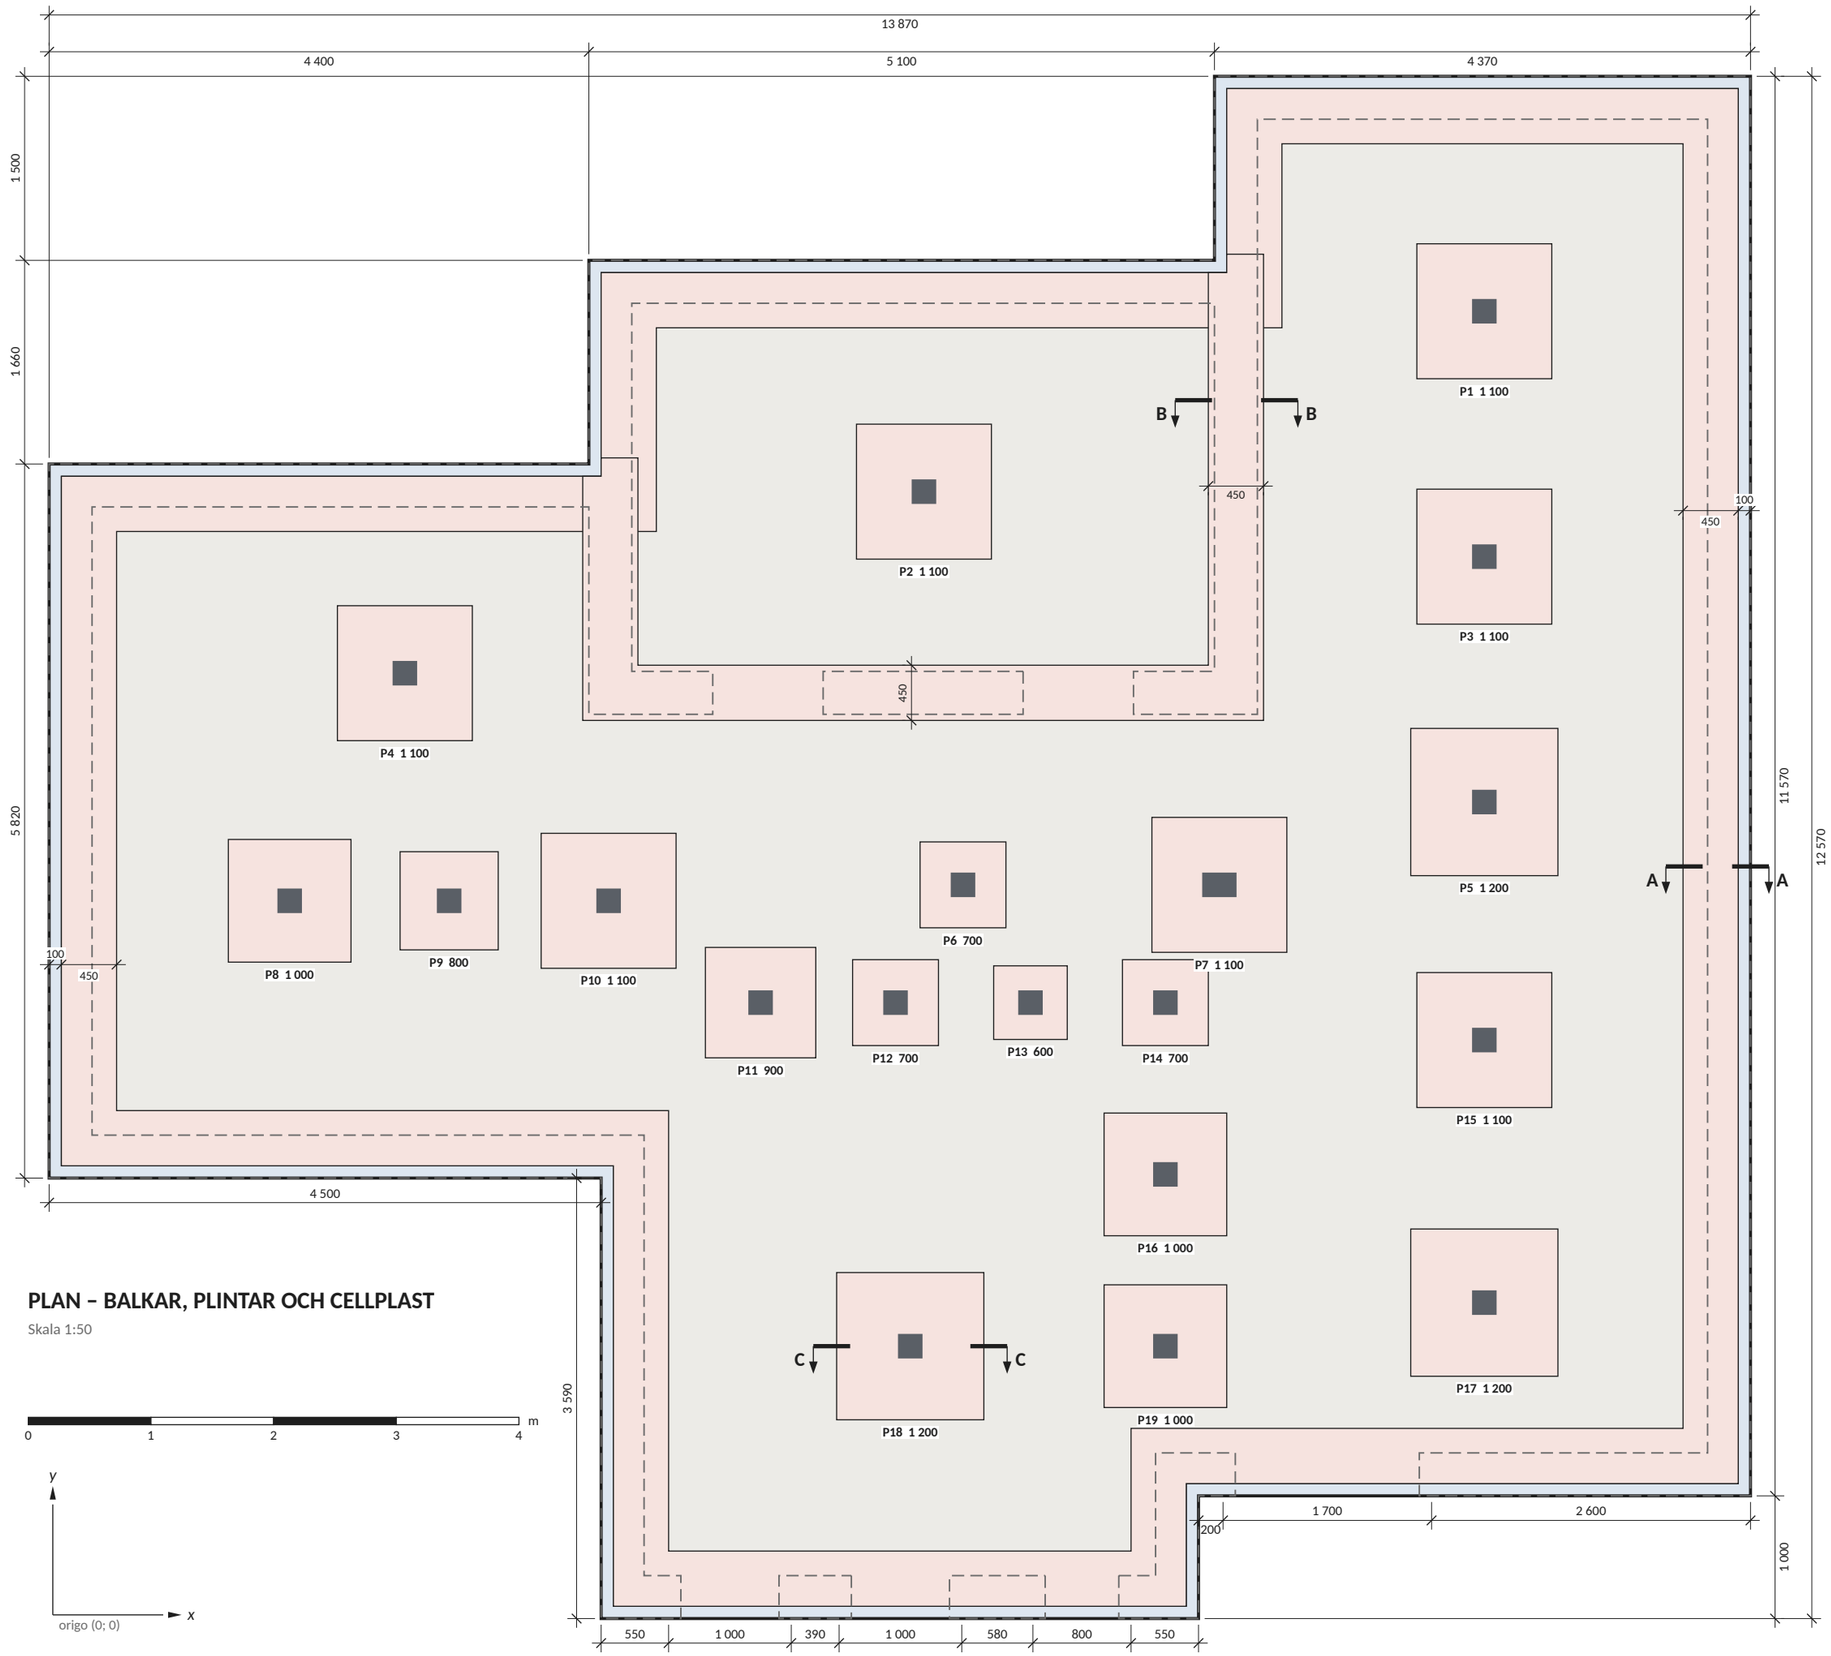



## PLAN – BALKAR, PLINTAR OCH CELLPLAST

Skala 1:50

### Anvisningar

1. Bottenplatta L300 (K-06): 100 mm betong C25/30 på 200 mm cellplast S100 i två skikt med åldringsbeständig plastfolie emellan. Kantbalkar 450 × 200 i L-element L300 med fot av S300 längs hela kanten; balkar under innerväggarna 450 × 200 och plintar under rören, lika höga, på 100 mm S300. Bara två kvaliteter: S100 under plattan och S300 under balkar och plintar. Samma uppbyggnad i hela källaren.
2. L-elementens ytterkant ligger i väggarnas ytterliv (R-04.1), som planens mått går till. Betongen börjar innanför L-elementets yttre ben, 100 mm, i kärnans yttre yta: väggens yttre cellplast står på benet och kärnan på kantbalken (detalj D, sektion A). Koordinater i mm enligt K-05, höjder från bottenplattans överkant.
3. Plintarna är kvadratiska och centrerade under rörets mitt (P7: mitt mellan de två rören). Sida och mitt enligt tabellen; mått från väggarna till rörens mitt på R-04.1.
4. Underlag: makadam på sprängt berg, avjämnat och packat. Dränledningen läggs runt huset innan cellplasten läggs (K-06).
5. Armering R-05.2, sektioner och förteckningar R-05.3. Fotplåtar och rör R-04.5.

### Teckenförklaring

- kantbalk, balk och plint, 200 hög, på 100 S300
- platta 100 på 200 S100
- L-elementets yttre ben, 100, i väggarnas ytterliv
- väggarna (R-04)
- fotplåt (R-04.5)

### Plintar (sida och mitt)

| Plint | Sida | x | y | Anm |
|---|---|---|---|---|
| P1 | 1 100 | 11 670 | 10 625 | |
| P2 | 1 100 | 7 102 | 9 155 | |
| P3 | 1 100 | 11 670 | 8 625 | |
| P4 | 1 100 | 2 870 | 7 675 | |
| P5 | 1 200 | 11 670 | 6 625 | |
| P6 | 700 | 7 420 | 5 950 | |
| P7 | 1 100 | 9 510 | 5 950 | två rör, fotplåt 280 × 200 eller 2 st 140 × 200 (R-04.5) |
| P8 | 1 000 | 1 931 | 5 820 | |
| P9 | 800 | 3 231 | 5 820 | |
| P10 | 1 100 | 4 531 | 5 820 | |
| P11 | 900 | 5 770 | 4 990 | |
| P12 | 700 | 6 870 | 4 990 | |
| P13 | 600 | 7 970 | 4 990 | |
| P14 | 700 | 9 070 | 4 990 | |
| P15 | 1 100 | 11 670 | 4 685 | |
| P16 | 1 000 | 9 070 | 3 590 | |
| P17 | 1 200 | 11 670 | 2 545 | |
| P18 | 1 200 | 6 990 | 2 190 | |
| P19 | 1 000 | 9 070 | 2 190 | |

### Ritningsförteckning R-05

| Ritning | Innehåll | Skala |
|---|---|---|
| R-05.1 | Plan, balkar, plintar och cellplast | 1:50 |
| R-05.2 | Armering | 1:50 |
| R-05.3 | Sektioner, detaljer och förteckningar | 1:10, 1:20, 1:50 |

| Rev | Avser | Datum | Sign |
|---|---|---|---|
| A | Första utgåvan | 2026-10-16 | VO |

PROJEKT

**Fritidshus Trebodar, Resö, Tanum**

FASTIGHET

Resö 2:66, Tanums kommun · BYGG.2025.2278


INNEHÅLL

**Bottenplatta**
**Plan, balkar, plintar och cellplast**

| SKALA | FORMAT | DATUM |
|---|---|---|
| 1:50 | A3 | 2026-10-16 |
| UPPRÄTTAD | GRANSKAD | UNDERLAG |
| Viktor Ogeman | – | K-06 rev A, K-05 rev A |
| STATUS | | REVISION |
| **KONSTRUKTION** | | **A** |

RITNINGSNUMMER

# R-05.1

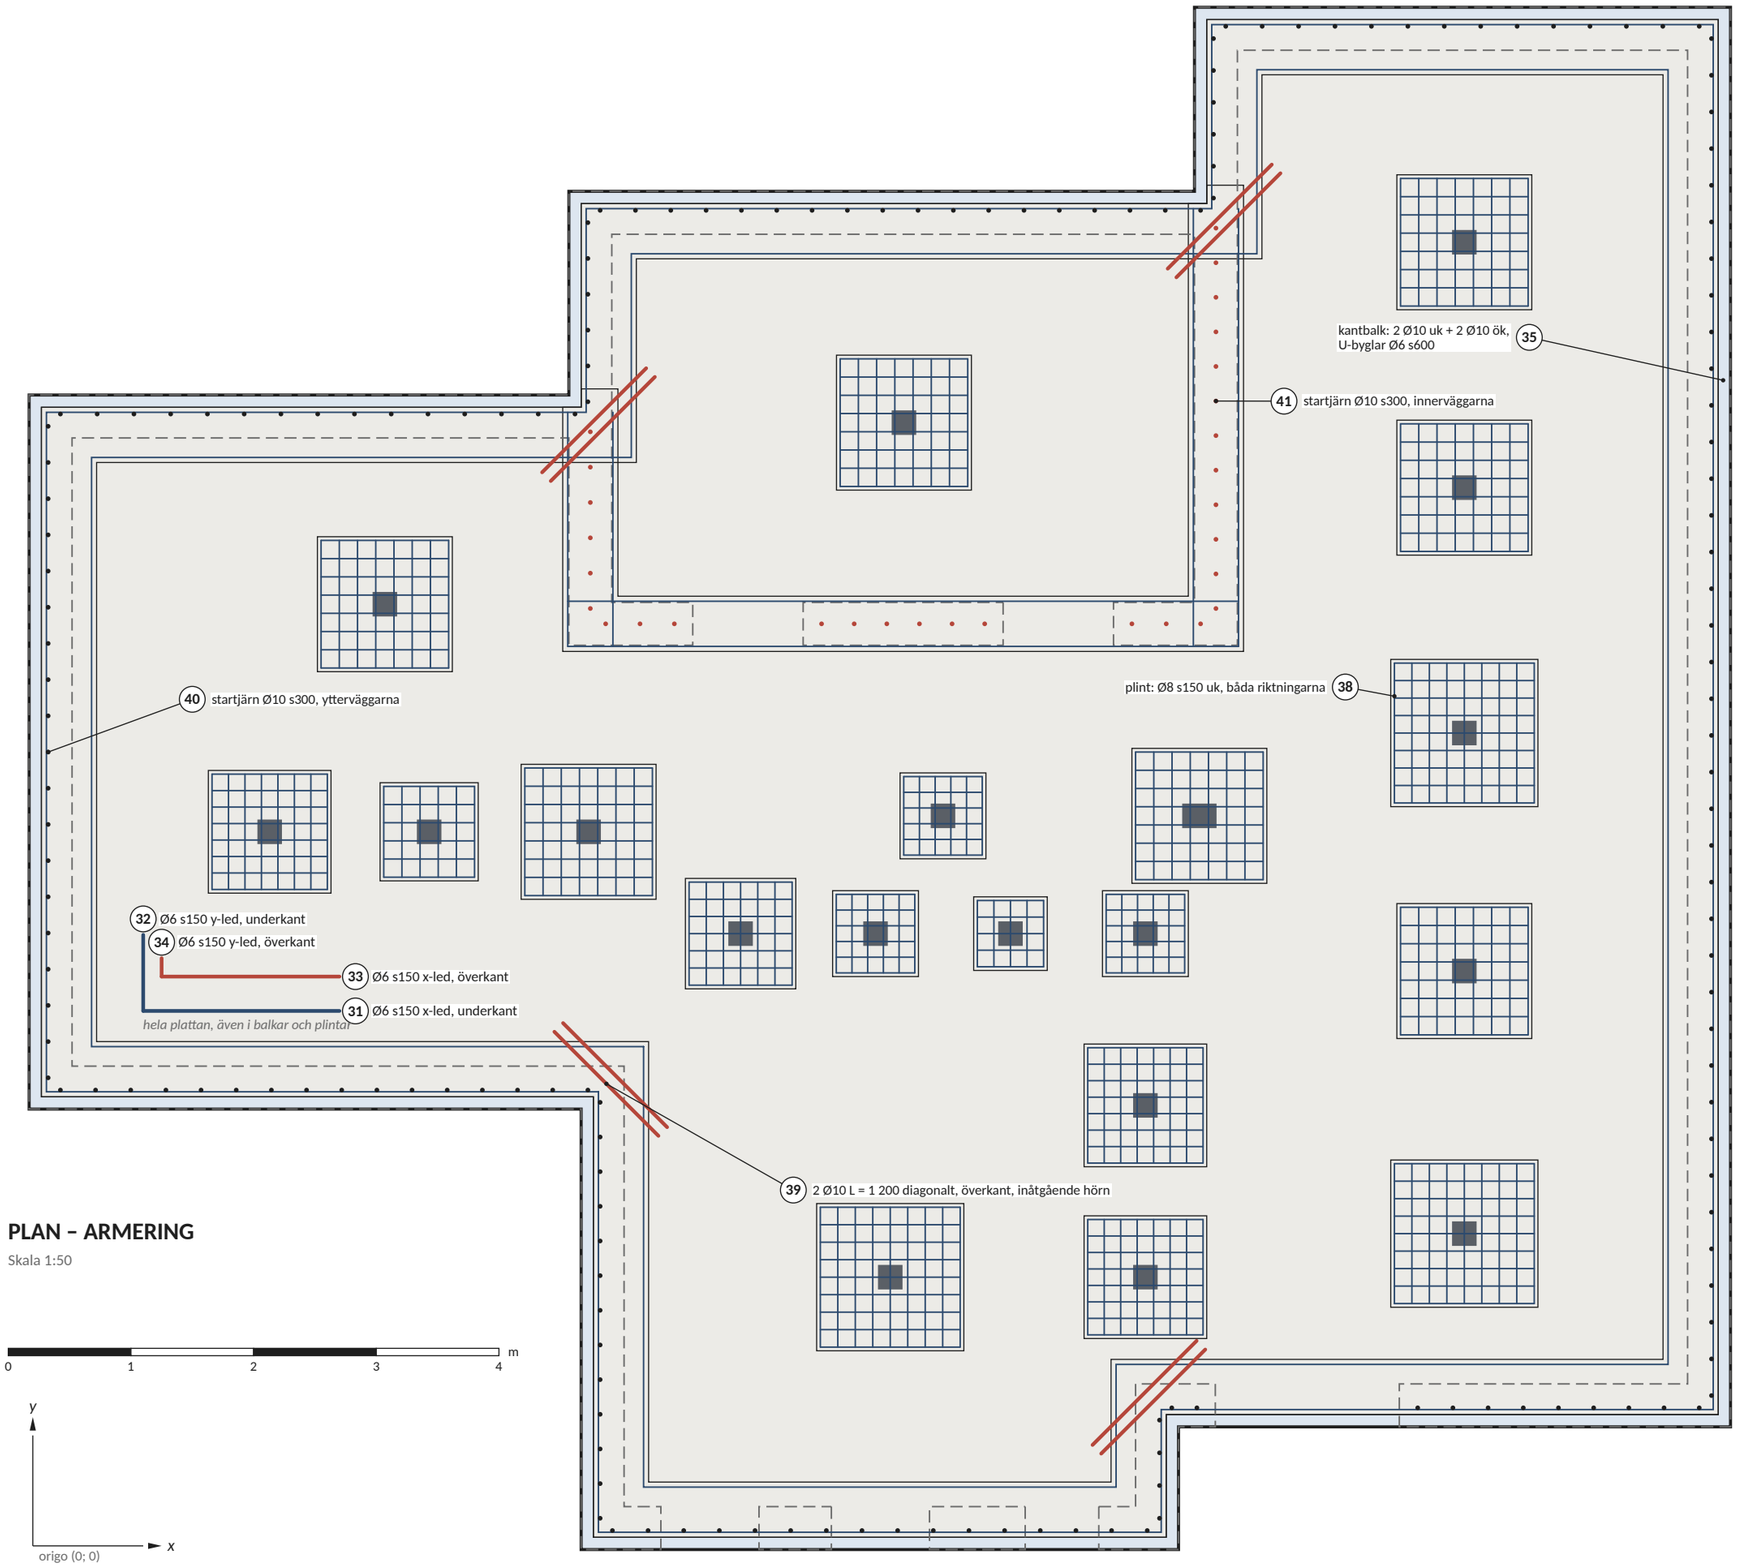


## PLAN – ARMERING

Skala 1:50

## Anvisningar

1. Betong C25/30, armering B500B. Täckande skikt: 30 mm mot cellplasten (distanser) och 25 mm i överkant.
2. Nät Ø6 s150 i under- och överkant i hela plattan (31–34), också genom balkarna och plintarna. Golvvärmeslangarna fästs i underkantsnätet. Skarvlängd Ø6 400.
3. Kantbalkar och balkar under innerväggarna: 2 Ø10 i underkant (35) på byglarna och 2 Ø10 i överkant (36) under överkantsnätet, U-byglar Ø6 s600 (37). Skarvlängd Ø10 650; i hörnen bockas järnen eller skarvas med vinkeljärn. Innerbalkarnas järn förs in i kantbalken och i den korsande balken.
4. Plintar: Ø8 s150 i underkant, båda riktningarna (38). Fotplåten gjuts in kant i kant med plintens överkant (R-04.5); näten läggs fritt från svetsbultarna.
5. Inåtgående hörn: 2 Ø10, L = 1 200, i överkant diagonalt, 150 och 250 mm från hörnet (39).
6. Startjärn Ø10 s300, 1 200 upp och 500 i balken: den lodräta delen och foten, 330, på byglarna. Ytterväggarna på utsidan (40, svarta), med foten vinkelrätt in i kantbalken (Sundolitt), också under bröstningarna vid F1–F3; innerväggarna i kärnans mitt (41, röda), med foten längs balken. Väggarnas armering: R-04.
7. Ytan under väggarna ruggas före väggarnas gjutning (K-06).

## Teckenförklaring

- armering i underkant / balkjärn
- armering i överkant (diagonaljärn)
- startjärn, ytterväggarna
- startjärn, innerväggarna
- (31) positionsnummer (stålförteckning R-05.3)

| Rev | Avser | Datum | Sign |
|---|---|---|---|
| A | Första utgåvan | 2026-10-16 | VO |

PROJEKT

**Fritidshus Trebodar, Resö, Tanum**

FASTIGHET

Resö 2:66, Tanums kommun · BYGG.2025.2278

INNEHÅLL

**Bottenplatta**
**Armering**


| SKALA | FORMAT | DATUM |
|---|---|---|
| 1:50 | A3 | 2026-10-16 |

| UPPRÄTTAD | GRANSKAD | UNDERLAG |
|---|---|---|
| Viktor Ogeman | – | K-06 rev A, K-05 rev A |

| STATUS | REVISION |
|---|---|
| **KONSTRUKTION** | **A** |


RITNINGSNUMMER

**R-05.2**

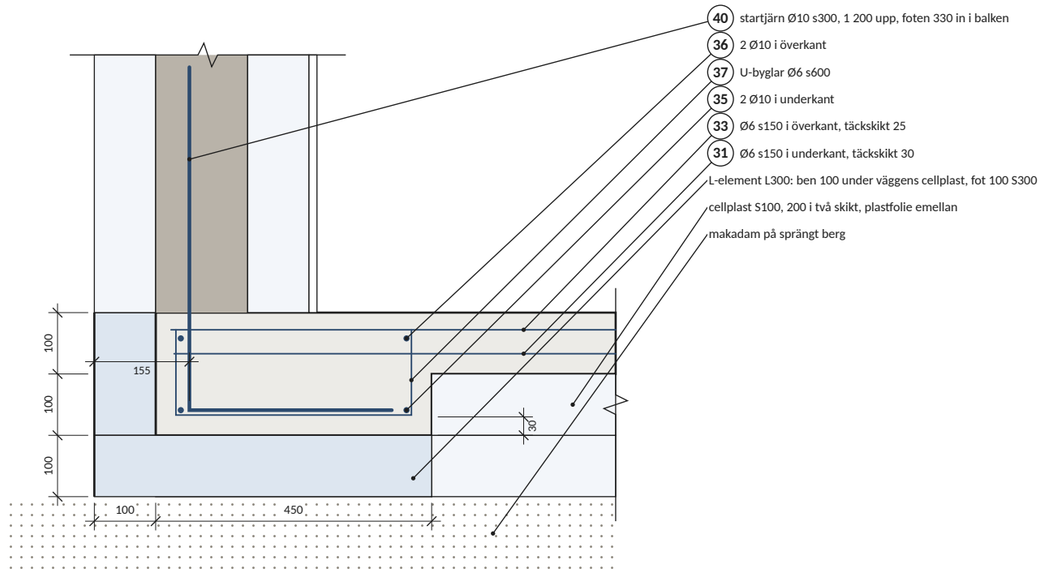



**SEKTION A–A Kantbalk i L-element (V14)**

Skala 1:10

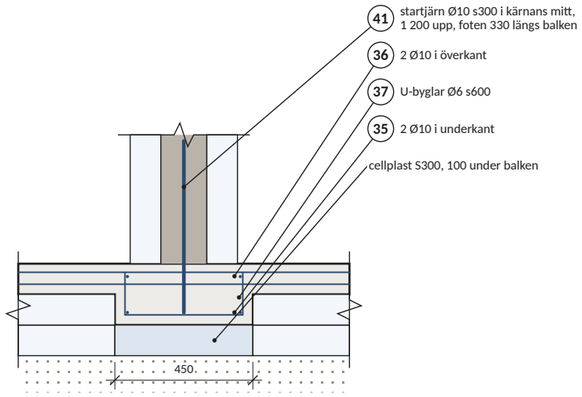



**SEKTION B–B Balk under innervägg (V15)**

Skala 1:20

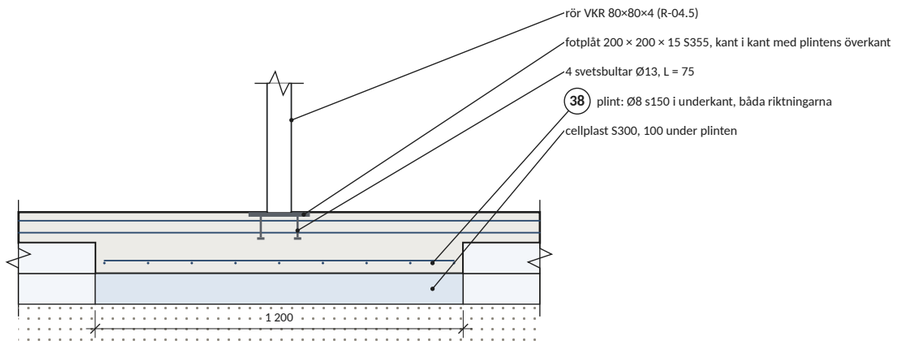


**SEKTION C–C Plint under rör (P18, 1 200)**

Skala 1:20

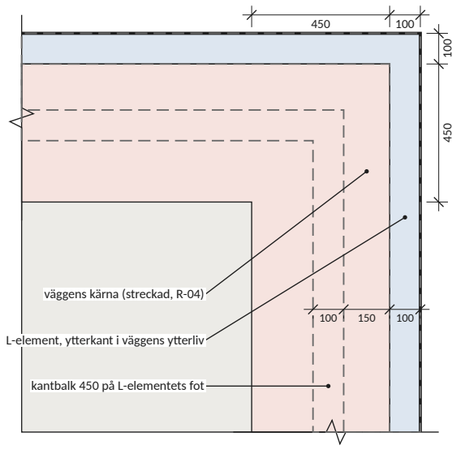


**DETALJ D Yttre hörn i plan (V1/V14)**

Skala 1:20

Samma vid alla hörn: L-elementets ytterkant i väggens ytterliv.

## Stålförteckning, B500B

| Pos | Ø | Form | s | Antal | L (mm) | Total (m) | Vikt (kg) | Anm |
|---|---|---|---|---|---|---|---|---|
| 31 | Ø6 | rak | s150 | 82 | var. | 848 | 188 | UK x-led, hela plattan |
| 32 | Ø6 | rak | s150 | 91 | var. | 840 | 186 | UK y-led, hela plattan |
| 33 | Ø6 | rak | s150 | 82 | var. | 848 | 188 | ÖK x-led, hela plattan |
| 34 | Ø6 | rak | s150 | 91 | var. | 840 | 186 | ÖK y-led, hela plattan |
| 35 | Ø10 | rak | – | 2 per balk | var. | 129 | 80 | balkar, underkant |
| 36 | Ø10 | rak | – | 2 per balk | var. | 129 | 80 | balkar, överkant |
| 37 | Ø6 | U 145+390+145 | s600 | 102 | 700 | 71 | 16 | byglar i balkarna |
| 38 | Ø8 | rak | s150 | 286 | var. | 272 | 108 | plintar, underkant |
| 39 | Ø10 | rak | – | 8 | 1 200 | 10 | 6 | inåtgående hörn, ÖK |
| 40 | Ø10 | L 1 360+330 | s300 | 176 | 1 690 | 297 | 184 | ytterväggarna, utsidan |
| 41 | Ø10 | L 1 360+330 | s300 | 30 | 1 690 | 51 | 31 | innerväggarna, mitt |
| | | | | | | Summa | 1 253 | Ø6: 765 + Ø8: 108 + Ø10: 380 |

## Anvisningar

1. Utförande (K-06): spräng och avjämna berget och lägg makadam. Lägg dränledningen. Lägg L-elementen (fot S300) med ytterkanten i väggarnas ytterliv, S300 under innerbalkarna och plintarna och S100 under plattan i två skikt med plastfolie emellan. Skär ur cellplasten för balkar och plintar.
2. Armera, lägg golvvärmeslangarna och fixera fotplåtarna i läge och höjd. Gjut bottenplattan med balkar och plintar i en gjutning; fotplåtarna gjuts in kant i kant med plintarnas överkant. Rugga ytan under väggarna.
3. Kontrollera före gjutning: armeringens läge och täckskikt (distanser), plintarnas läge och storlek, fotplåtarnas läge och höjd (±5 mm), startjärnen.
4. Plattan behöver inga fogar; golvbeläggning och tätskikt ska tåla krympsprickor (K-06).
5. Plan R-05.1, armering R-05.2.

## Teckenförklaring

- betong C25/30
- cellplast S100
- L-element (fot S300), S300 under balkar och plintar
- väggens betongkärna (R-04)
- armering

## Cellplast

| | Utförande | Mängd | Anm |
|---|---|---|---|
| S100 | 2 × 100 mm, plastfolie emellan | 81,0 m² | under plattan |
| S300 | 100 mm | 23,3 m² | under innerbalkarna och plintarna |
| L-element | L300, 550 × 300, ben 100, fot S300 | 52,9 m | längs hela kanten, ytterkant i väggarnas ytterliv |

| Rev | Avser | Datum | Sign |
|---|---|---|---|
| A | Första utgåvan | 2026-10-16 | VO |

PROJEKT

**Fritidshus Trebodar, Resö, Tanum**

FASTIGHET

Resö 2:66, Tanums kommun · BYGG.2025.2278

INNEHÅLL

**Bottenplatta**
**Sektioner, detaljer och förteckningar**

| SKALA | FORMAT | DATUM |
|---|---|---|
| 1:10, 1:20, 1:50 | A3 | 2026-10-16 |
| UPPRÄTTAD: Viktor Ogeman | GRANSKAD: – | UNDERLAG: K-06 rev A, K-05 rev A |
| STATUS: **KONSTRUKTION** | | REVISION: **A** |

RITNINGSNUMMER

**R-05.3**