
Plan, utsättningspunkter

Skala 1:100

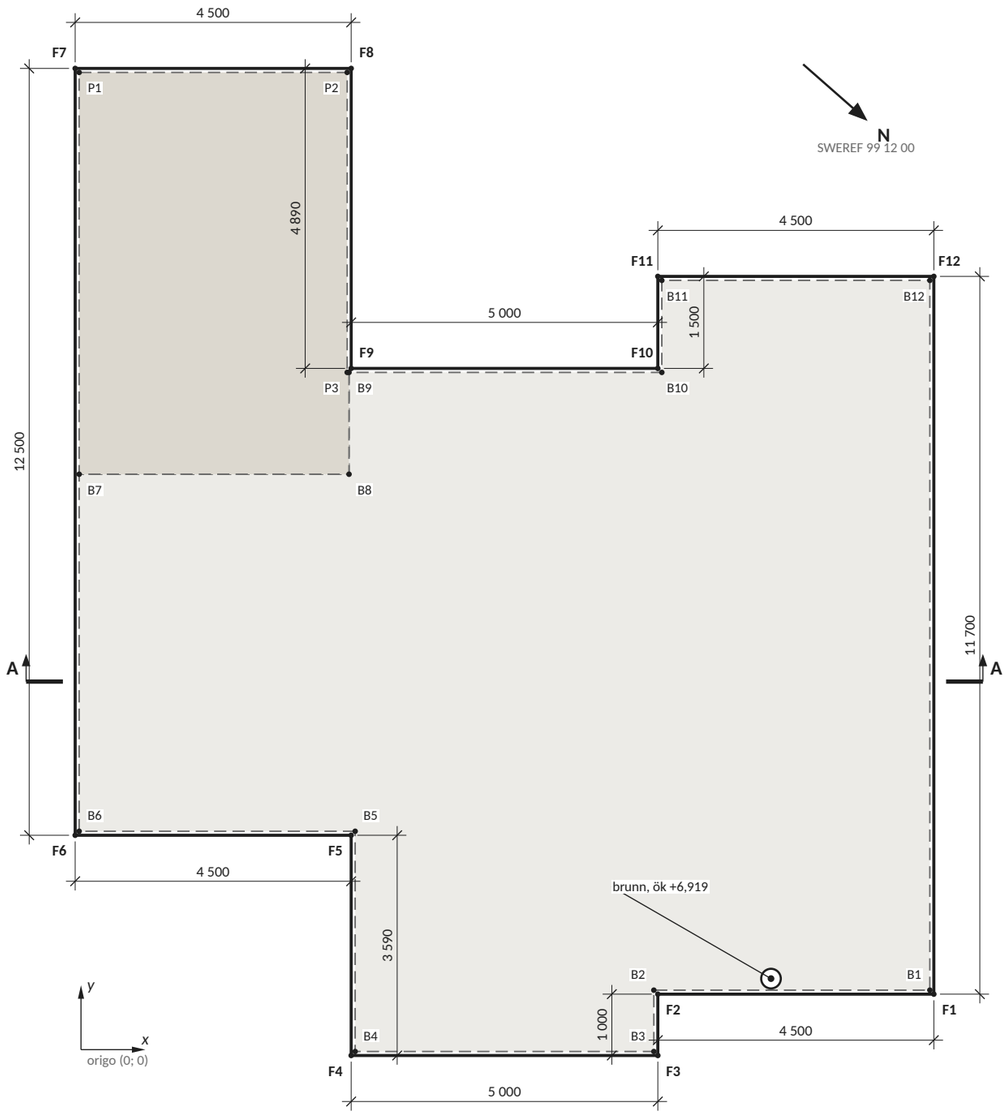

Utsättningspunkter, SWEREF 99 12 00

x, y i mm (K-05), N, E och höjder i m. Höjder i RH2000 och relativt fixpunkten FIX (+7,760).

Fasadens utsida (F)

Punkt	x	y	N	E
F1	13 905	905	6 520 175,041	102 362,162
F2	9 405	905	6 520 171,660	102 365,132
F3	9 405	−95	6 520 172,320	102 365,883
F4	4 405	−95	6 520 168,563	102 369,183
F5	4 405	3 495	6 520 166,194	102 366,485
F6	−95	3 495	6 520 162,813	102 369,455
F7	−95	15 995	6 520 154,564	102 360,062
F8	4 405	15 995	6 520 157,945	102 357,093
F9	4 405	11 105	6 520 161,172	102 360,767
F10	9 405	11 105	6 520 164,929	102 357,468
F11	9 405	12 605	6 520 163,939	102 356,341
F12	13 905	12 605	6 520 167,321	102 353,371

Bottenplattans kant (B), L-elementens ytterkant, ök +6,250 (FIX −1,510)

Punkt	x	y	N	E
B1	13 840	970	6 520 174,949	102 362,156
B2	9 340	970	6 520 171,568	102 365,126
B3	9 340	−30	6 520 172,228	102 365,877
B4	4 470	−30	6 520 168,569	102 369,091
B5	4 470	3 560	6 520 166,200	102 366,393
B6	−30	3 560	6 520 162,819	102 369,363
B7	−30	9 380	6 520 158,978	102 364,990
B8	4 370	9 380	6 520 162,284	102 362,086
B9	4 370	11 040	6 520 161,189	102 360,839
B10	9 470	11 040	6 520 165,021	102 357,474
B11	9 470	12 540	6 520 164,031	102 356,347
B12	13 840	12 540	6 520 167,314	102 353,463

Plattan på marks kant (P), L-elementens ytterkant, ök +8,500 (FIX +0,740)

Punkt	x	y	N	E
P1	−30	15 930	6 520 154,656	102 360,068
P2	4 340	15 930	6 520 157,939	102 357,185
P3	4 340	11 040	6 520 161,166	102 360,859

Fixpunkt FIX, +7,760


Punkt	x	y	N	E
FIX	16 628,8	42 302,7	6 520 149,770	102 329,260

Dräneringsbrunnen (befintlig, inmätt), ök +6,919, utgående rör ø110 ök +5,759

Punkt	x	y	N	E
Brunn	11 250	1 158	6 520 172,879	102 363,724

Översikt, fixpunkt

Skala 1:500

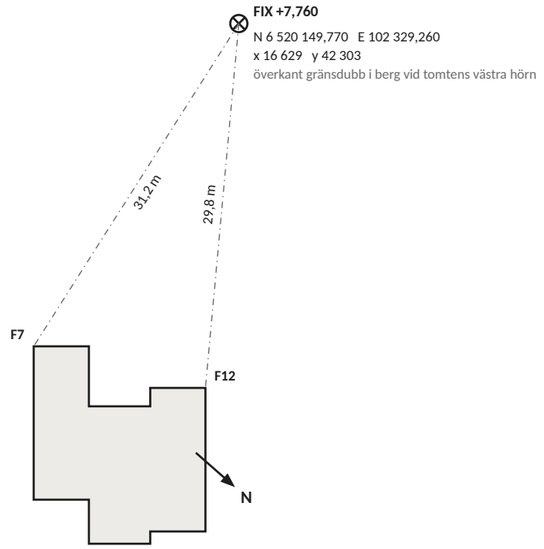

Anvisningar

1. Koordinater i SWEREF 99 12 00 (Tanums kommun), höjder i RH2000 (AR-02.2). Mått i mm. x, y är husets koordinater, samma som i K-05 och på R-03–R-06: origo i skärningen mellan mellanbjälklagets kanter x = 0 och y = 0.
2. Utstakning och lägeskontroll görs av certifierad mättekniker (krav i bygglovet BYGG.2025.2278).
3. Höjdreferens: fixpunkten FIX, byggfixen på nybyggnadskartan (2025-11-12): överkant gränsdubb i berg vid tomtens västra hörn, +7,760. Alla höjder anges i RH2000 och relativt dubben. Dubbens läge är angivet i cm.
4. Fasadens hörn F1–F12 är utsättningsdata. Bottenplattans (B) och plattan på marks (P) punkter är beräknade med samma läge:
5. E = E0 + (x cos θ − y sin θ)/1 000, N = N0 + (x sin θ + y cos θ)/1 000, med θ = 131,290900°, E0 = 102 372,0179, N0 = 6 520 165,1905.
6. Plattan på mark (P, tillbyggnaden) byggs med L-element, 500 mm höga. P är L-elementens ytterkant, i linje med bottenplattans kant vid B7–B9.

Teckenförklaring

- fasadens utsida (F)
- bottenplattan (B), L-elementens ytterkant
- plattan på mark (P), L-elementens ytterkant
- utsättningspunkt
- dräneringsbrunn (befintlig, inmätt) med utgående rör ø110

Rev	Avser	Datum	Sign
A	Första utgåvan	2026-10-31	VO

PROJEKT

Fritidshus Trebodar, Resö, Tanum

FASTIGHET

Resö 2:66, Tanums kommun · BYGG.2025.2278

INNEHÅLL

Utsättning
Plan och koordinater


SKALA	FORMAT	DATUM
1:100, 1:500	A3	2026-10-31
UPPRÄTTAD	GRANSKAD	UNDERLAG
Viktor Ogeman	–	Bygglov, NBK, K-05, R-05
STATUS		REVISION
KONSTRUKTION		**A**

RITNINGSNUMMER

AR-02.1

Sektion A–A, y = 6 000 (princip)

Skala 1:50

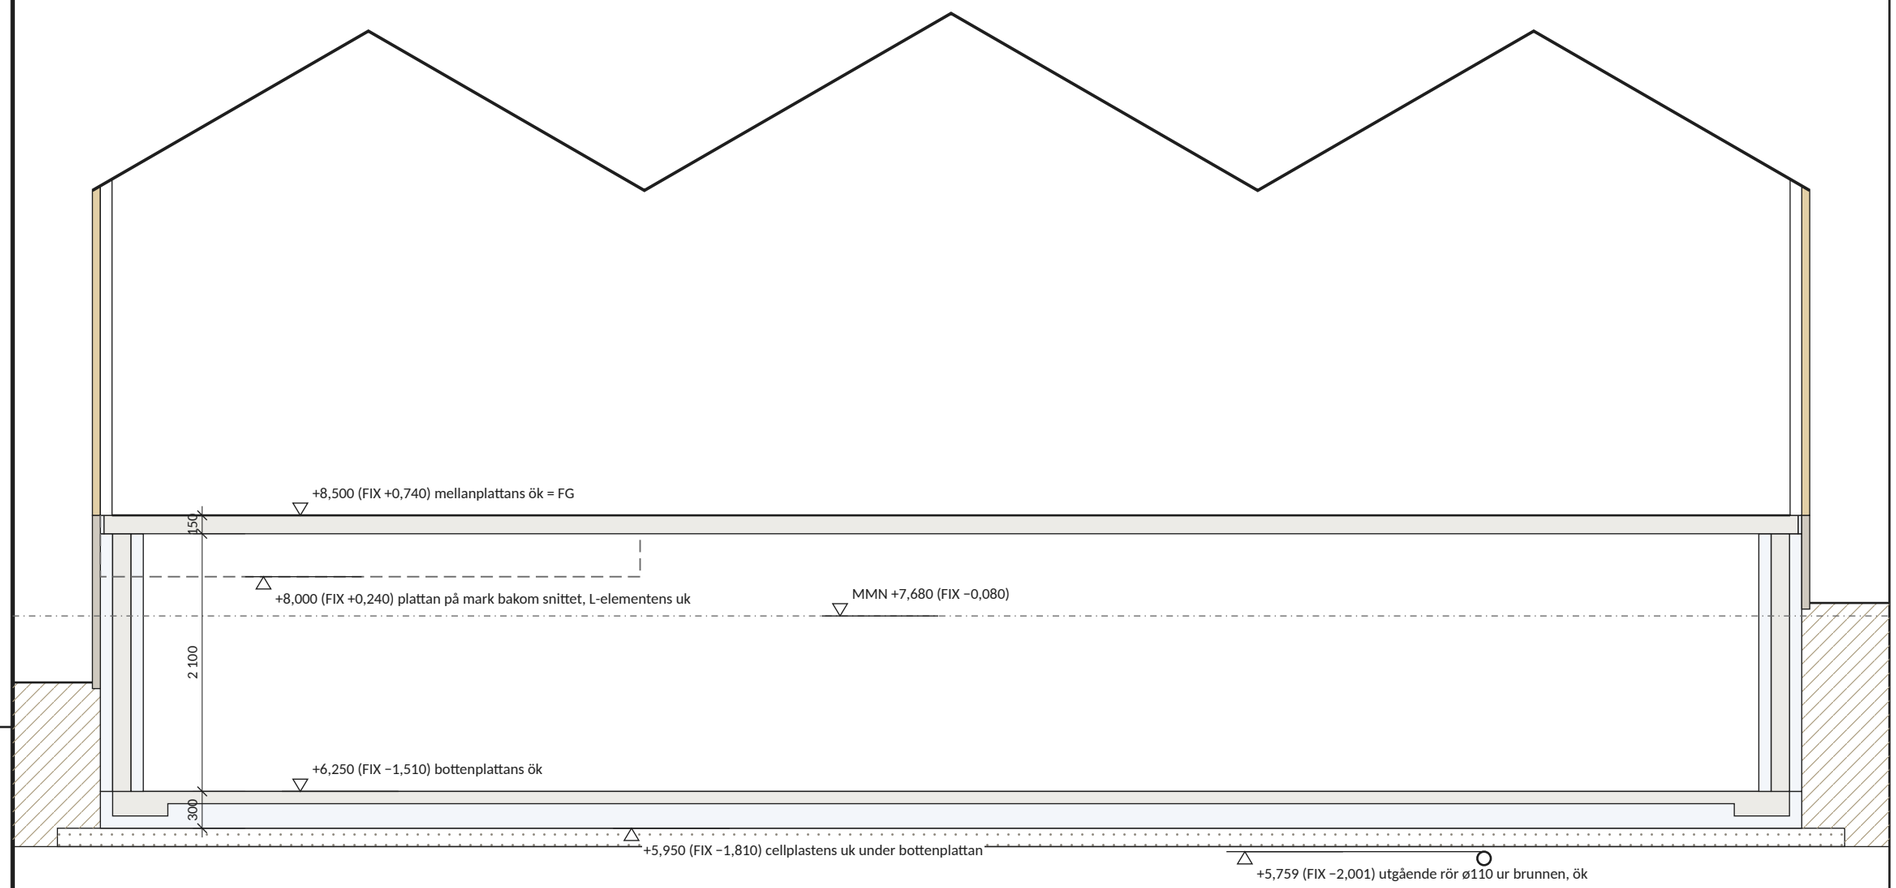

Höjder, RH2000

Nivå	RH2000 (m)	Relativt FIX (m)	Underlag
Mellanplattans överkant = FG, färdigt golv plan 1	+8,500	+0,740	bygglov; betonggolv
Golvet i det gamla huset	+8,473	+0,713	inmätt 2026-11-01 (GNSS)
Plattan på mark: L-elementens och cellplastens underkant	+8,000	+0,240	plattans ök − L-element 500
Fixpunkt FIX, överkant gränsdubb i berg vid tomtens västra hörn	+7,760	±0	nybyggnadskartan 2025-11-12 (byggfix)
MMN, medelmarknivå	+7,680	−0,080	bygglov
Dräneringsbrunnen (befintlig), överkant	+6,919	−0,841	inmätt 2026-11-01 (GNSS)
Bottenplattans överkant	+6,250	−1,510	mellanplattans ök − 150 − 2 100 (K-05, K-06)
Cellplastens underkant under bottenplattan	+5,950	−1,810	− platta 100 − cellplast 200 (R-04)
Utgående rör ø110 ur brunnen, överkant: avledning för dränvattnet	+5,759	−2,001	brunnens ök − 1 160

Anvisningar

1. Höjder i RH2000 och relativt fixpunkten FIX (+7,760, gränsdubb i berg, se AR-02.1), i m. Mått i mm. Sektionen är en principskiss. Snittets läge: AR-02.1.
2. FG +8,500 är mellanplattans överkant.
3. Bottenplattans cellplast läggs på avjämnad makadam (R-04).
4. Dräneringsbrunnen är befintlig och inmätt (läge AR-02.1, y = 1 158); dess utgående rör ø110 är ritat i brunnens x. Överkant rör = brunnens överkant − 1 160.

Teckenförklaring

- takplanets ovansida
- MMN
- plattan på mark bakom snittet (L-element 500)
- betong
- cellplast
- fasadsten (AR-01)
- beklädnad, plan 1
- makadam
- mark

Rev	Avser	Datum	Sign
A	Första utgåvan	2026-10-31	VO

PROJEKT

Fritidshus Trebodar, Resö, Tanum

FASTIGHET

Resö 2:66, Tanums kommun · BYGG.2025.2278

INNEHÅLL

Utsättning
Sektion och höjder

SKALA	FORMAT	DATUM
1:50	A3	2026-10-31

UPPRÄTTAD	GRANSKAD	UNDERLAG
Viktor Ogeman	–	Bygglov, NBK, K-05, R-05

STATUS	REVISION
KONSTRUKTION	**A**

RITNINGSNUMMER

AR-02.2